

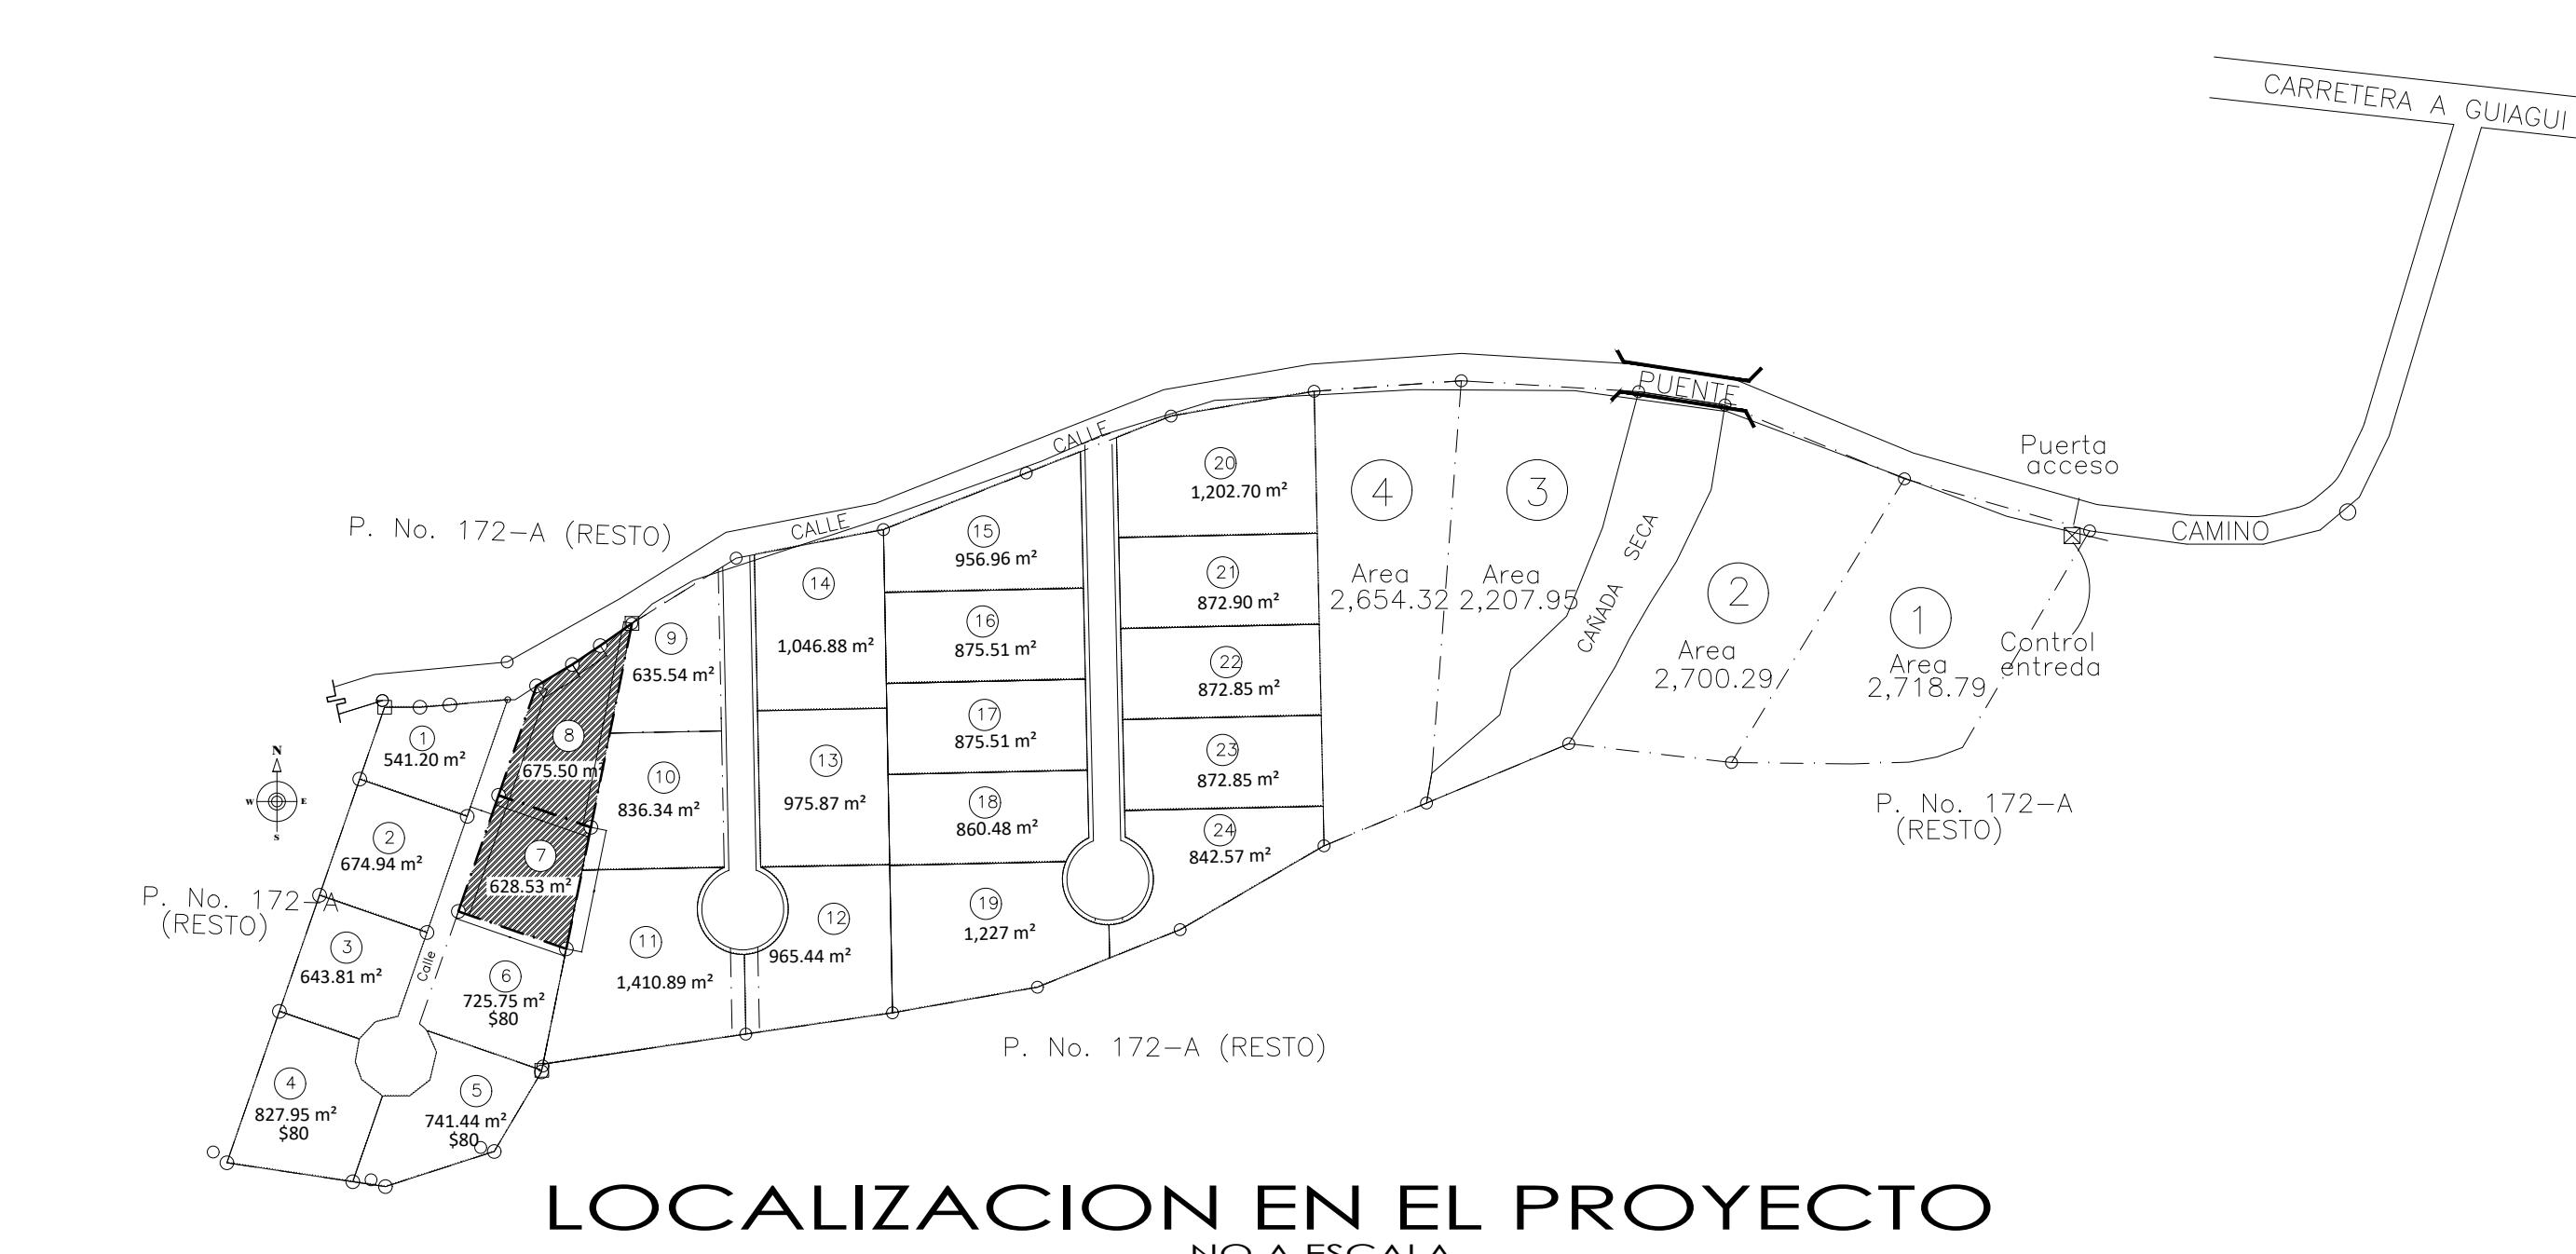
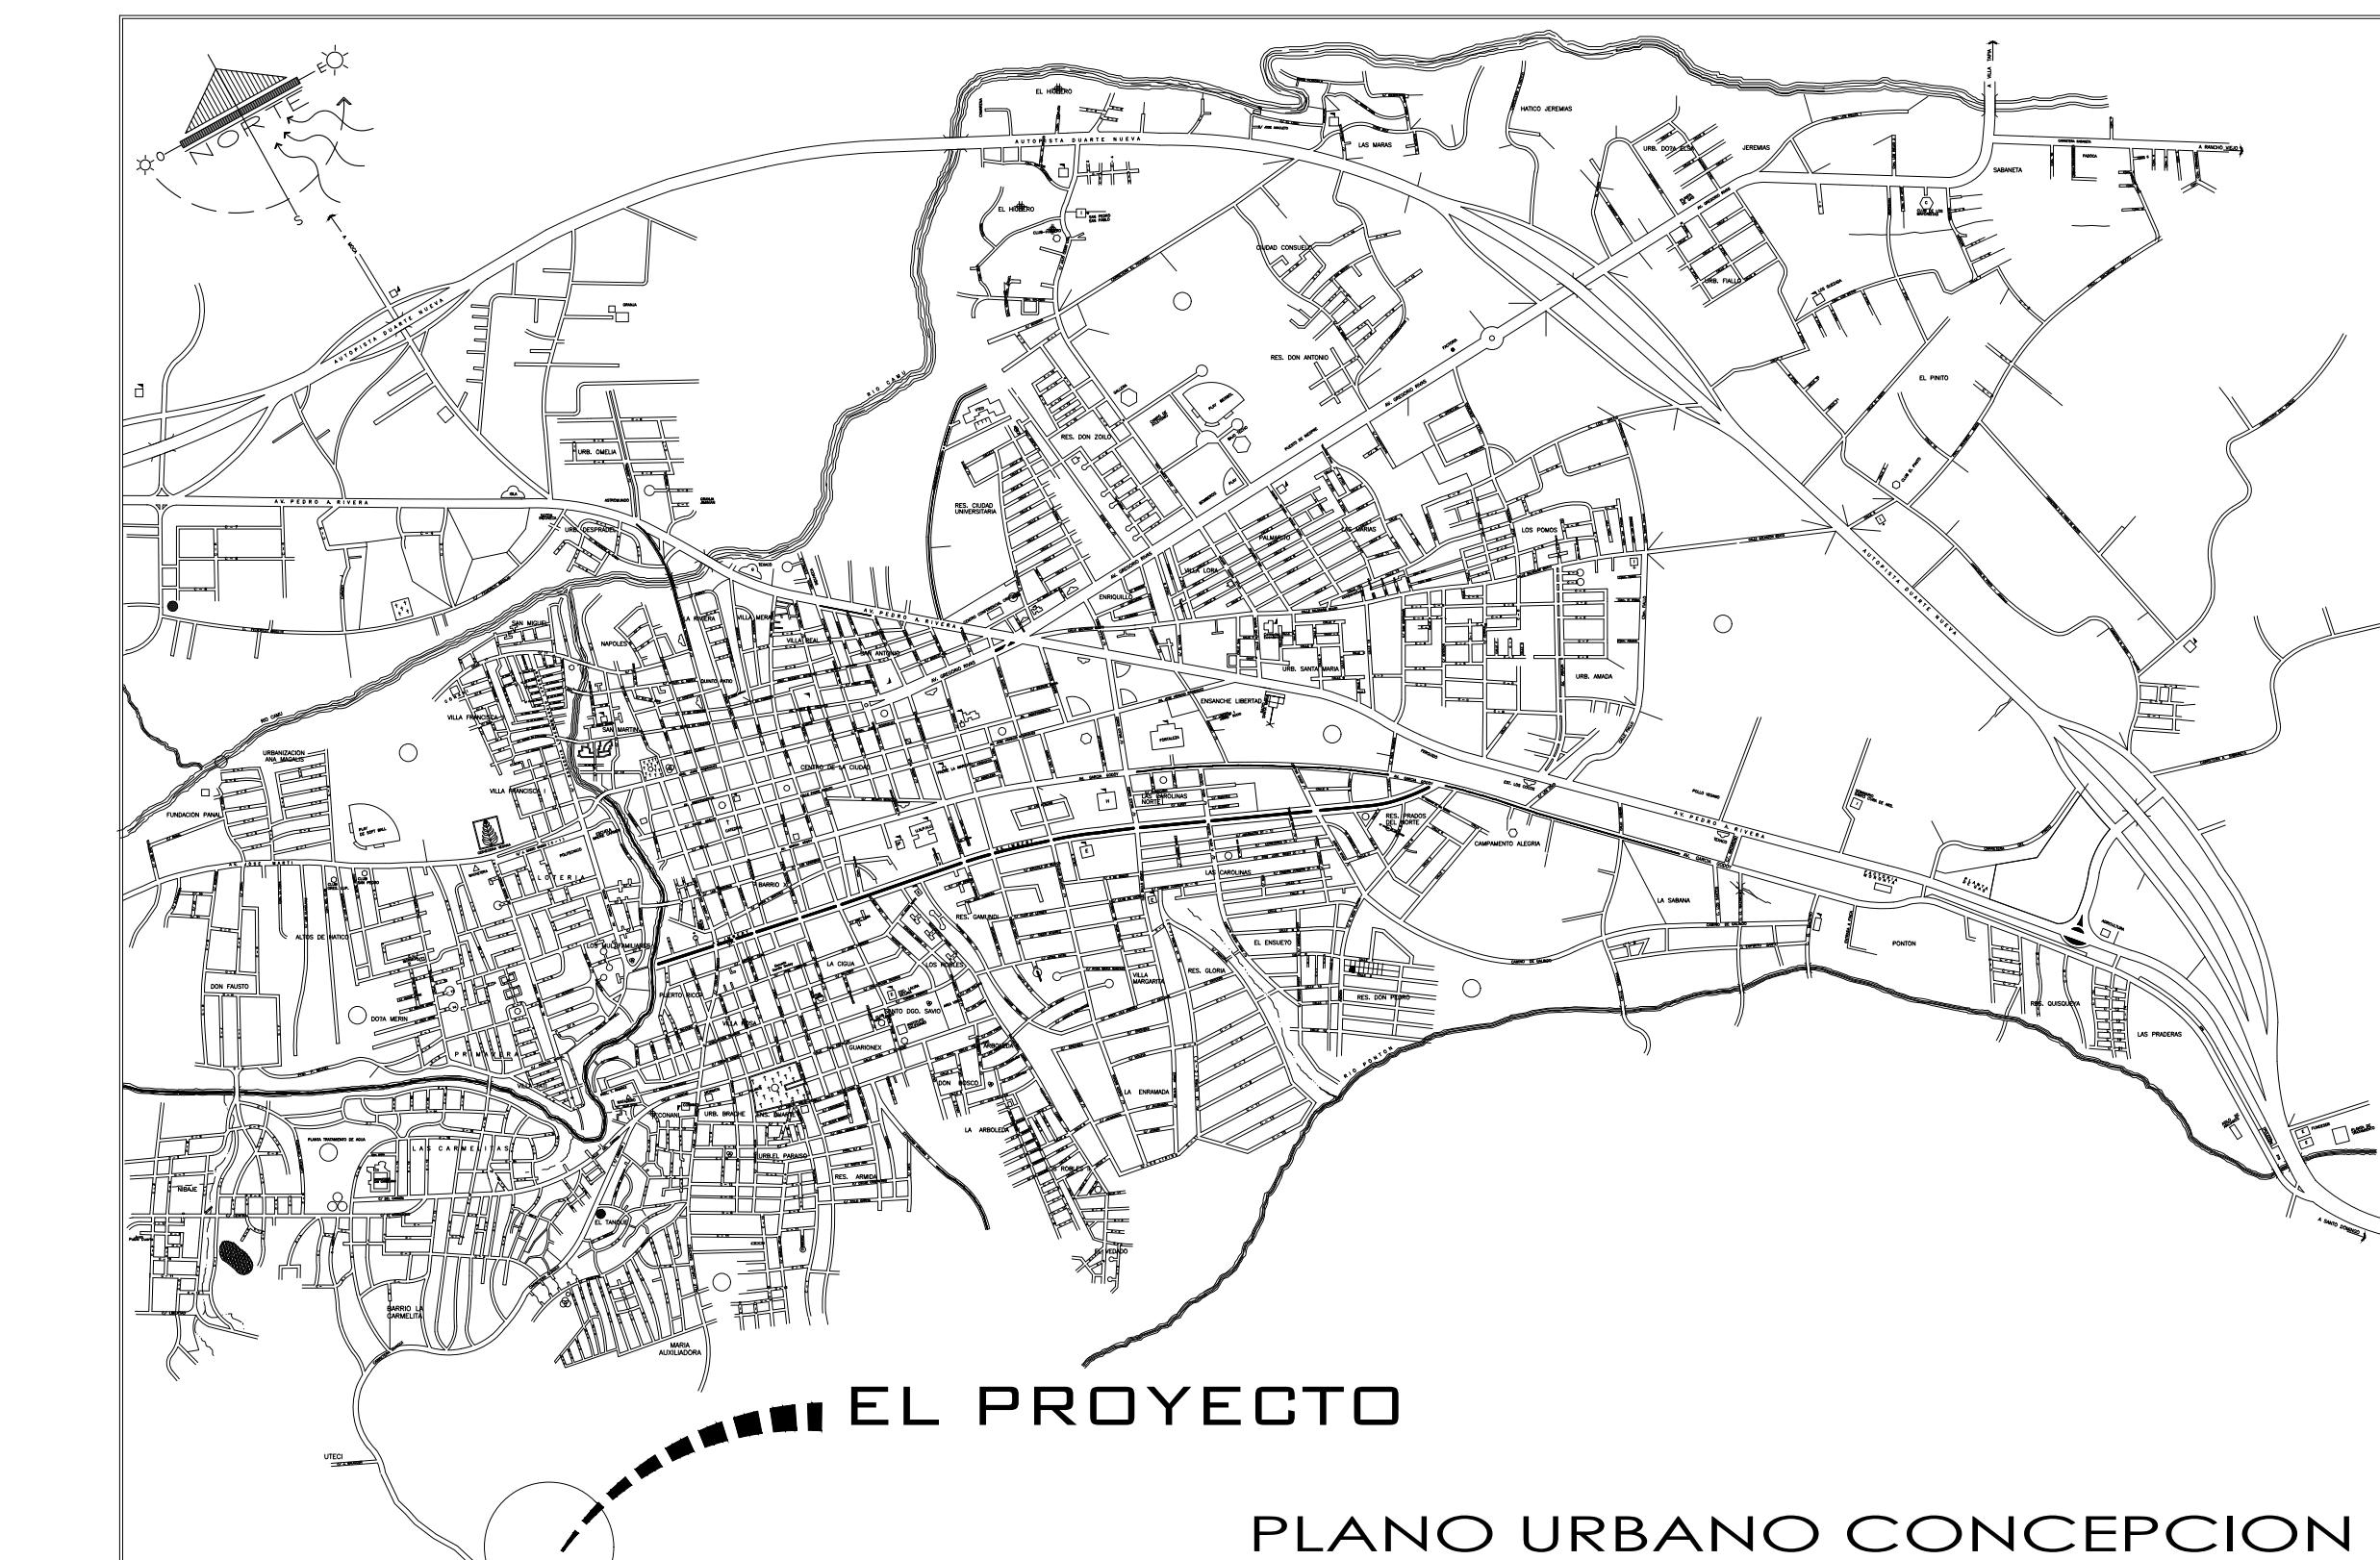


LOCALIZACION EN EL PAIS
NO A ESCALA

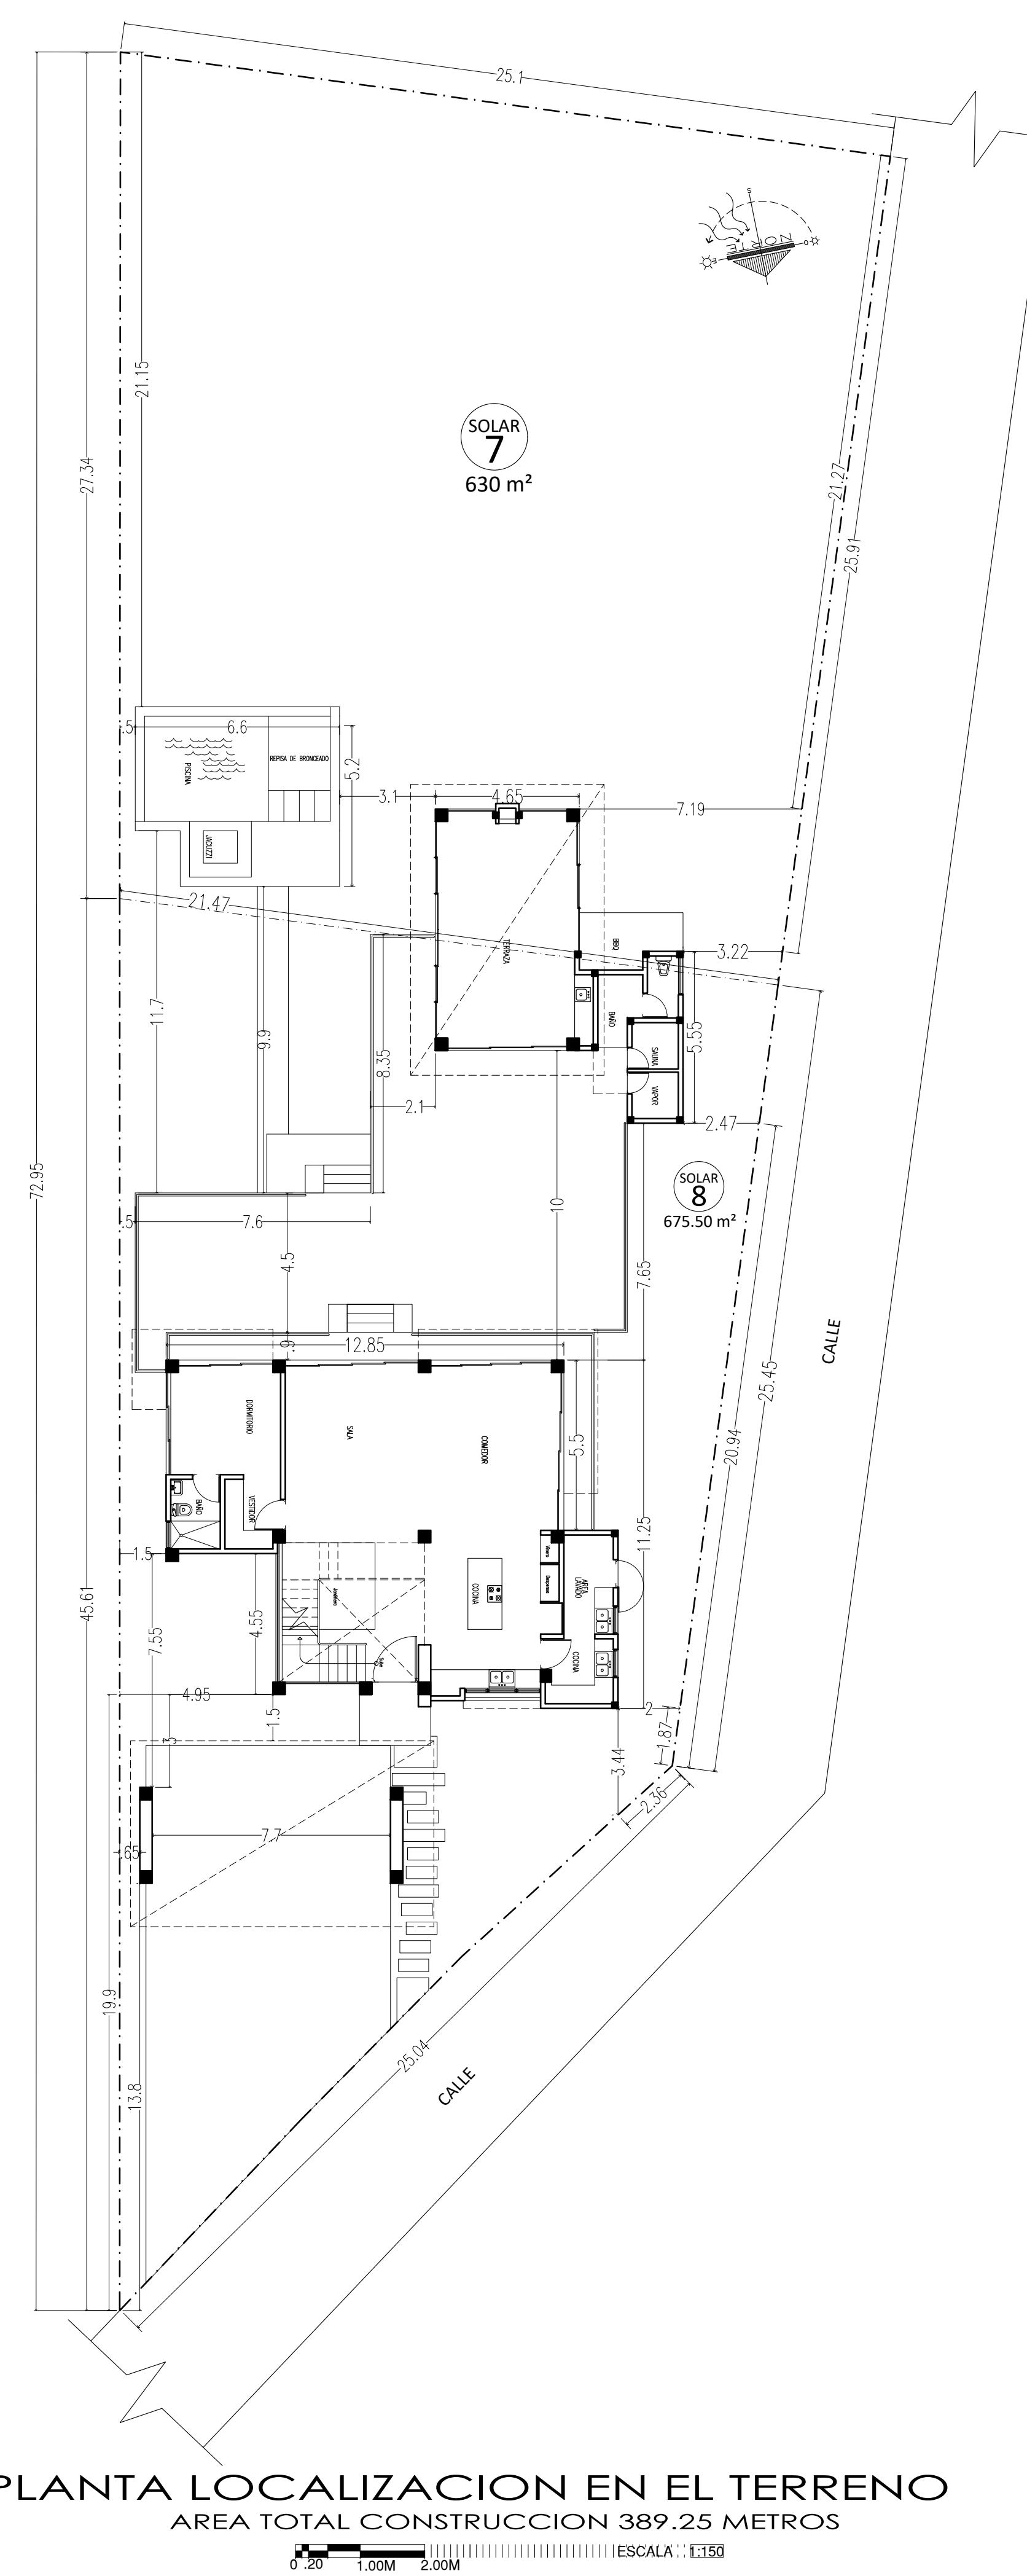


LOCALIZACION EN EL CARIBE
NO A ESCALA

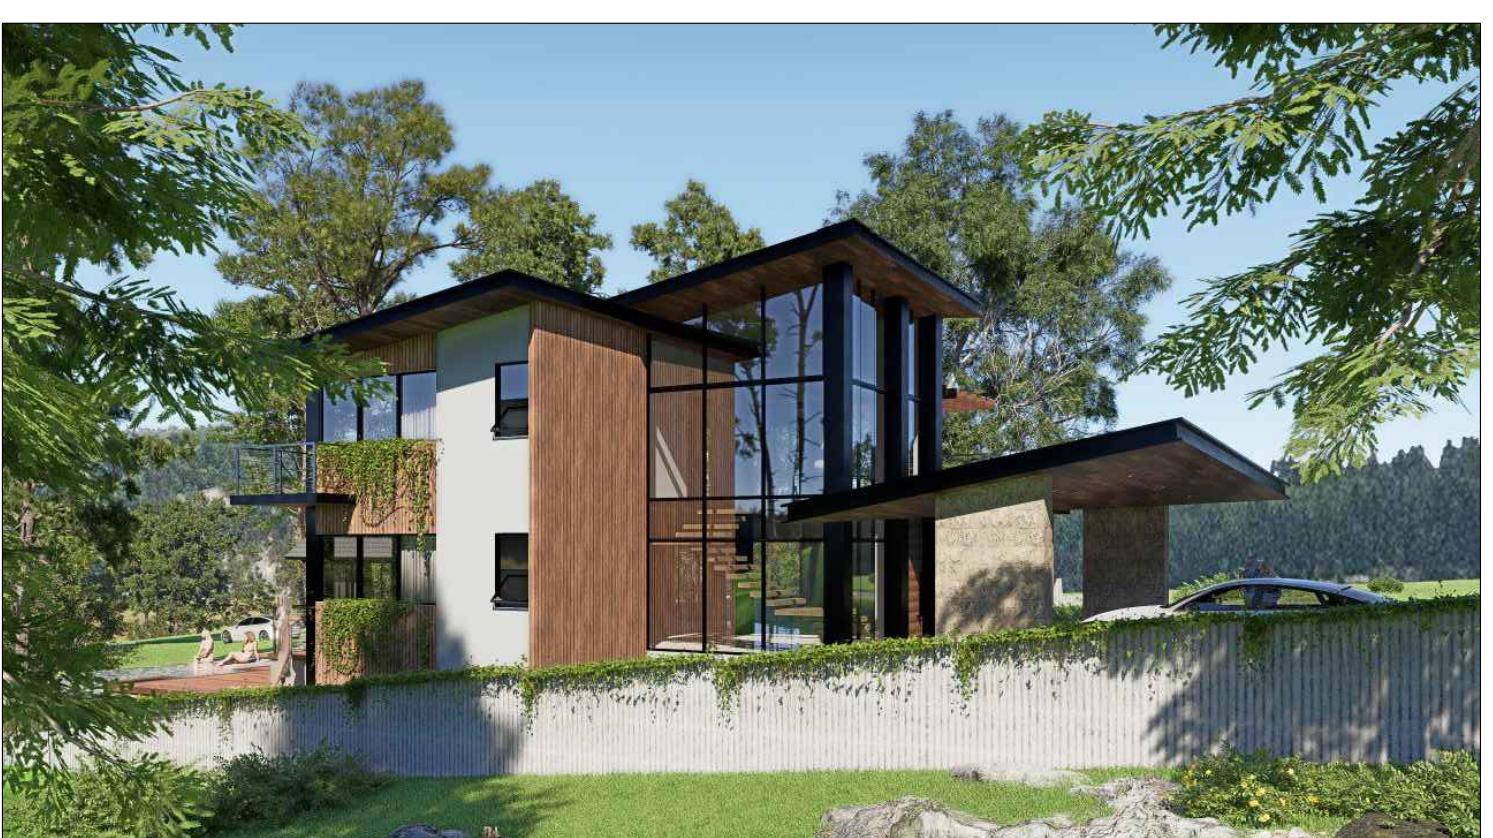


Este proyecto es propiedad única y exclusivamente del arquitecto EDDY J. LOPEZ C. el cual sede la ejecución con estos planos de un solo proyecto en un solo lugar específico. Si usted es destinatario o no de este proyecto, debe abstenerse totalmente de copiar, reproducir, distribuir, ceder a un familiar o particular, robar conceptos del mismo. La violación a esta disposición sería procesada legalmente con todo el peso de la justicia Dominicana por violar la ley sobre derecho de autor.

Villa Beato Reyes	LOCALIZACION: GUIAGUI, LA VEGA		
PROPIETARIOS:			
JOSE LUIS BEATO PEÑA CED. 402-2763926-3	FIRMA	JOSELYN ANTONELIA REYES A. CED. 402-2737538-9	FIRMA
DISEÑO ARQUITECTONICO: SHERYL LOPEZ R. CODA: 46298			
DISEÑO SANITARIO: ING. FRANK FELIZ LOPEZ CODA: 19796			
DISEÑO ESTRUCTURAL: HIPOLITO MORONITA LLONG CODA: 4166			
DISEÑO ELECTRICO: HIPOLITO MORONITA LLONG CODA: 4166			
ARQ. EDDY LOPEZ C. 809-399 8344	DIBUJO : 018 U 0 EL ARQUITECTURA AVENIDA AMERICA #4 LA VEGA 809-573-7056 809-399-8344	ESCALA : 1:150	HOJA # 1/23
RESPONSABLE DEL PROYECTO: ARQUITECTO: EDDY J. LOPEZ CODA: 13.638	FECHA: 1 - 9 - 2021	INDICADA	

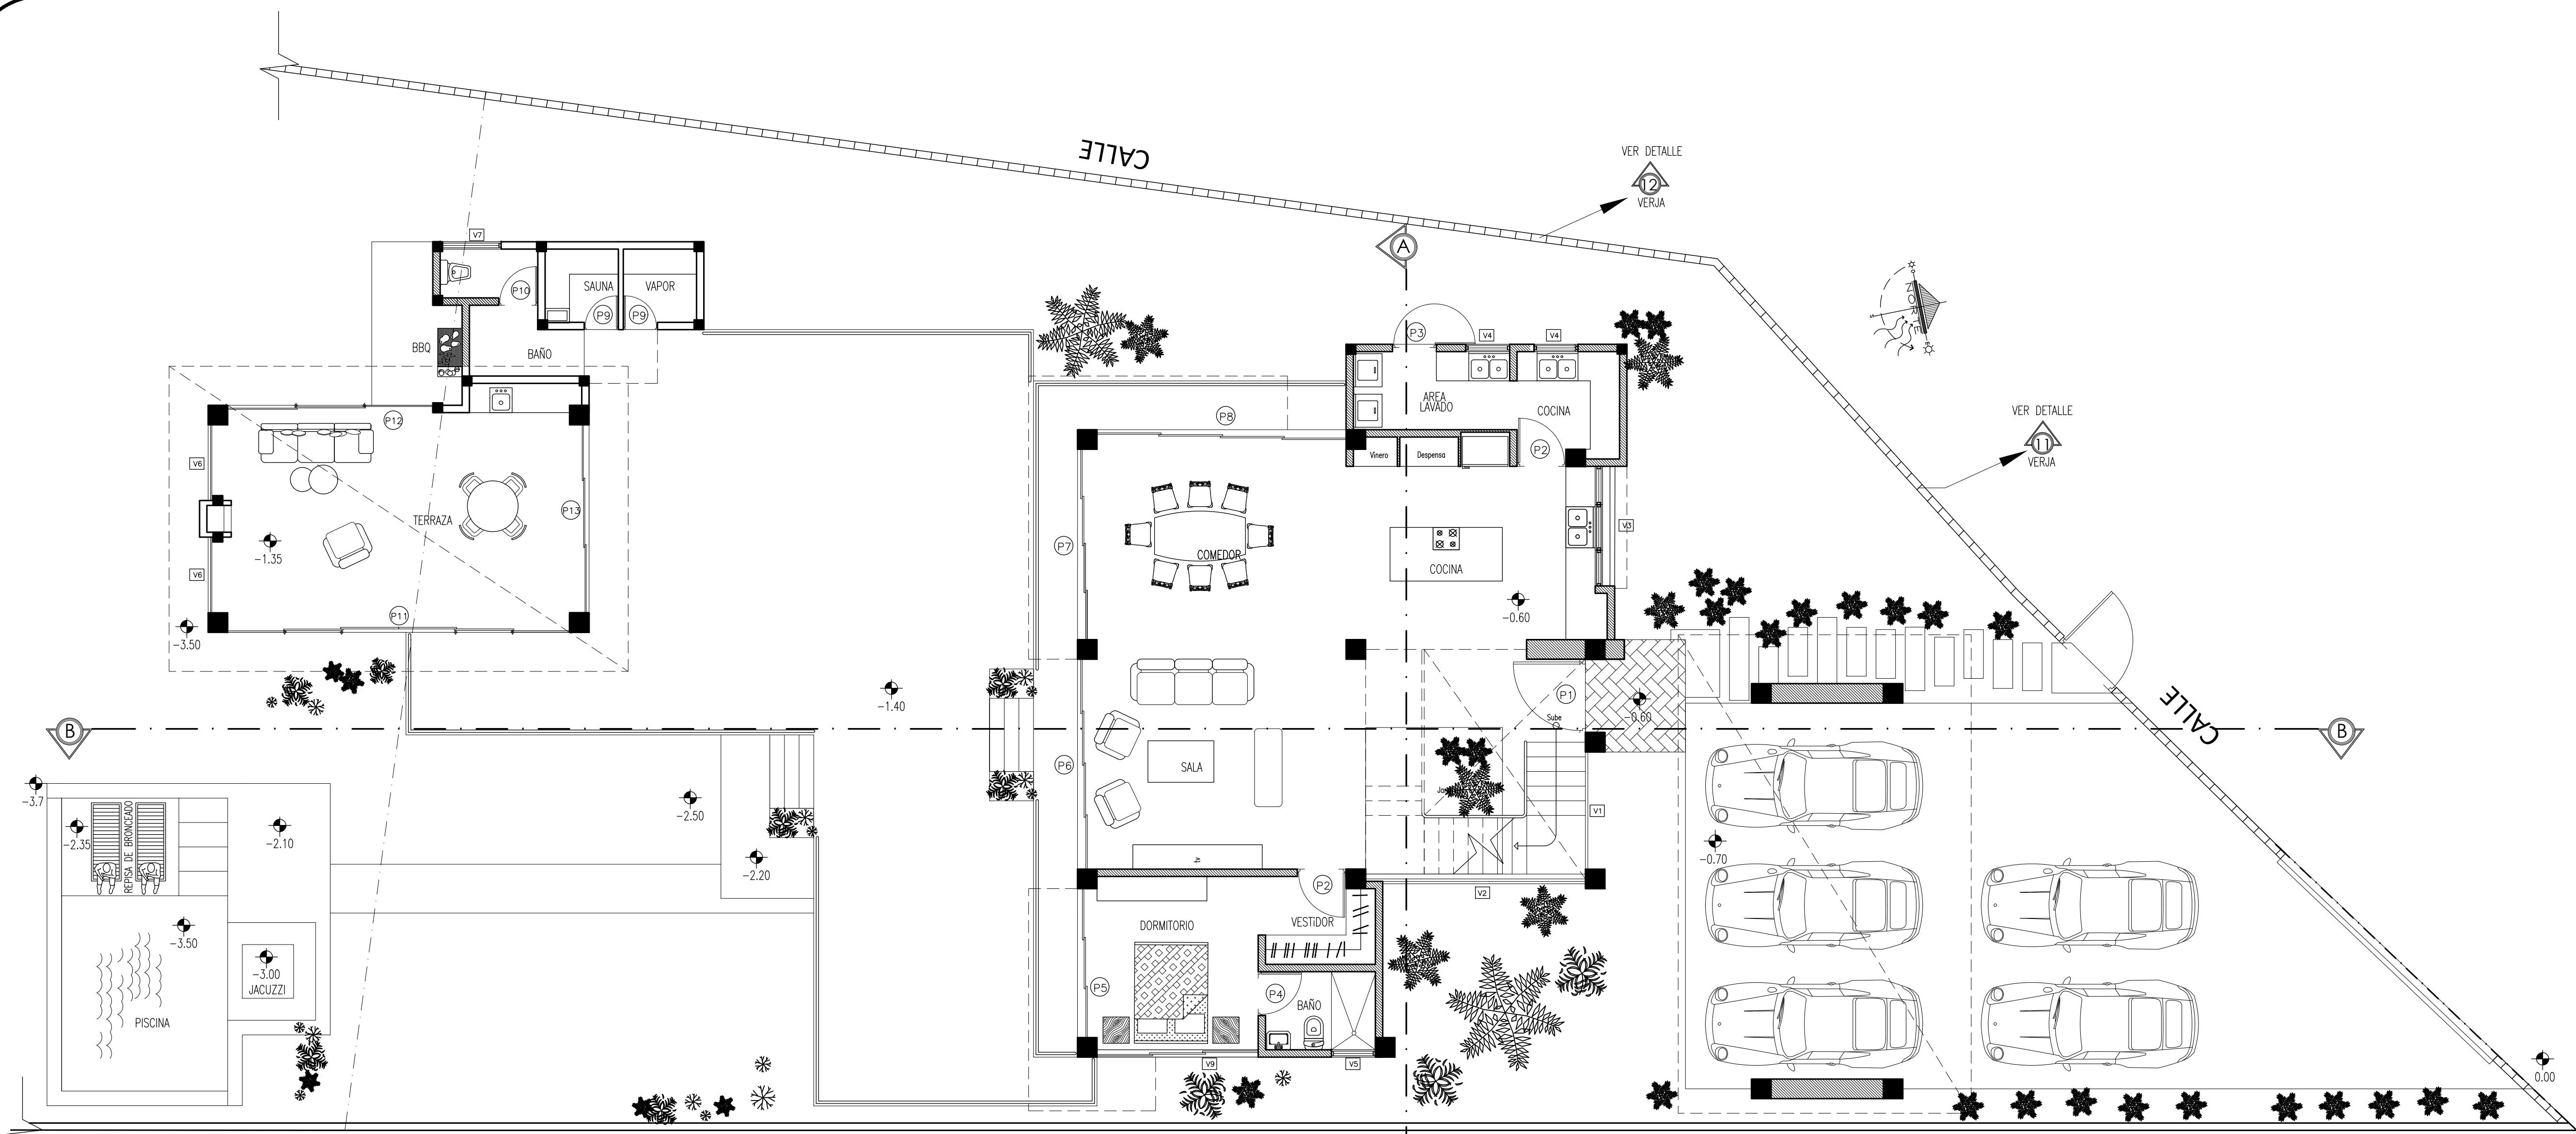

PLANTA ARQUITECTONICA
ESCALA: 1:75 1er. nivel 240.00 M²
AREA TOTAL CONSTRUCCION 389.25 METROS

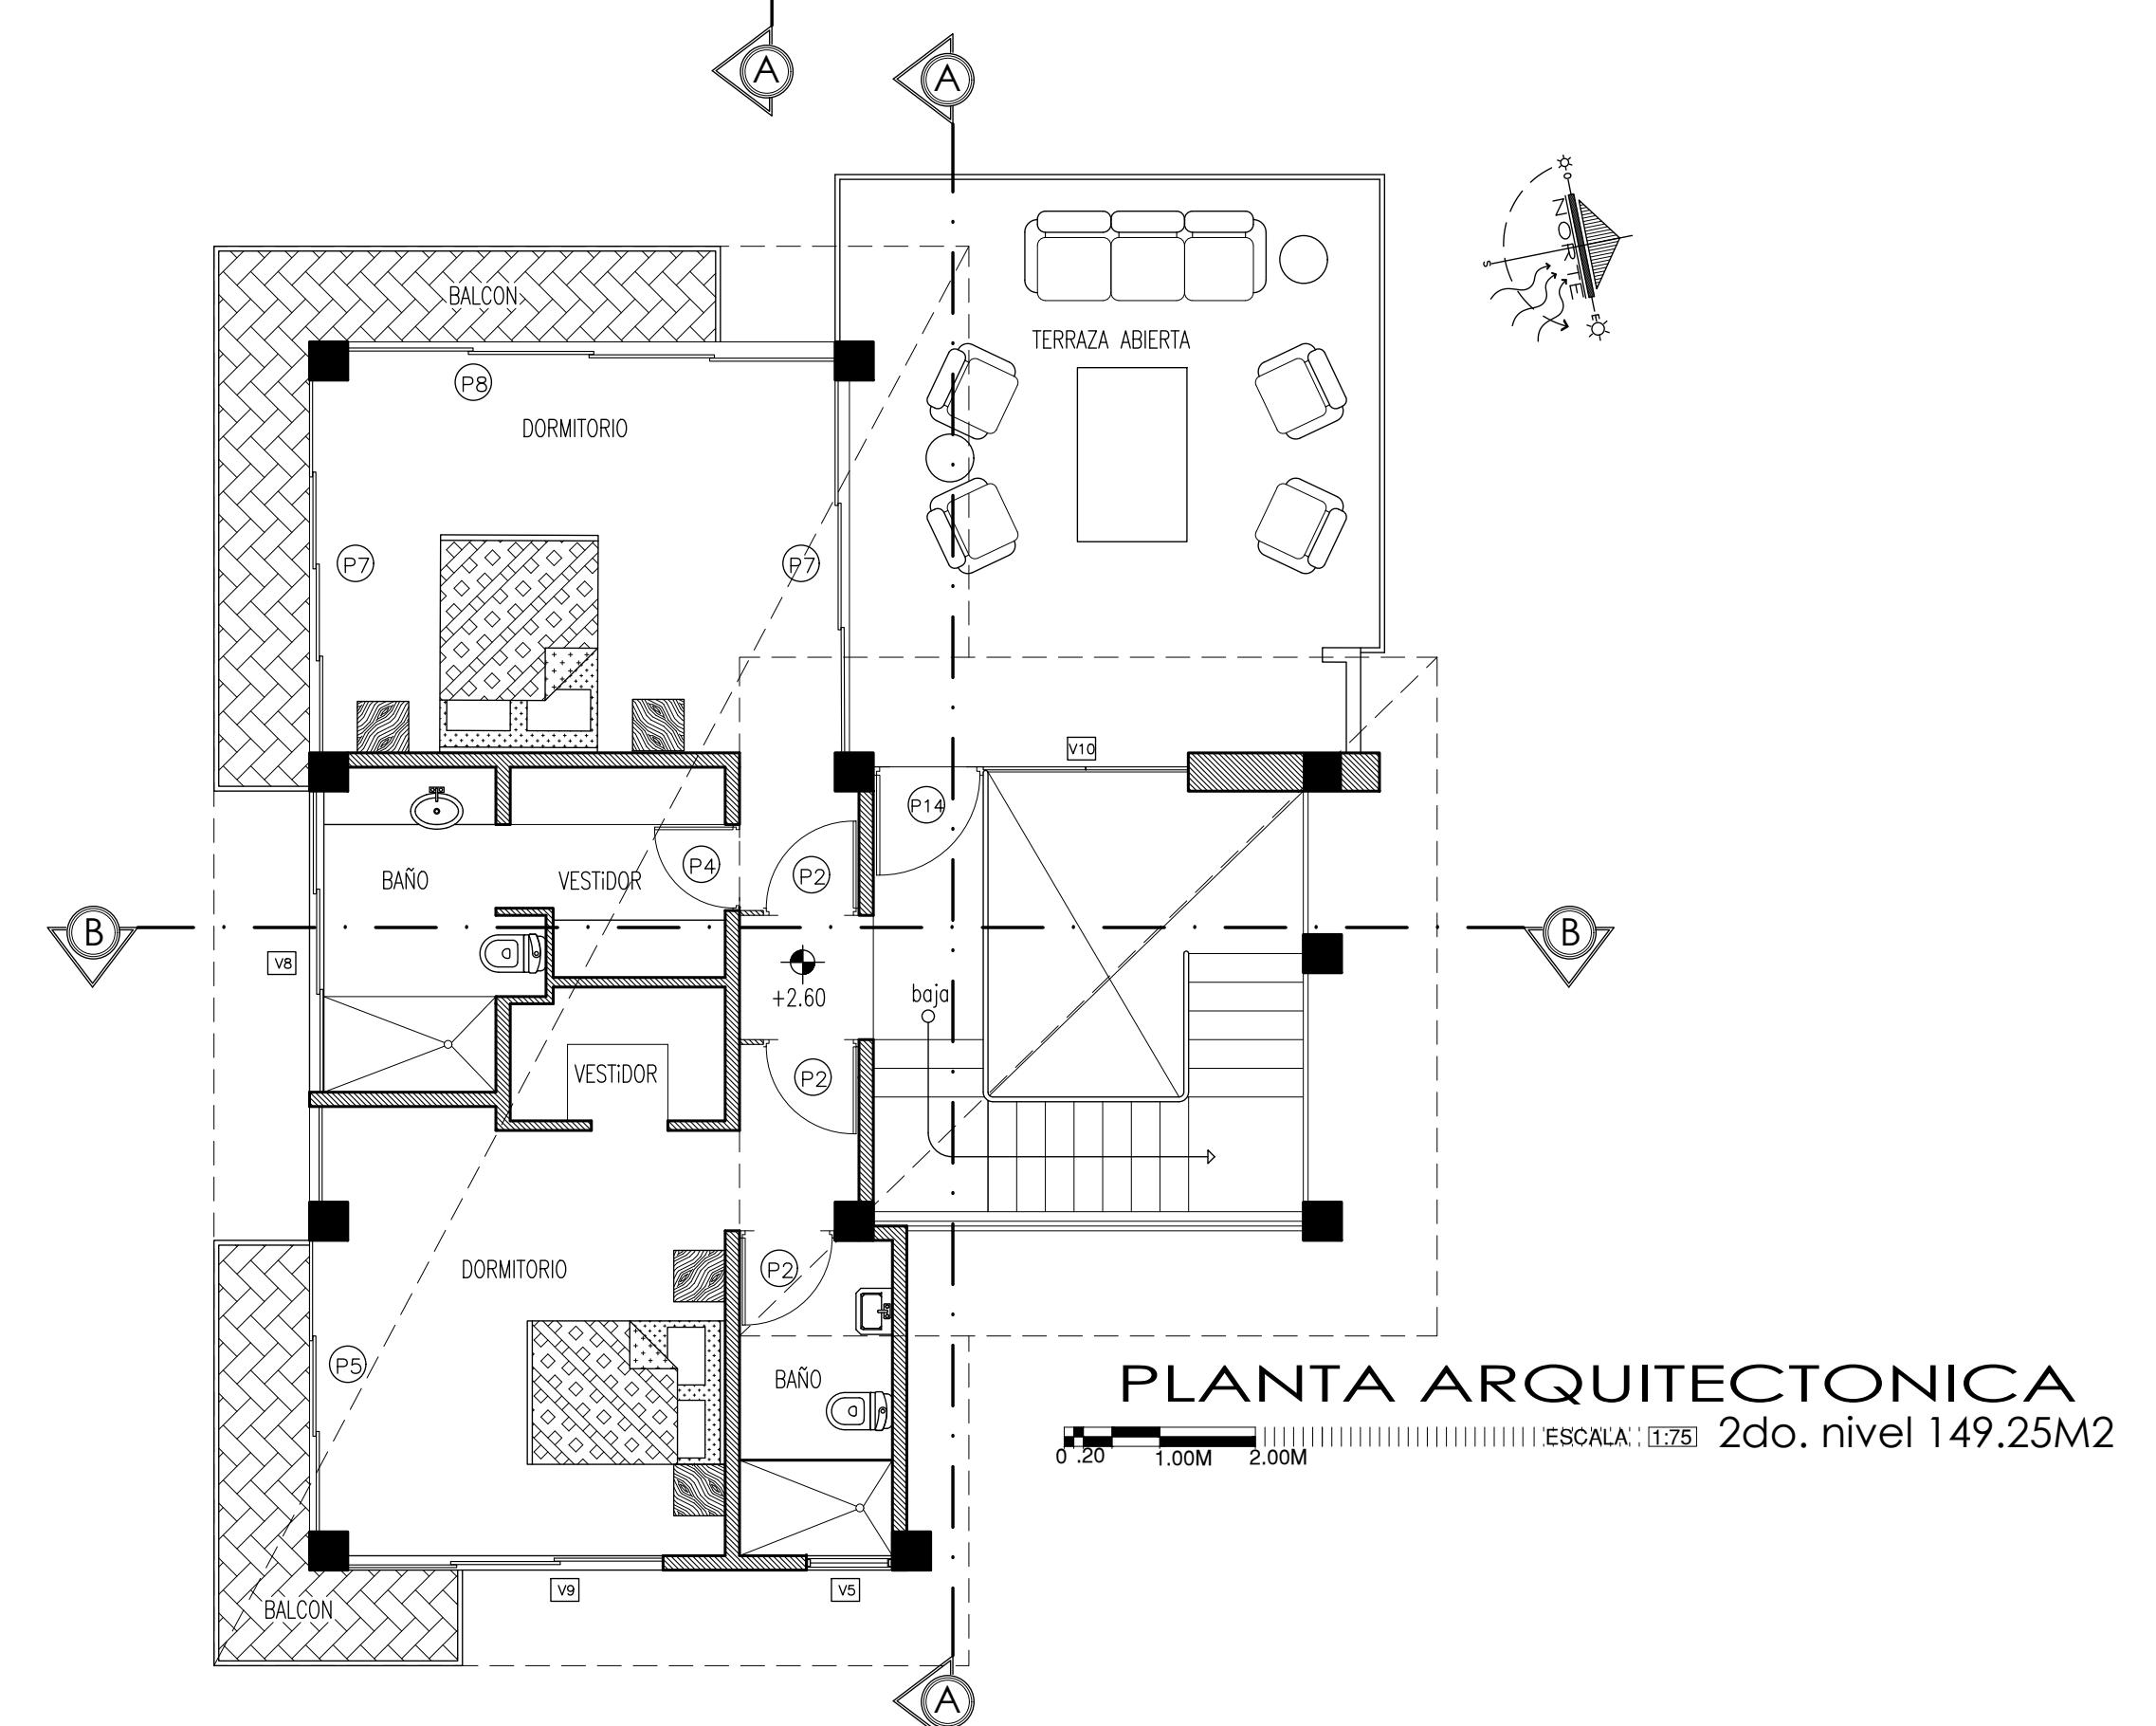

PLANTA ARQUITECTONICA
ESCALA: 1:75 2do. nivel 149.25M²

Este proyecto es propiedad única y exclusivamente del arquitecto EDDY J. LOPEZ C. el cual sede la ejecución con estos planos de un solo proyecto en un solo lugar específico ya previamente establecido, si usted es destinatario o no de este proyecto, debe abstenerse totalmente de copiar, reproducir, distribuir, ceder a un familiar o particular, robar conceptos del mismo. La violación a esta disposición sería procesada legalmente con todo el peso de la justicia Dominicana por violar la ley sobre derecho de autor.

NOTA: ESTAS TABLAS SON VALIDAS PARA LOS TRES NIVELES

TABLA DE VENTANAS					
VENTANA	ALTURA	ANCHO	ATURA NPT.	#HOJAS	CANTIDAD
V1	7.10	2.40	0.00	9	1 UD
V2	7.10	4.15	0.00	9	1 UD
V3	0.60	2.45	1.60	3	1 UD
V4	0.60	0.90	1.10	2	2 UD
V5	1.40	0.90	1.20	2	2 UD
V6	2.35	1.55	0.00	1	2 UD
V7	1.20	1.25	1.20	2	1 UD
V8	1.00	3.15	1.60	4	1 UD
V9	1.40	3.30	1.20	3	2 UD
V10	2.60	2.15	0.00	2	1 UD
					CRISTAL FIJO

TABLA DE PUERTAS				
PUERTA	ALTURA	ANCHO	No. PUERTA	DESCRIPCION
P1	2.80 MT.	1.50	1	MADERA ROBLE
P2	2.10 MT.	1.00	5	MADERA ROBLE
P3	2.10 MT.	0.90	1	POLIMETAL
P4	2.10 MT.	0.90	2	MADERA ROBLE
P5	2.60MT.	3.05	2	CRISTAL + ALUMINIO CORREDIZA(3HOJAS)
P6	2.60 MT.	4.30	1	CRISTAL + ALUMINIO CORREDIZA(4HOJAS)
P7	2.60 MT.	3.90	3	CRISTAL + ALUMINIO CORREDIZA(4HOJAS)
P8	2.60 MT.	5.10	2	CRISTAL + ALUMINIO CORREDIZA(4HOJAS)
P9	2.10 MT.	0.70	2	MADERA ROBLE
P10	2.10 MT.	0.80	1	MADERA ROBLE
P11	2.35 MT.	4.20	1	CRISTAL + ALUMINIO CORREDIZA(6HOJAS)
P12	2.35 MT.	4.20	1	CRISTAL + ALUMINIO CORREDIZA(6HOJAS)
P13	2.35 MT.	4.10	1	CRISTAL + ALUMINIO CORREDIZA(3HOJAS)
P13	2.60 MT.	1.15	1	CRISTAL + ALUMINIO CORREDIZA(1HOJAS)

ESPECIFICACIONES

PISOS
EN PROYECTO GRAL. PORCELANATO 0.50X0.50MT CON DERRETIDO SEPARACION 3.0 MM. EN TODO EL PROYECTO MENOS EN MARQUESINA Y TERRAZA, LAS CUALES SERAN CON CERAMICA ANTIRRESPALDIZADAS.

ZOCALOS
PORCELANATO 0.50X0.10MT CON DERRETIDO
BANOS, SEGUN DETALLES



PAREDES
PAÑete LISO EN TODA LA CONSTRUCCION Y CERAMICA
EN BAÑOS, SEGUN DETALLES

PINTURA
EL PROYECTO SERA PINTADO EN SU EXTERIOR Y EN SU INTERIOR
CON DOS MANOS DE PINTURA ACRILICA .

TECHOS
LOS TECHOS SERAN EN ALUZINC CON AISLANTE Y LA ESCALERA
HA CON UN FINO DE 0.03 MM. + SELLADOR DE TECHO.


GENERAL
TODA LA CONSTRUCCION DEBE SER
EJECUTADA DE ACUERDO CON LAS
ESPECIFICACIONES DADA EN LOS PLANOS

Villa Beato Reyes	LOCALIZACION: GUAGUI, LA VEGA
PROPIETARIOS:	
JOSE LUIS BEATO PEÑA CED. 402-2763926-3	FIRMA
JOSELYN ANTONELIA REYES A. CED. 402-2737538-9	FIRMA
DISEÑO ARQUITECTONICO: SHERYL LOPEZ R. CODIA: 46298	
DISEÑO SANITARIO: ING. FRANK FELIZ LOPEZ CODIA: 19796	
DISEÑO ESTRUCTURAL: HIPOLITO MORONIA LLONG CODIA: 4166	
DISEÑO ELECTRICO: HIPOLITO MORONIA LLONG CODIA: 4166	
ARQ. EDDY LOPEZ C. 809-399 8344	
DIBUJO : 0 1 8 U 0 EL ARQUITECTURA AVENIDA AMERICANA #4 LA VEGA 809-573-7056 809-399-8344	ESCALA : INDICADA
FECHA: 1 - 9 - 2021	HOJA # 2/23

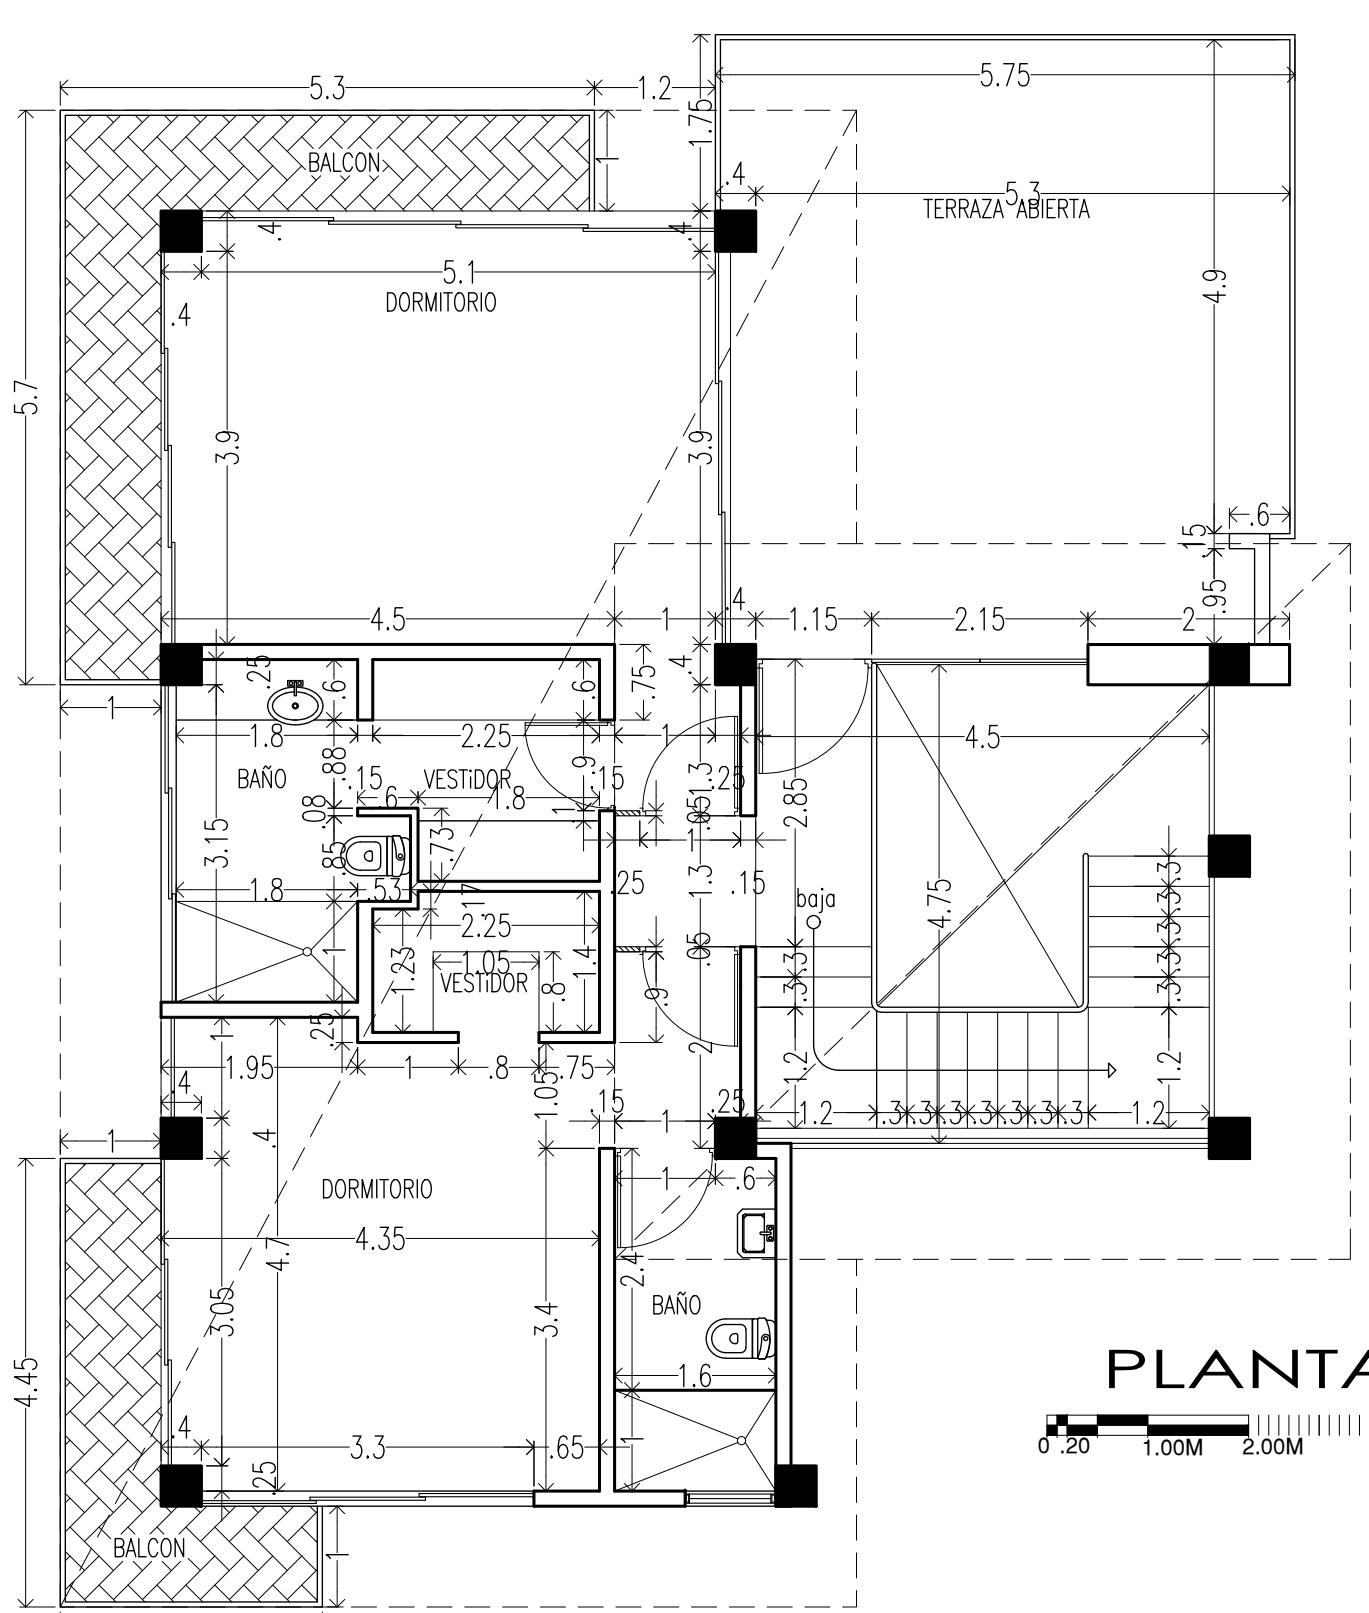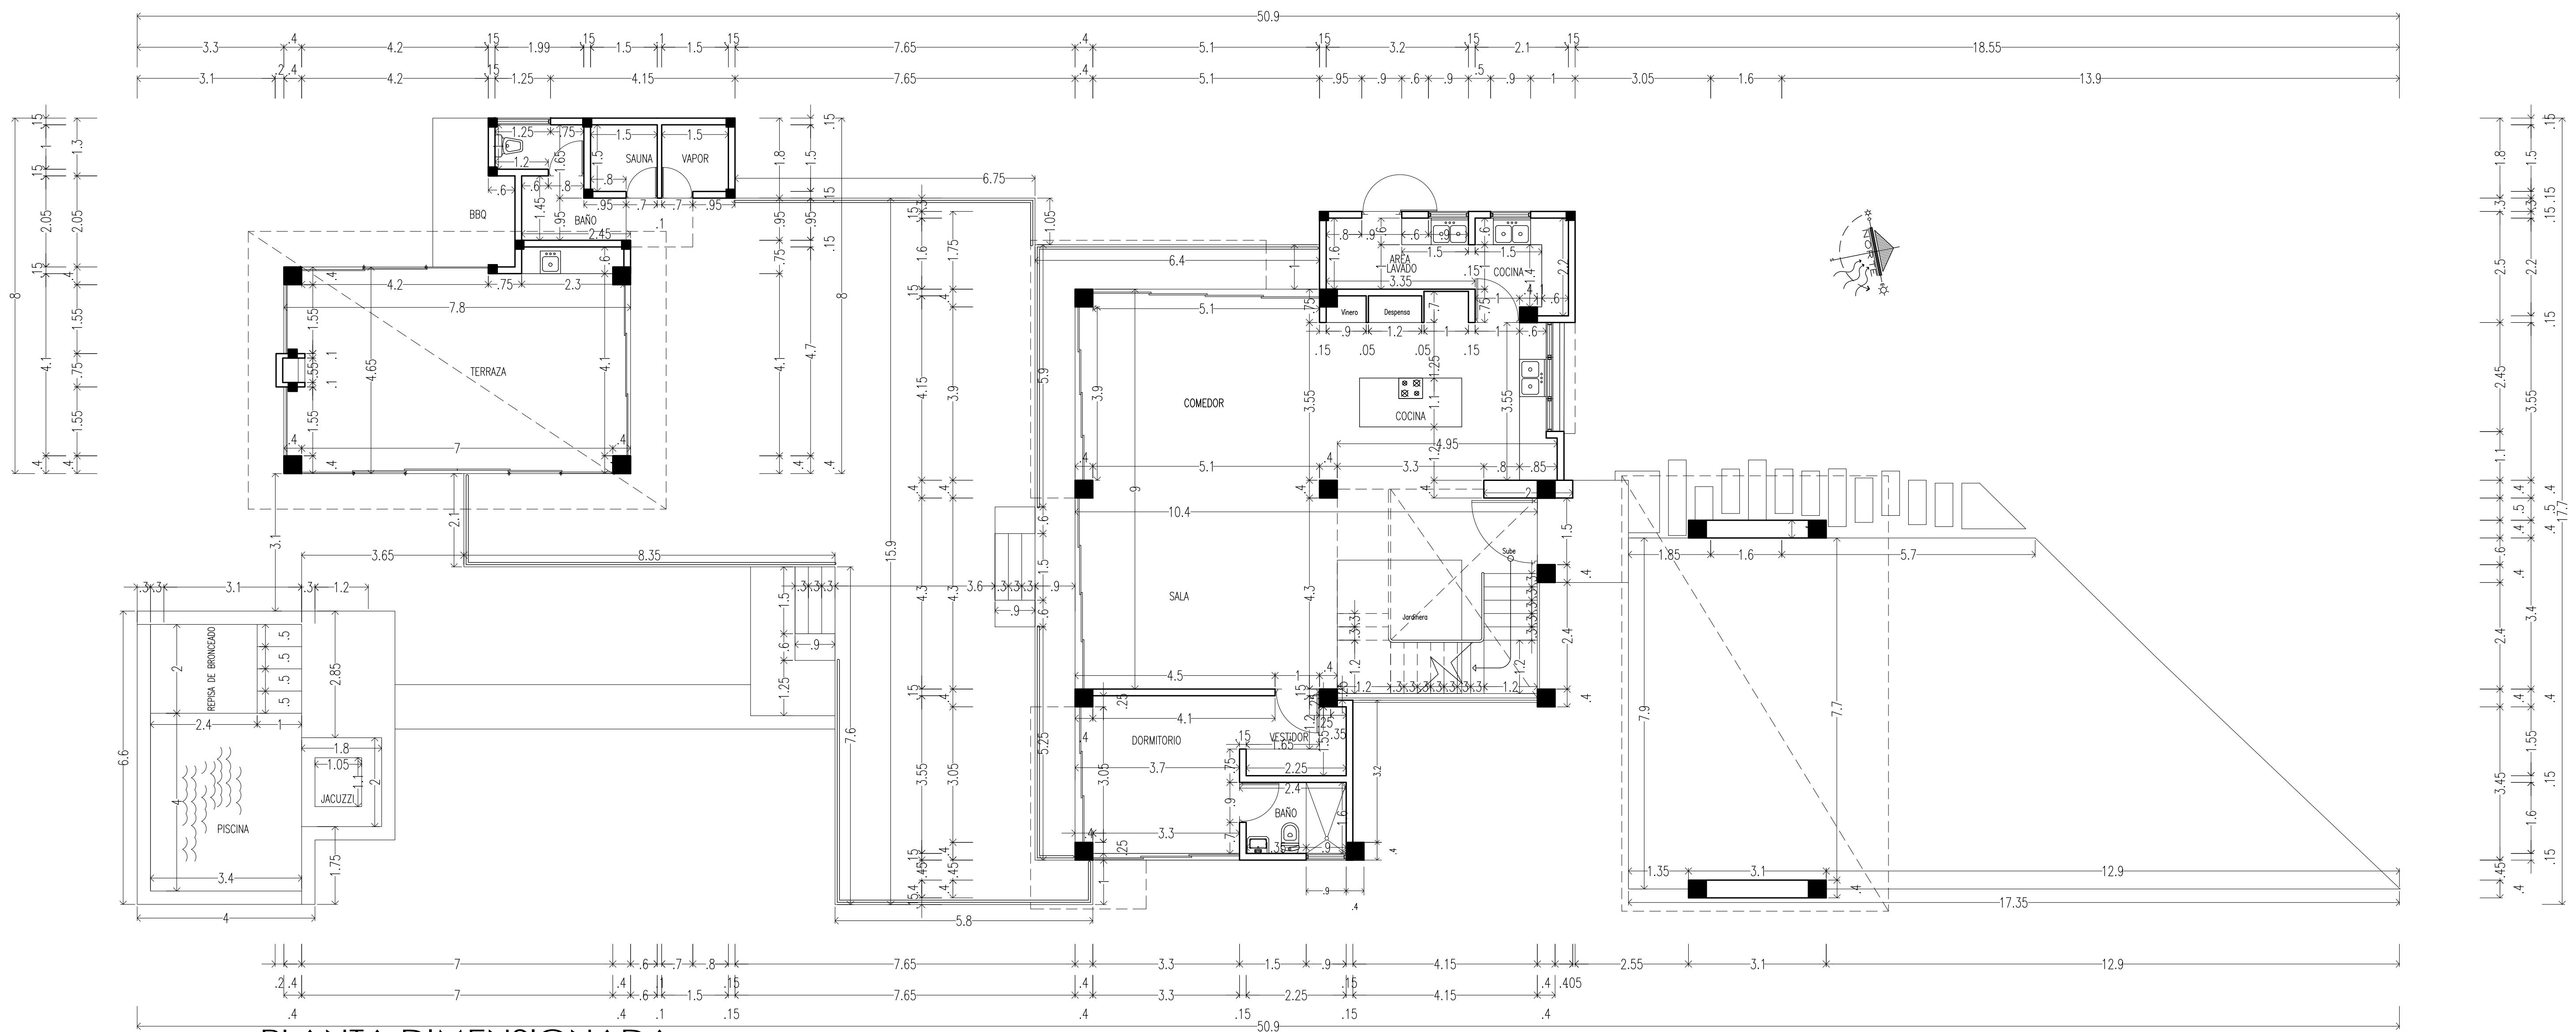


Este proyecto es propiedad única y exclusivamente del arquitecto EDDY J. LOPEZ C. el cual sede la ejecución con estos planos de un solo proyecto en un solo lugar específico ya previamente establecido, si usted es destinatario o no de este proyecto, debe de abstenerse totalmente de copiar, reproducir, distribuir, ceder a un familiar o particular, robar conceptos del mismo. La violación a esta disposición sería procesada legalmente con todo el peso de la justicia Dominicana por violar la ley sobre derecho de autor.

Villa Beato Reyes	
LOCALIZACION: GUAGUI, LA VEGA	
PROPIETARIOS:	
JOSE LUIS BEATO PEÑA CED. 402-2763926-3	FIRMA
JOSELYN ANTONELIA REYES A. CED. 402-2737538-9	FIRMA
DISEÑO ARQUITECTONICO: SHERYL LOPEZ R. CODA: 46298	
DISEÑO SANITARIO: ING. FRANK FELIZ LOPEZ CODA: 19796	
DISEÑO ESTRUCTURAL: HIPOLITO MORONITA LILONG CODA: 4166	
DISEÑO ELECTRICO: HIPOLITO MORONITA LILONG CODA: 4166	
RESPONSABLE DEL PROYECTO: ARQUITECTO: EDDY J. LOPEZ CODA: 13.638	
DIBUJO : DIBUJO 0 EL ARQUITECTURA AVENIDA AMERICA #4 LA VEGA 809-575-7056 809-599-8344	ESCALA
FECHA: 1 - 9 - 2021	INDICADA
HOJA # 3/23	

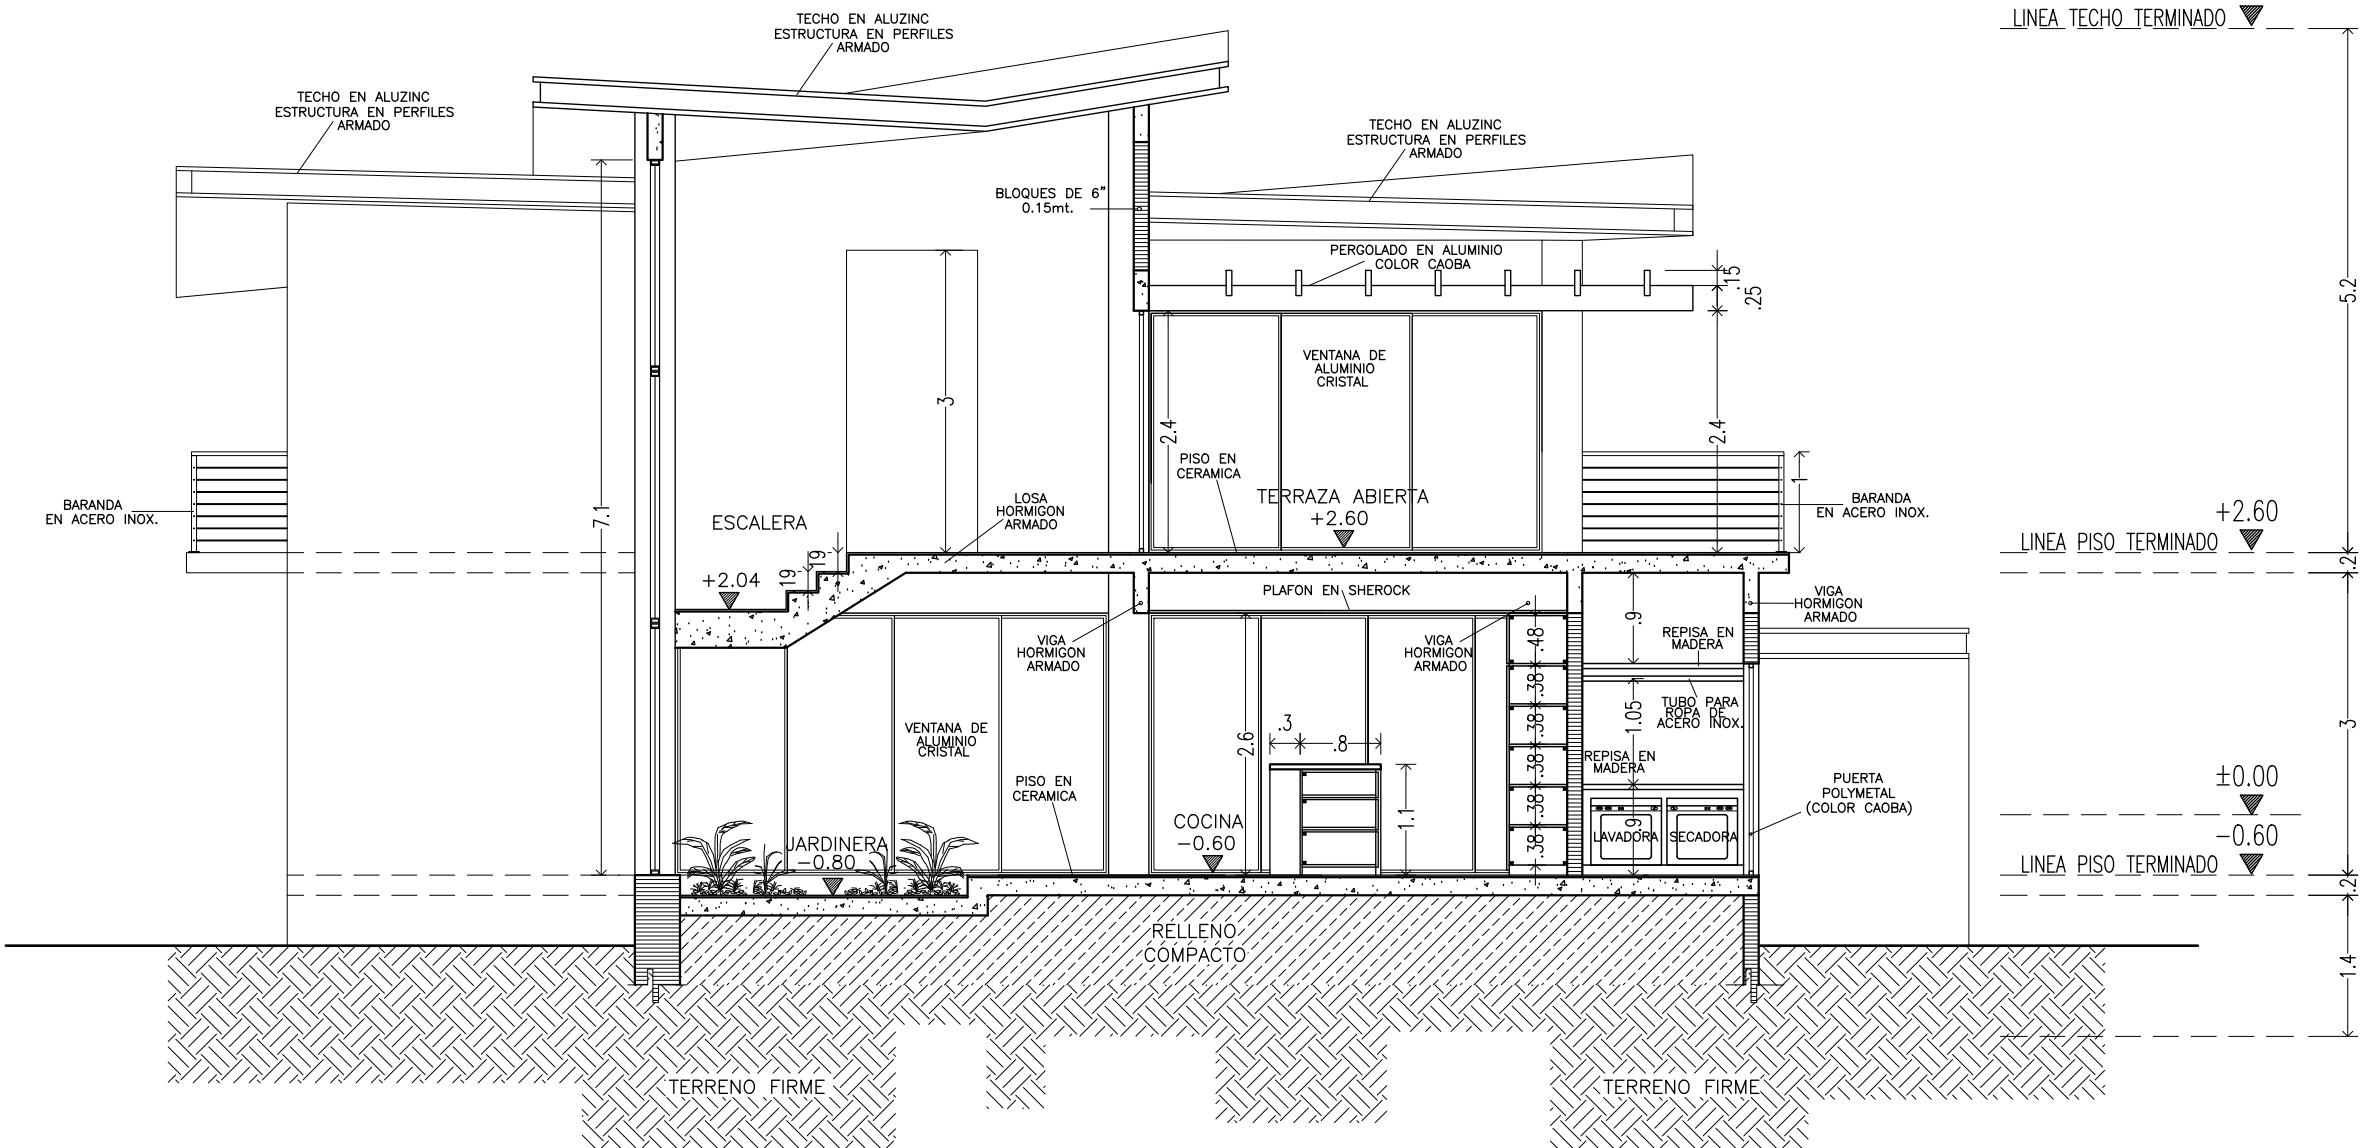


SECCION A-A

0.20 1.00M 2.00M ESCALA: 1:75

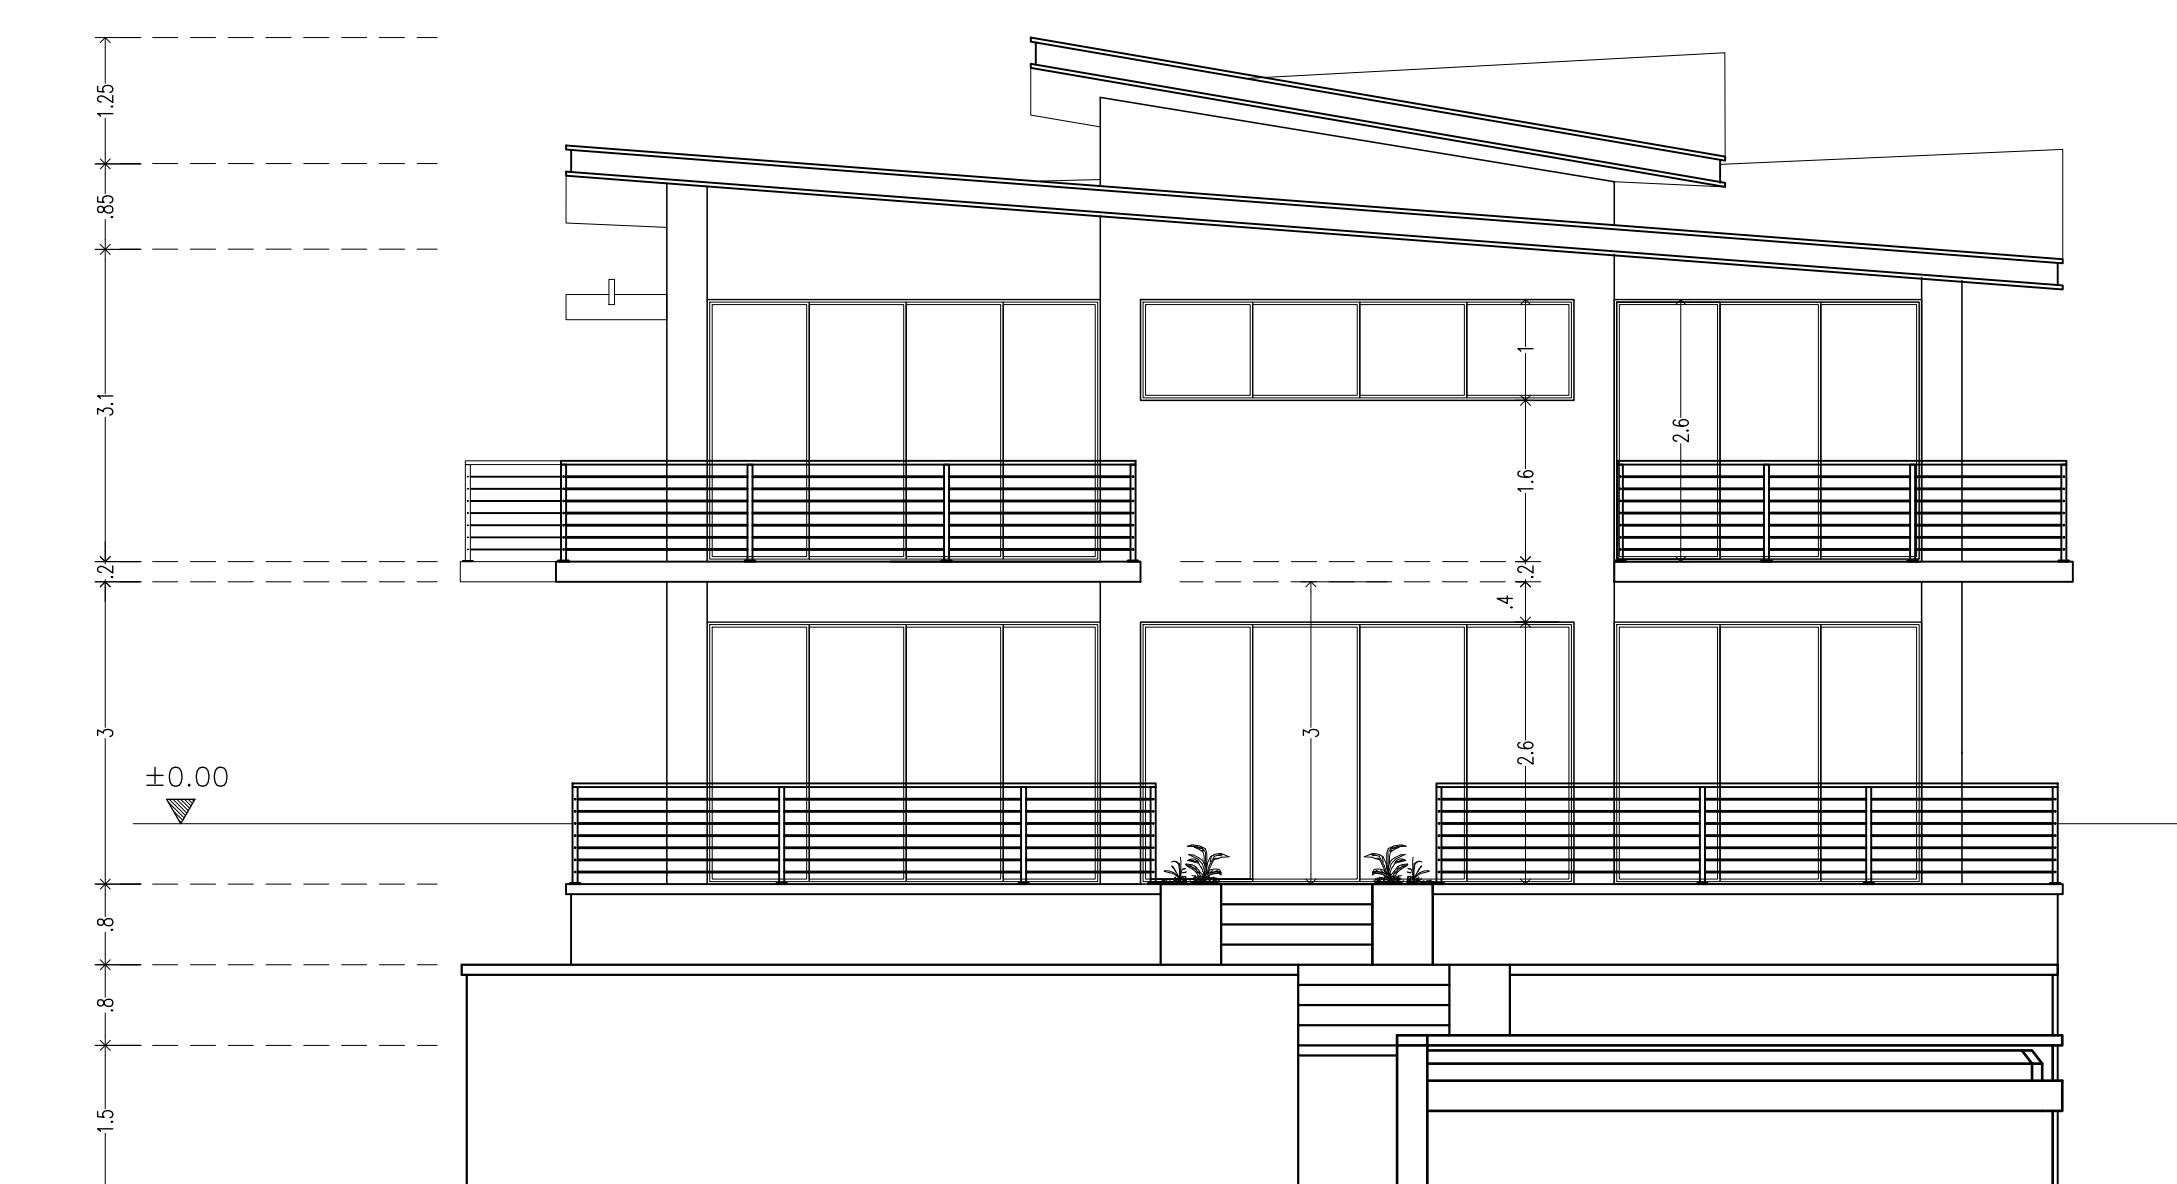


ELEVACION POSTERIOR

0.20 1.00M 2.00M ESCALA: 1:75

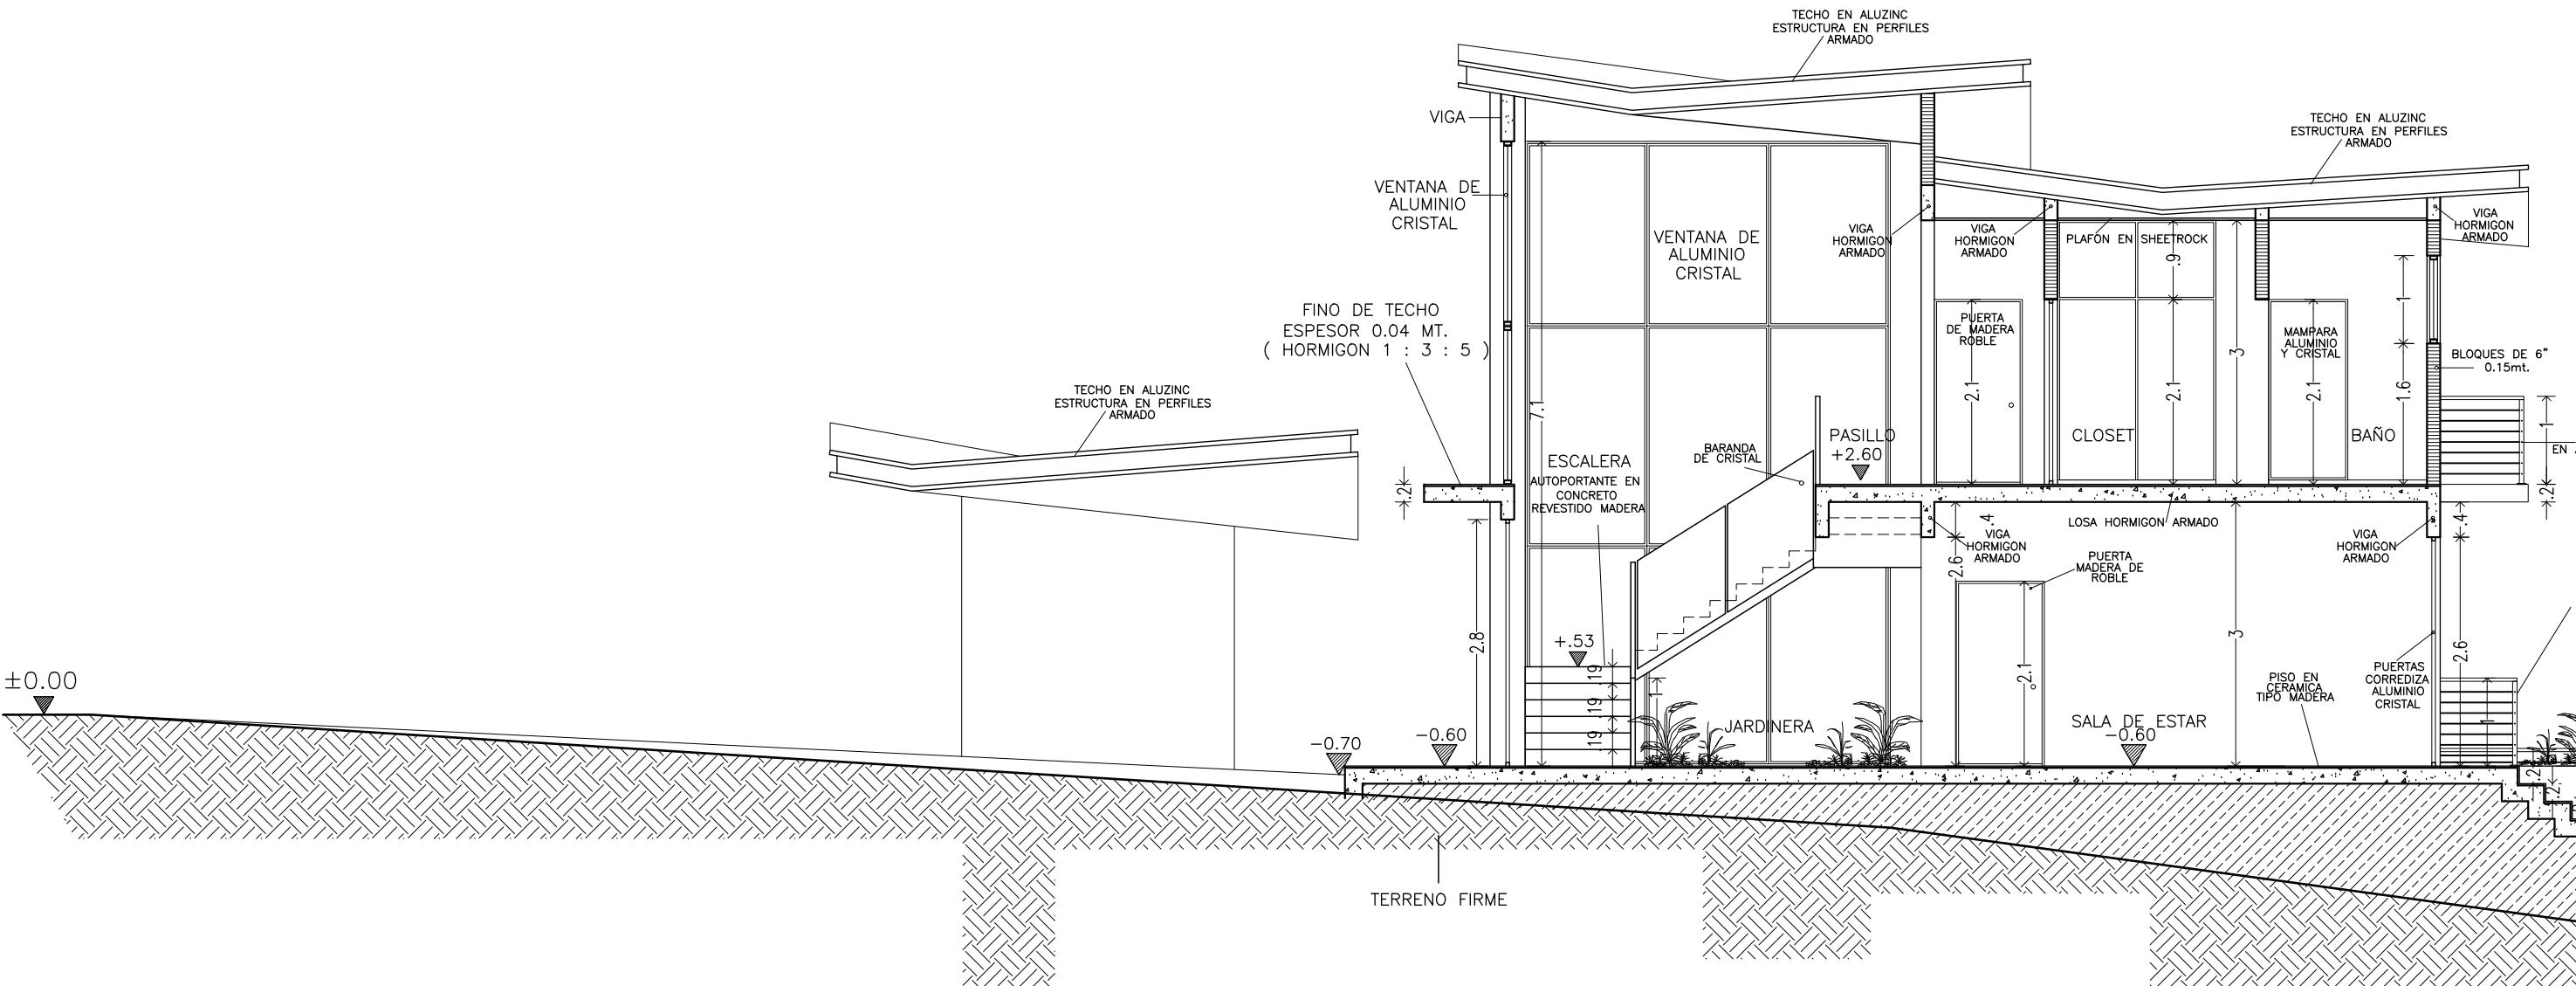

SECCION B-B

0.20 1.00M 2.00M ESCALA: 1:75

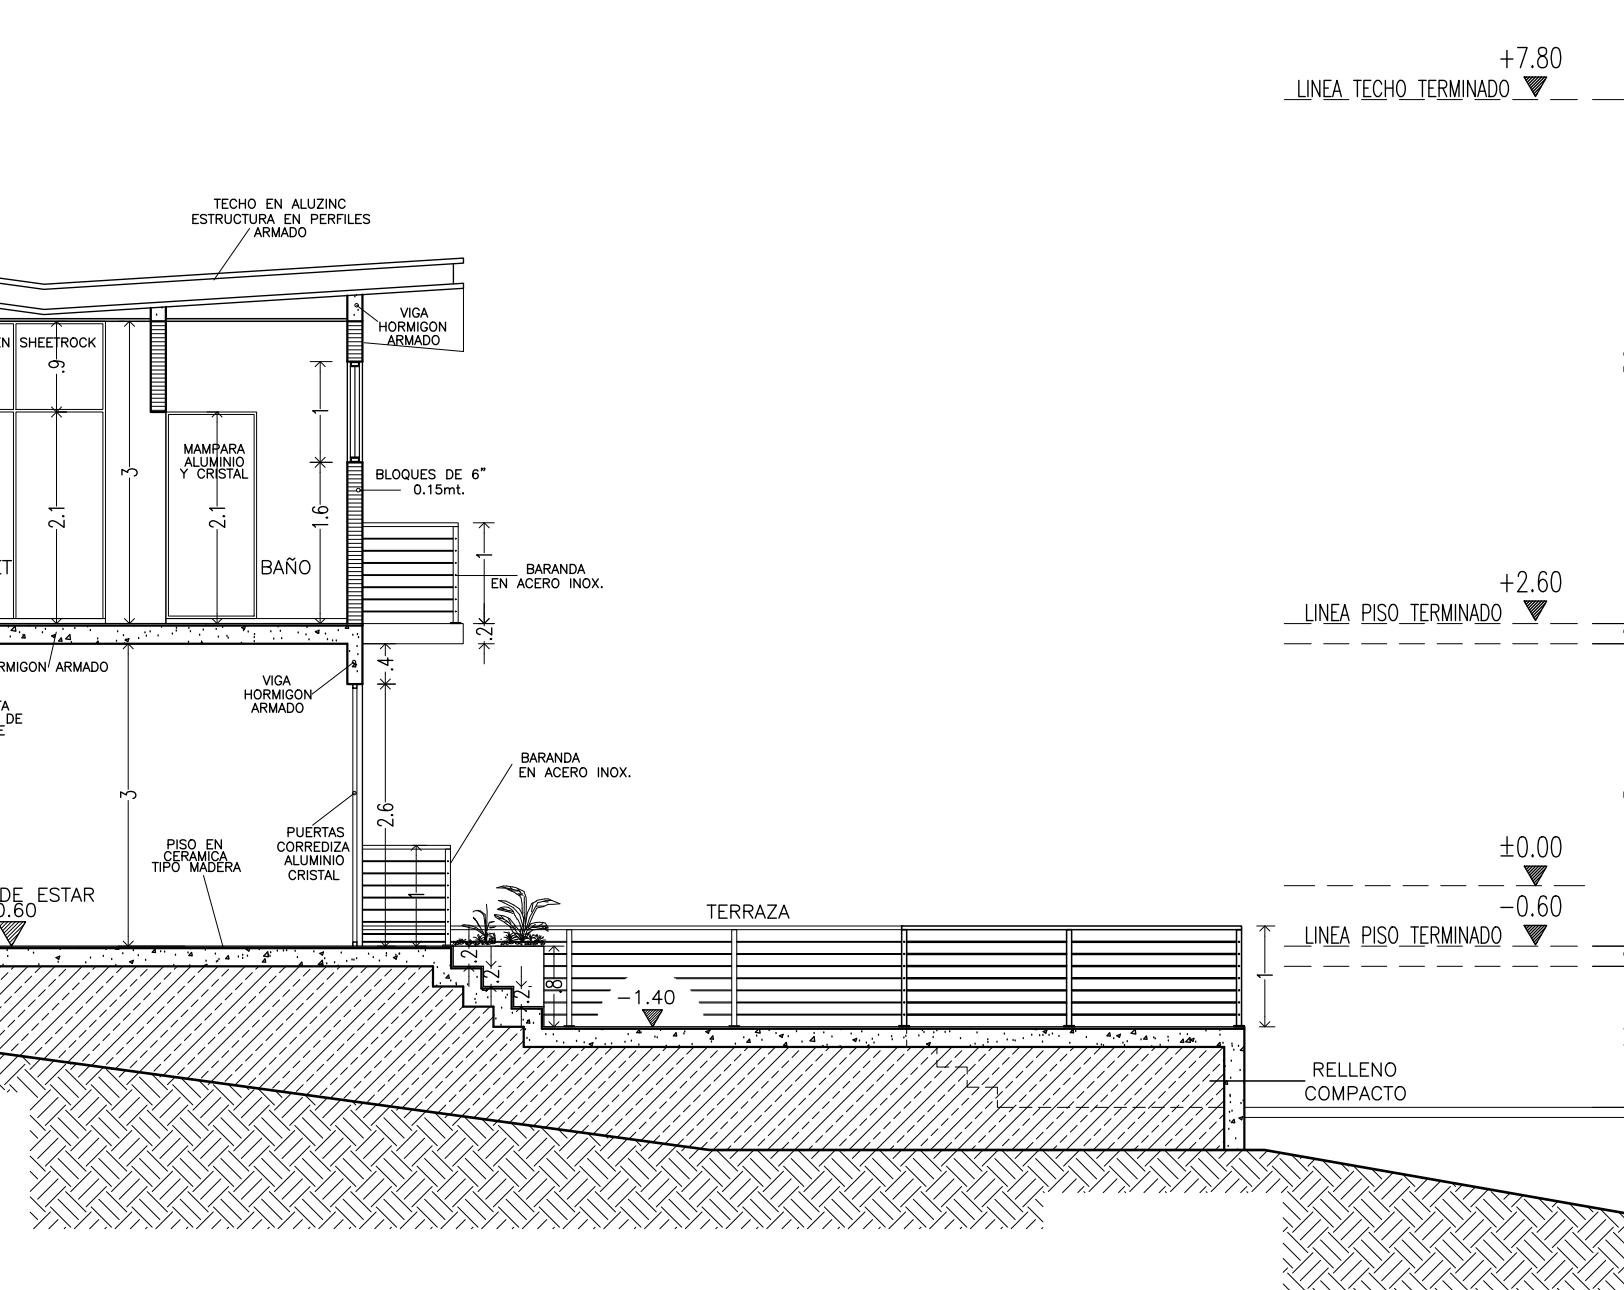


ELEVACION FRONTAL
(TERRAZA)

0.20 1.00M 2.00M ESCALA: 1:75


ELEVACION POSTERIOR
(TERRAZA)

0.20 1.00M 2.00M ESCALA: 1:75

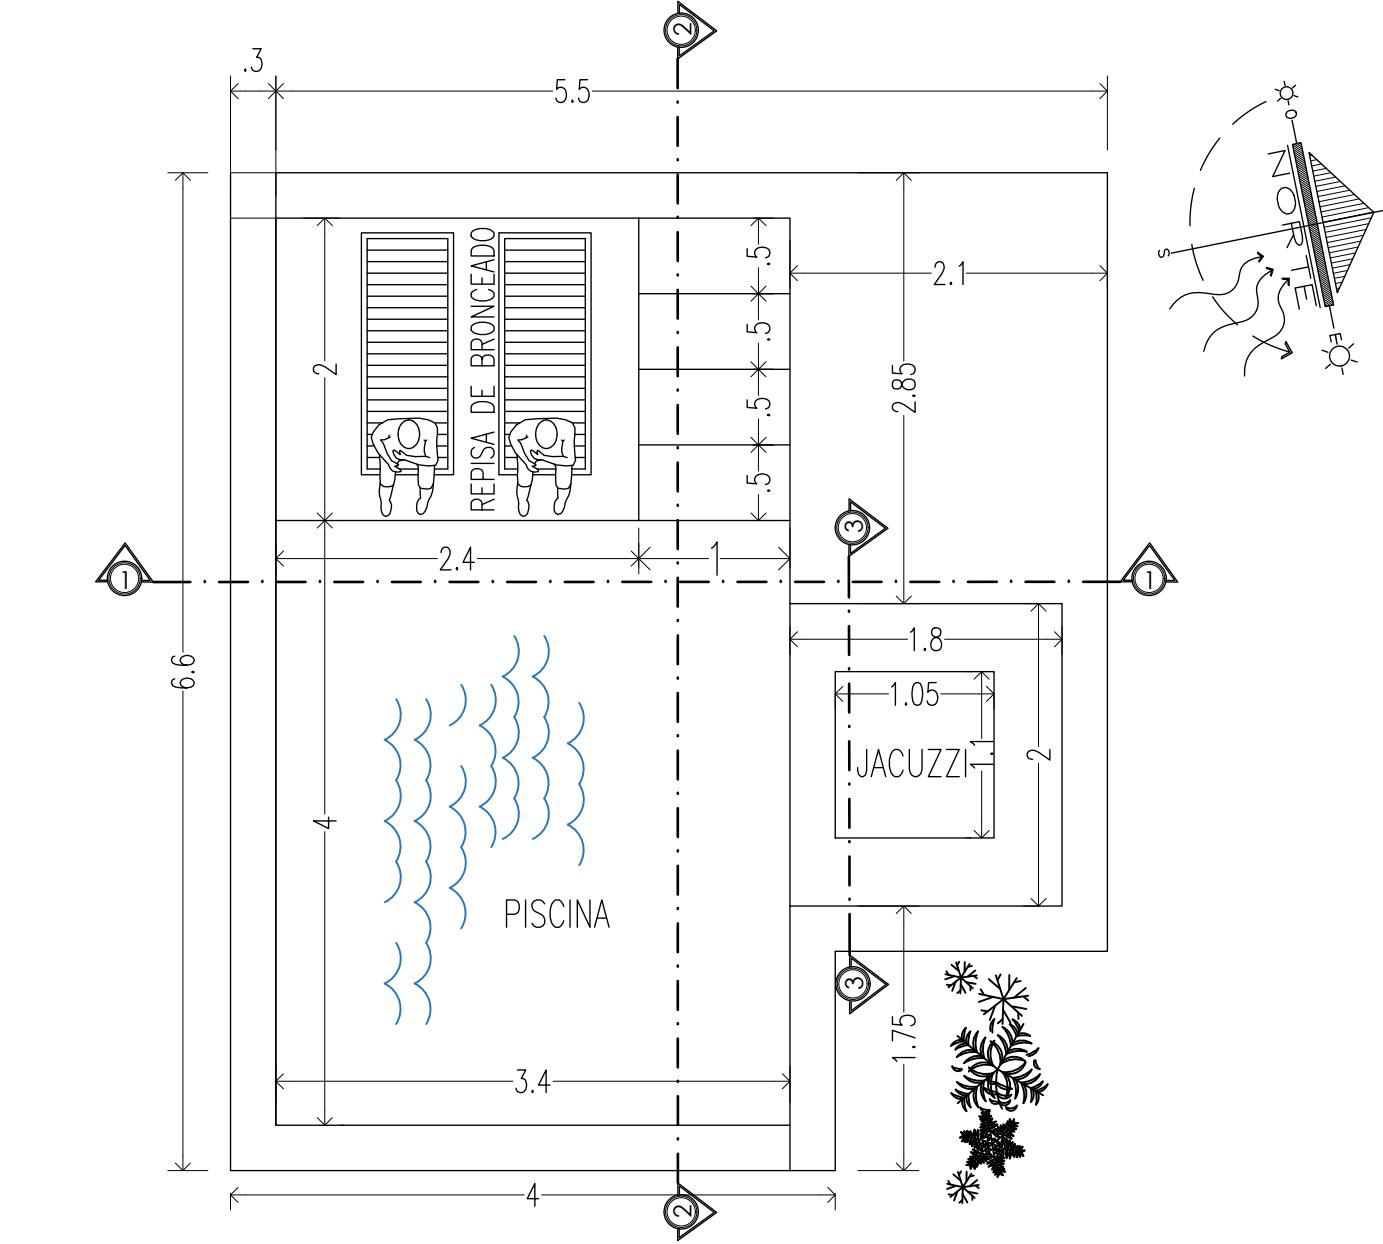


PLANTA DE PISCINA

0.20 1.00M 2.00M ESCALA: 1:50

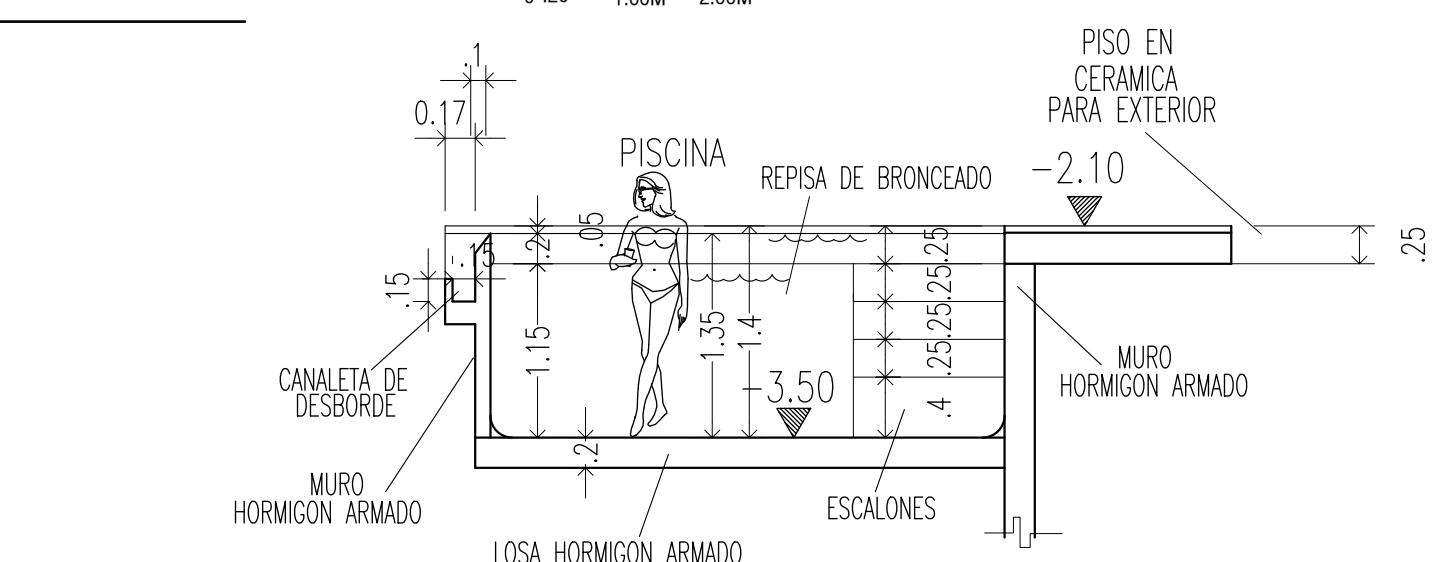


SECCION DE PISCINA

0.20 1.00M 2.00M ESCALA: 1:50

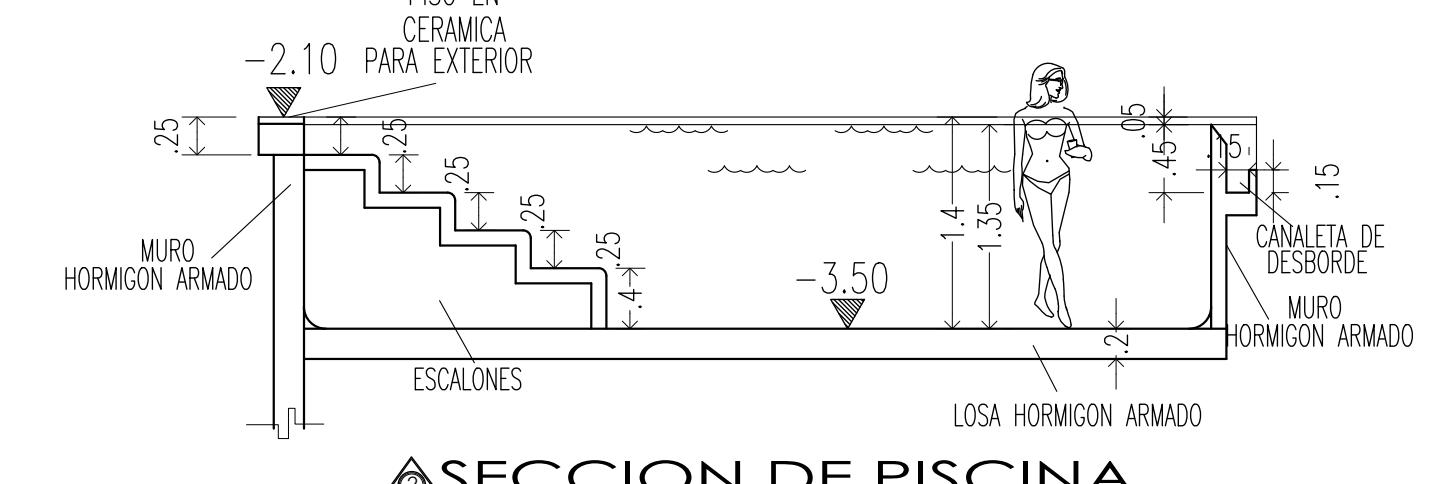

SECCION DE PISCINA

0.20 1.00M 2.00M ESCALA: 1:50

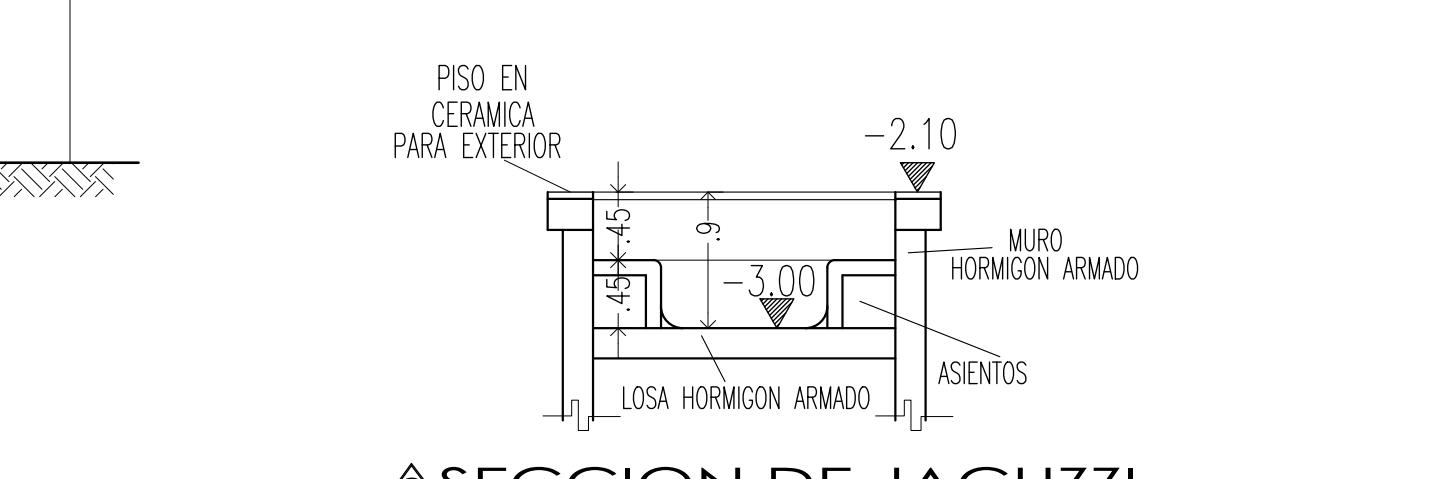

SECCION DE JACUZZI

0.20 1.00M 2.00M ESCALA: 1:50



ARQ. EDDY LOPEZ C.
809-399 8344

Villa Beato Reyes

LOCALIZACION: GUAIGU, LA VEGA

PROPIETARIOS:

JOSE LUIS BEATO PEÑA
CED. 402-2763926-3 FIRMA

JOSELYN ANTONELIA REYES A.
CED. 402-2737538-9 FIRMA

DISEÑO ARQUITECTONICO: SHERYL LOPEZ R. CODA: 46298


DISEÑO SANITARIO: INC. FRANK FELIZ LOPEZ CODA: 19796

DISEÑO ESTRUCTURAL: HIPOLITO MORONITA LLONG CODA: 4166


DISEÑO ELECTRICO: HIPOLITO MORONITA LLONG CODA: 4166

DIBUJO : D 1 B U 0
AVENIDA IMBERT #4 LA VEGA
809-573-7056 809-399-8344


ESCALA :
INDICADA

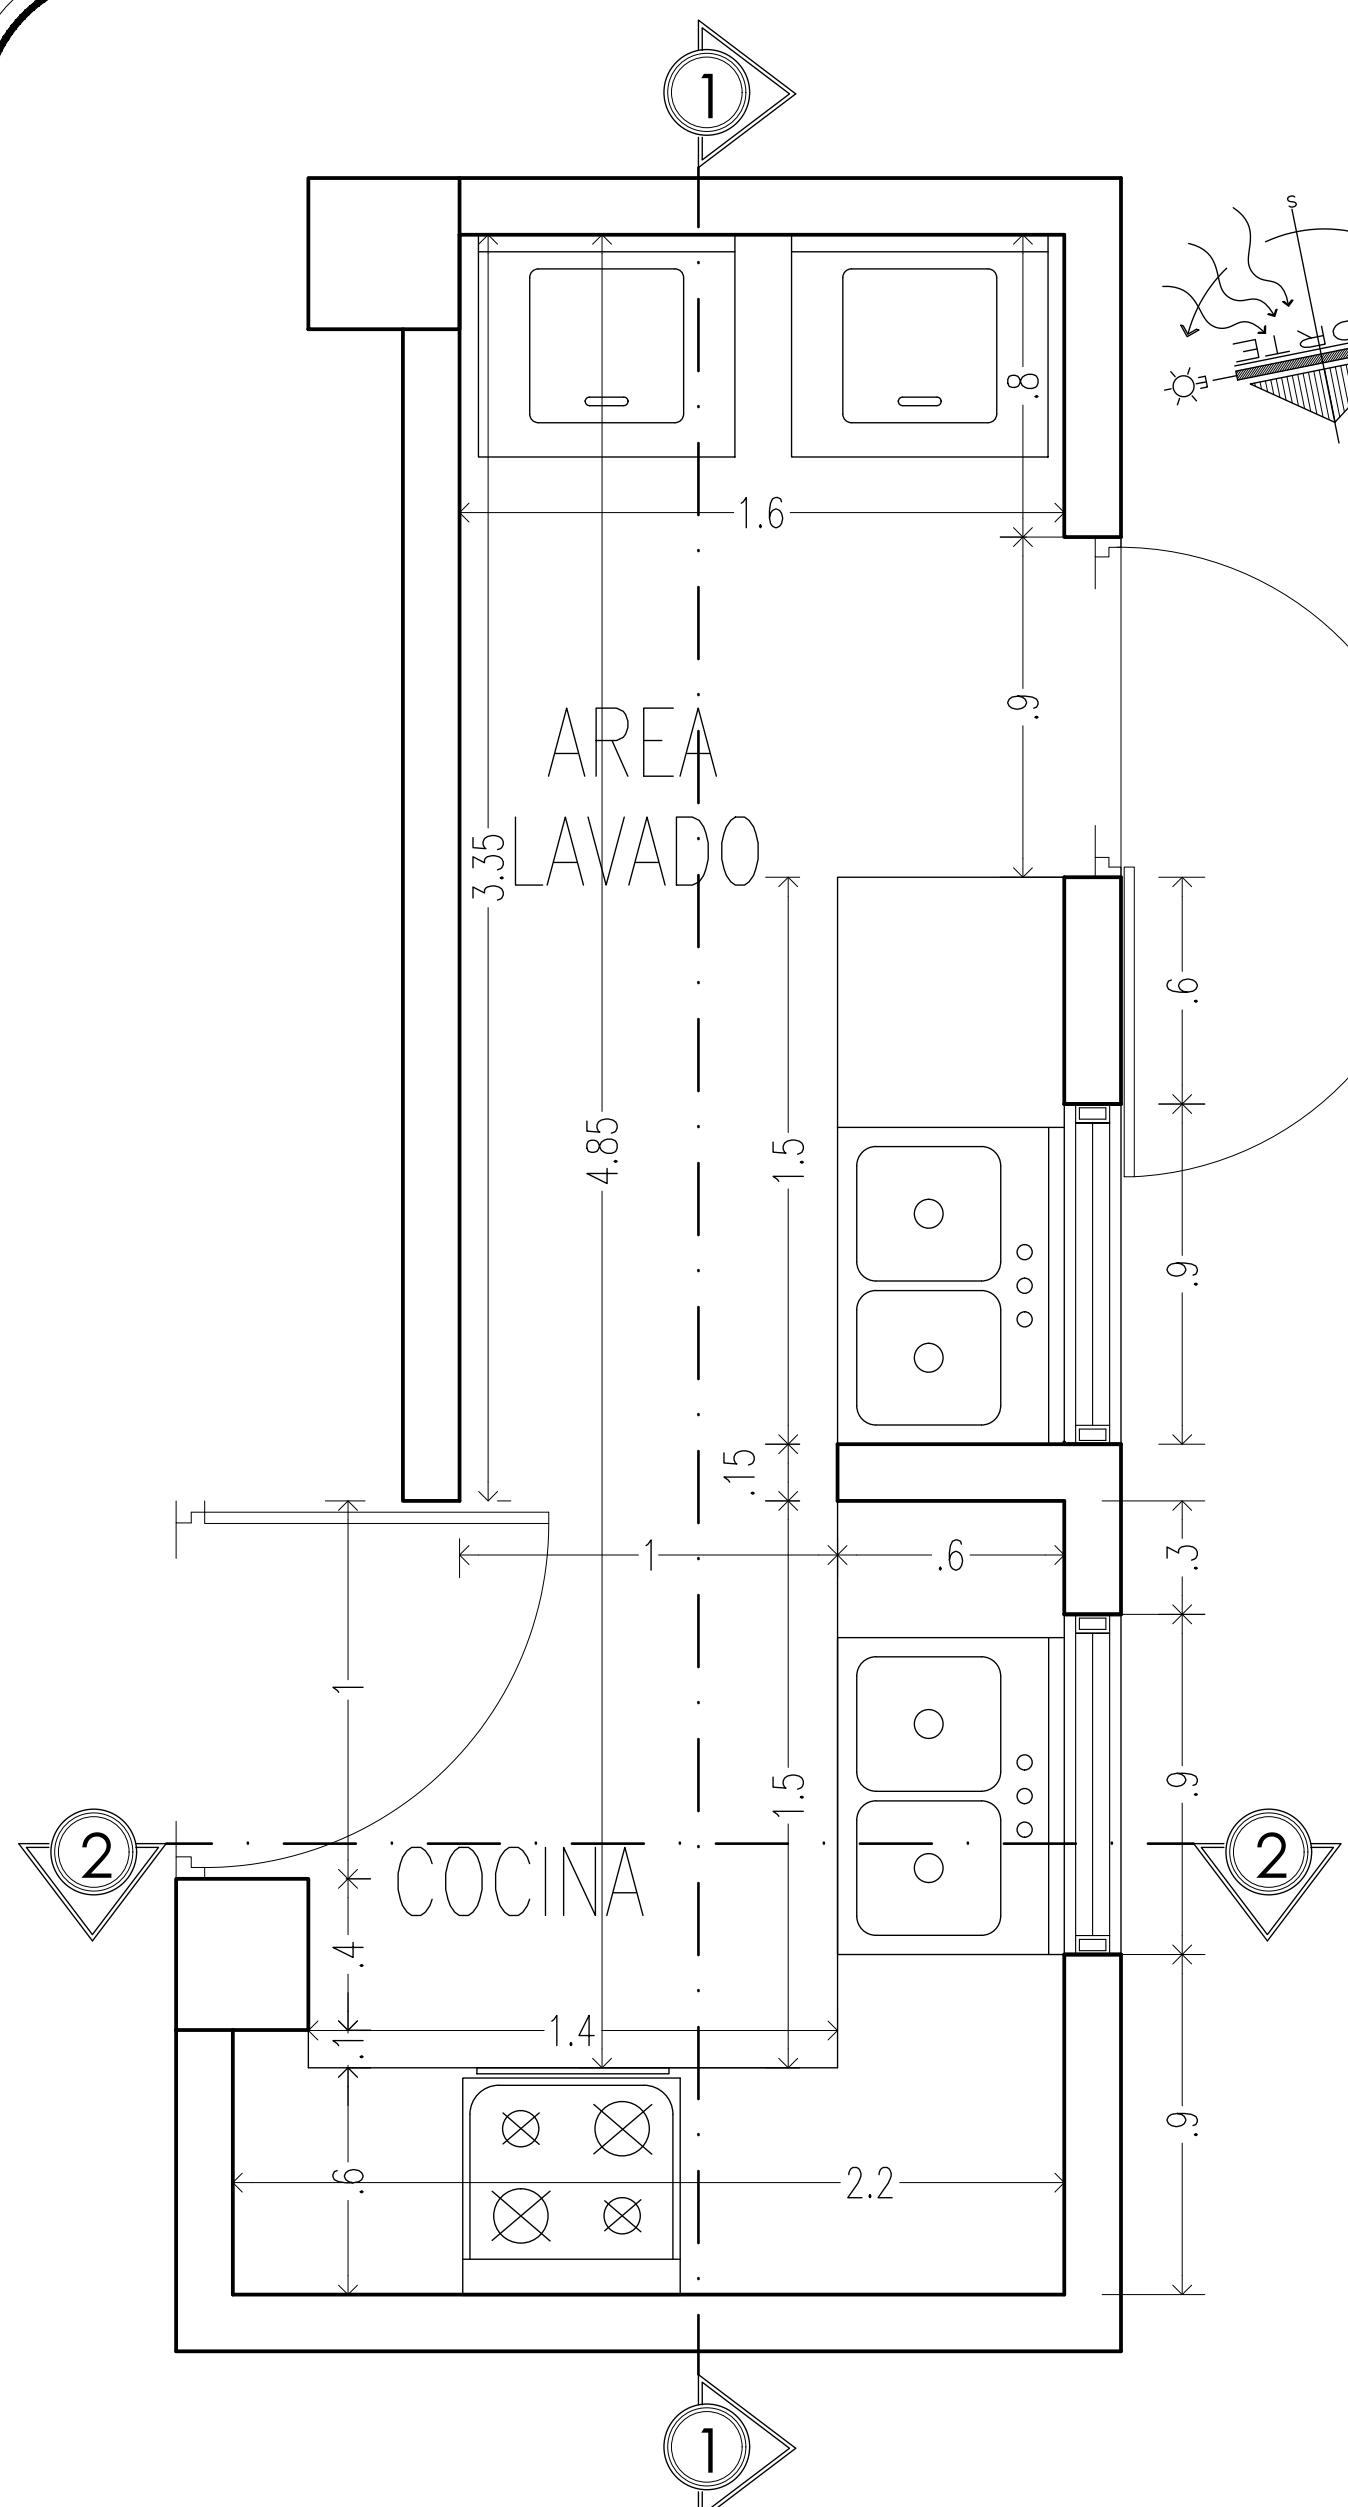


PLANTA DE COCINA/AREA DE LAVADO
(1er. Nivel) ESC.1:20

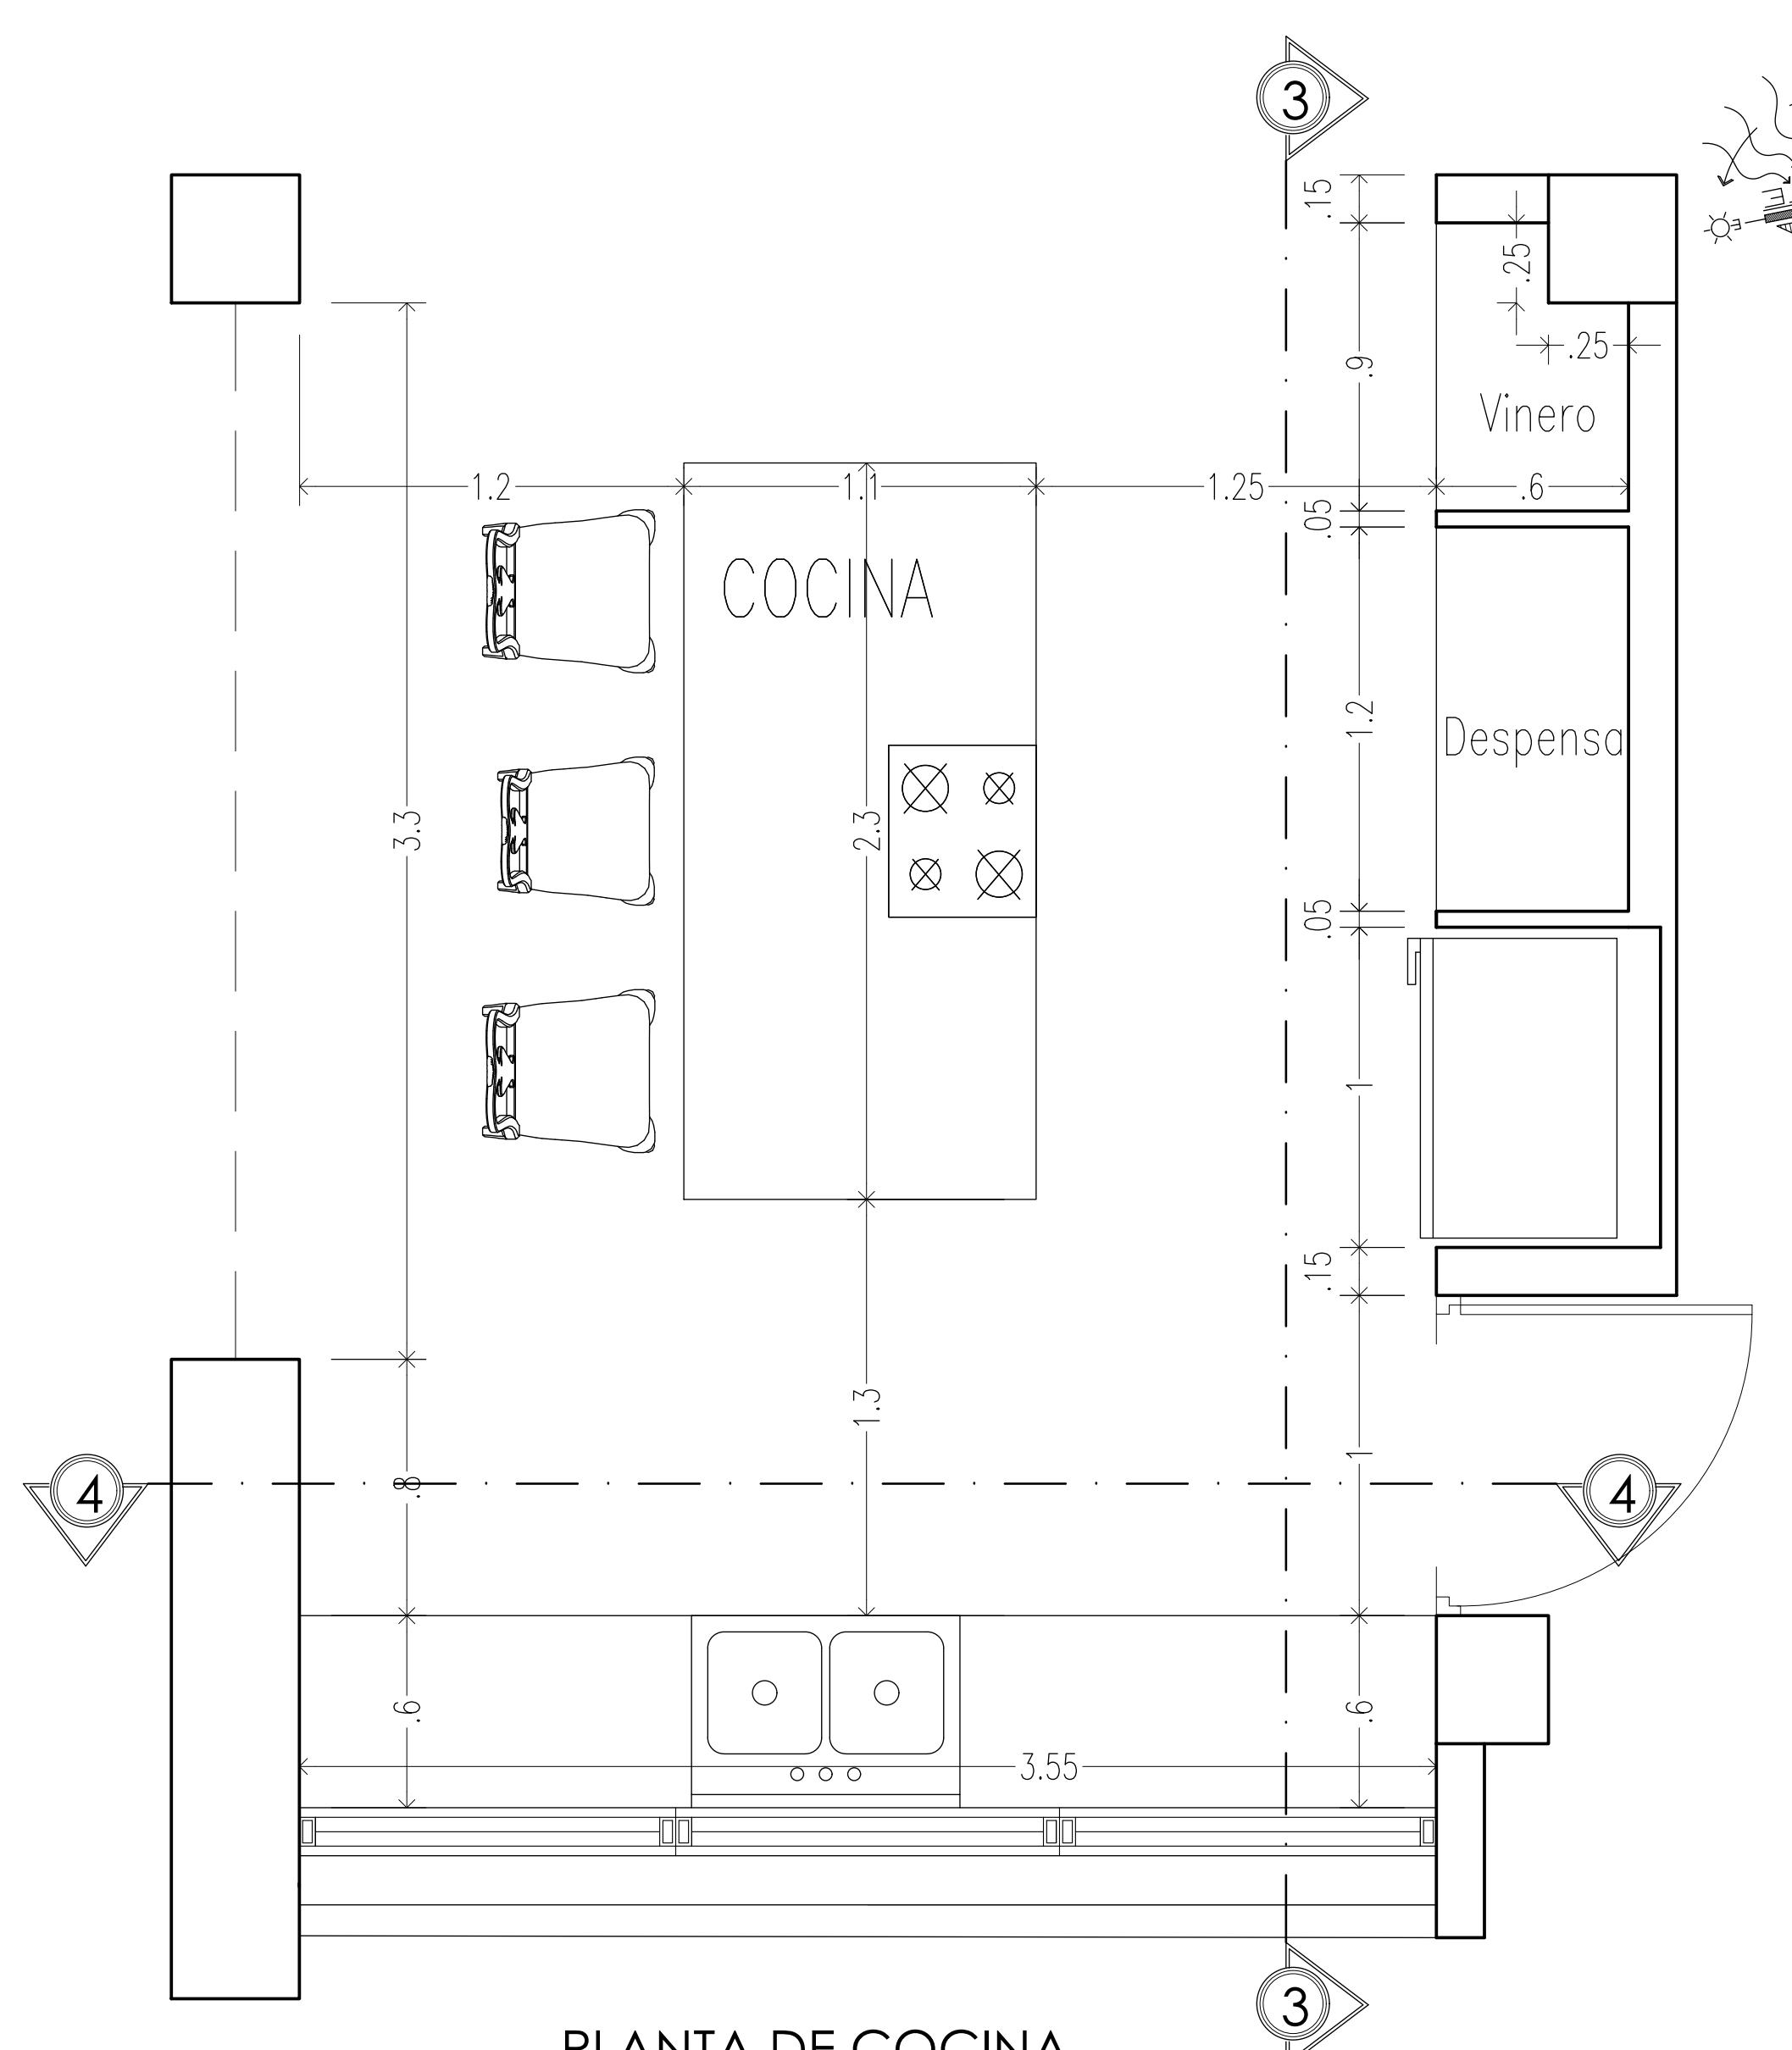


PLANTA DE COCINA
(1er. Nivel) ESC.1:20

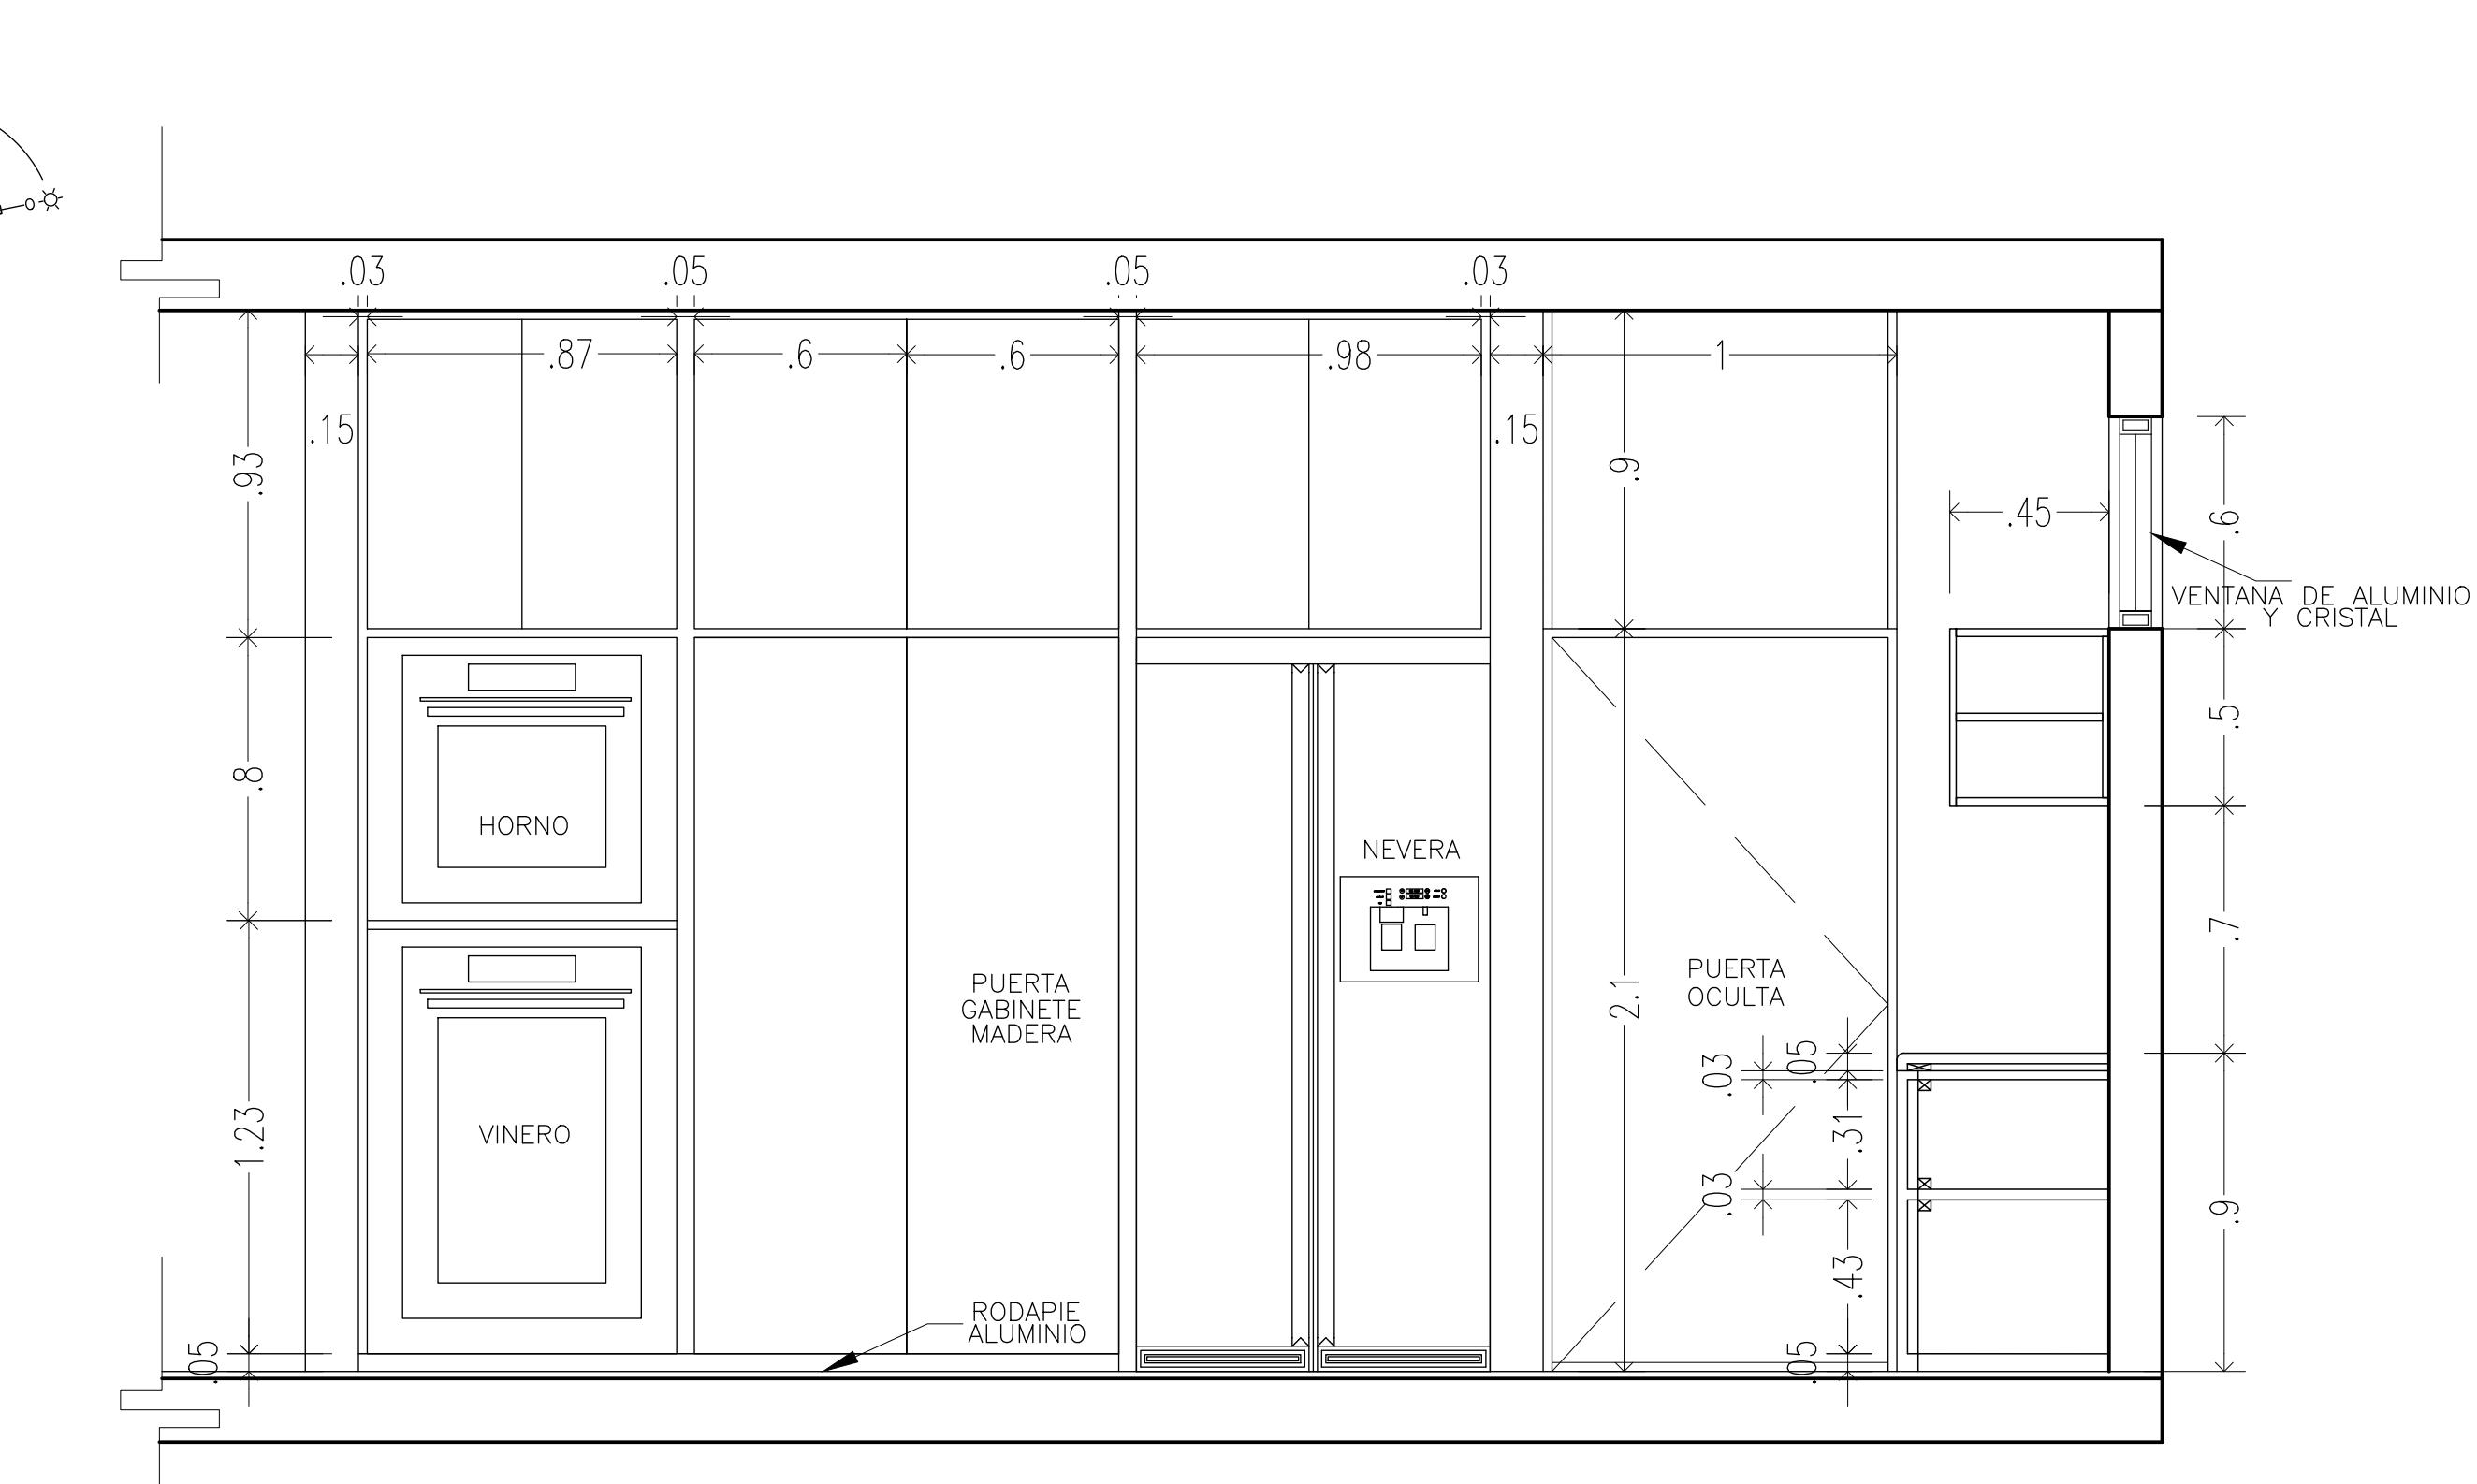


DETALLE DE COCINA
(1er. Nivel) ESC.1:20

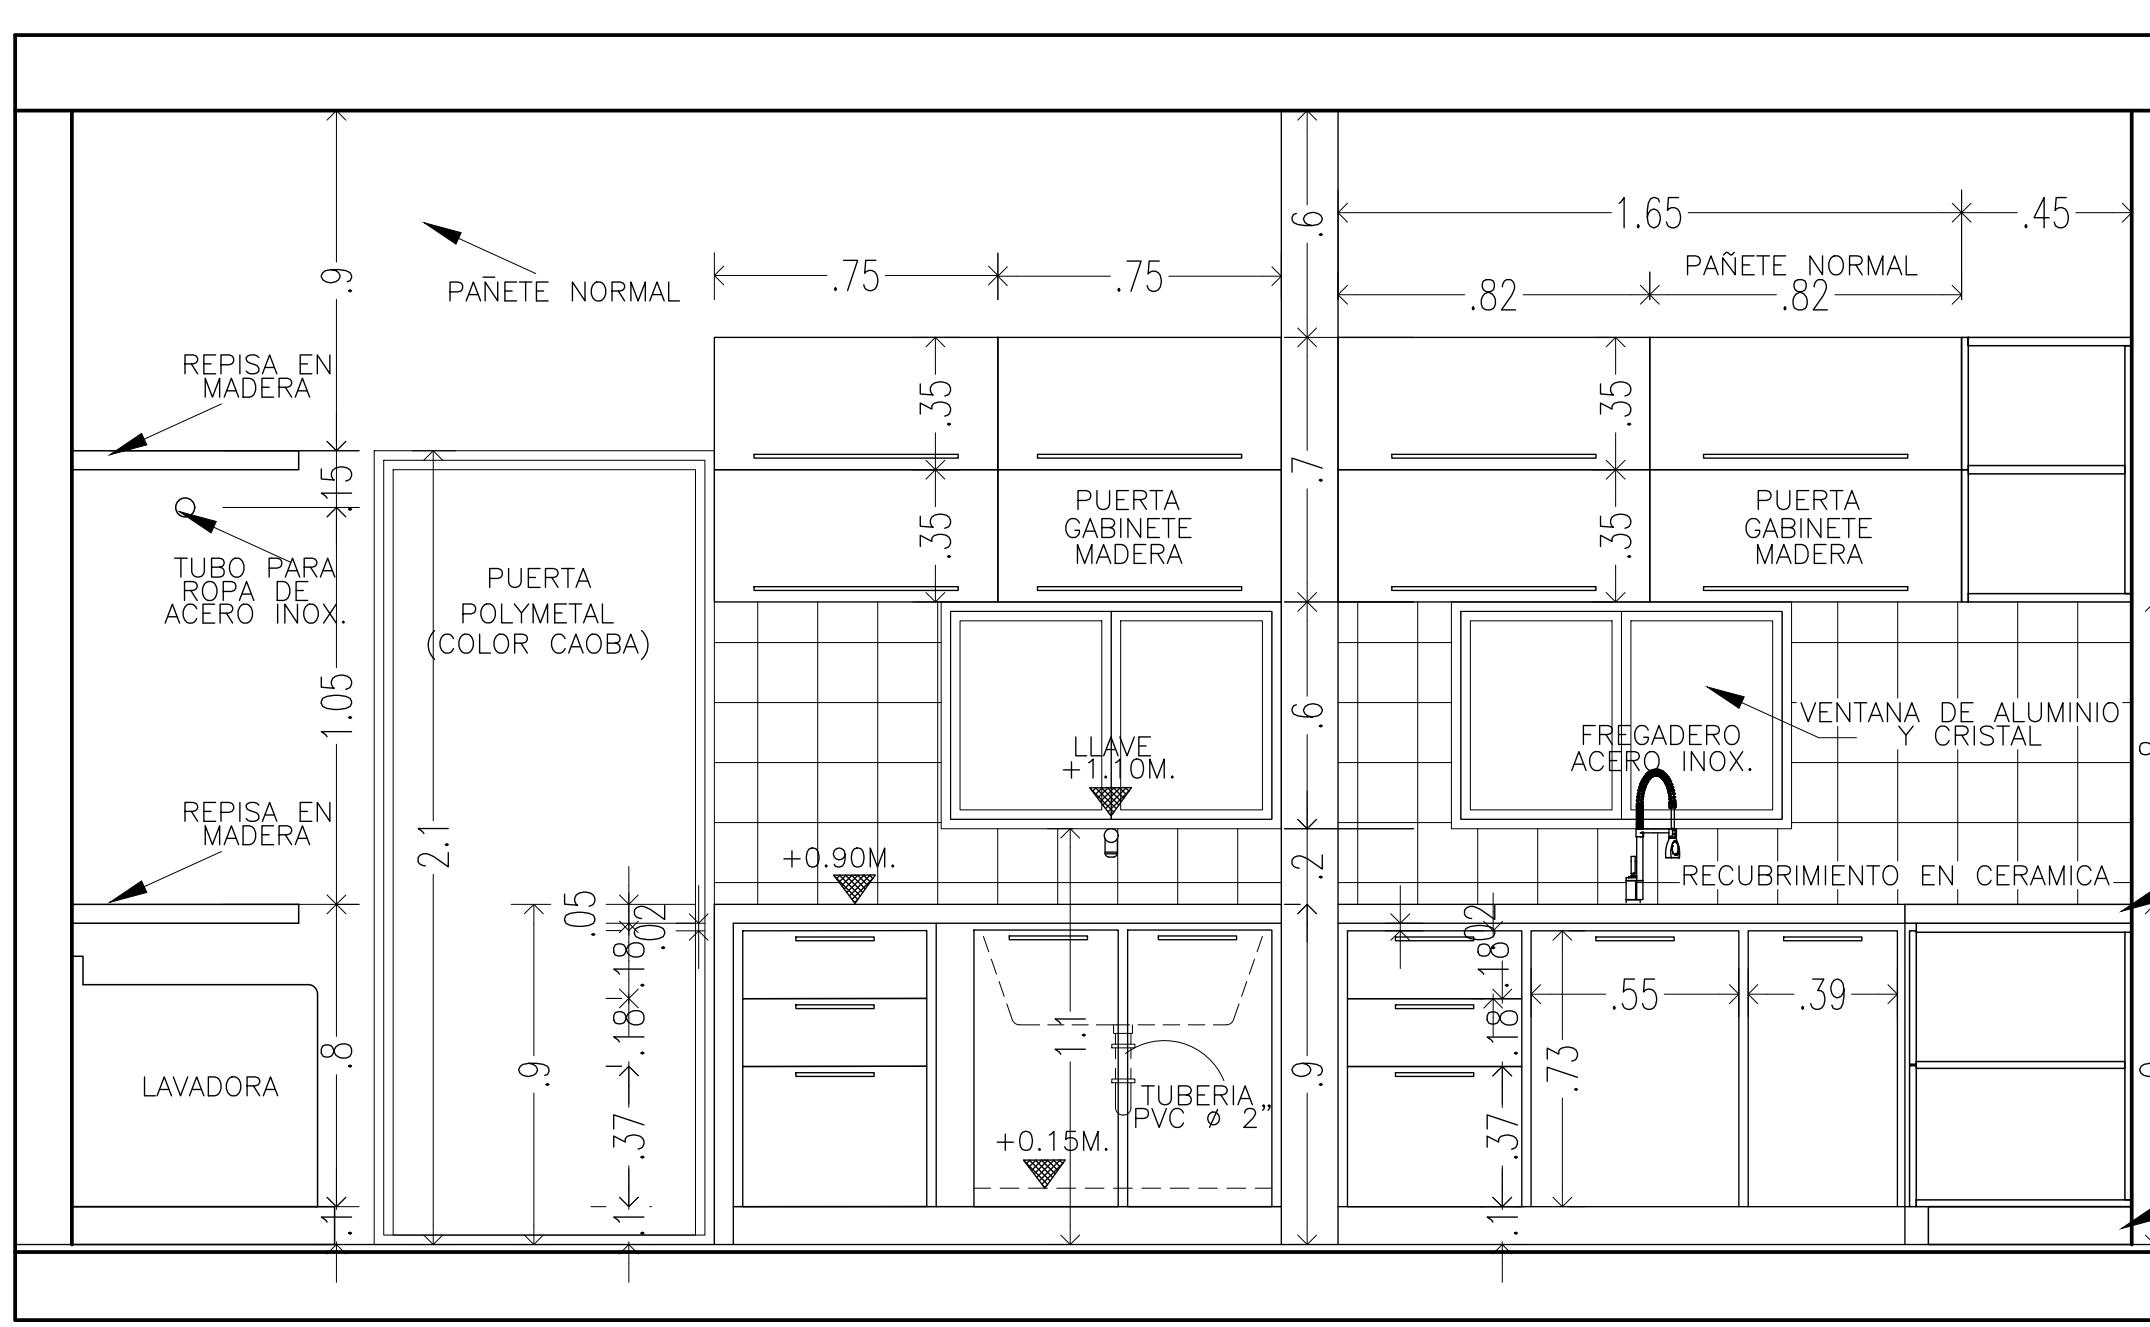

DETALLE DE COCINA/AREA DE LAVADO
(1er. Nivel) ESC.1:20

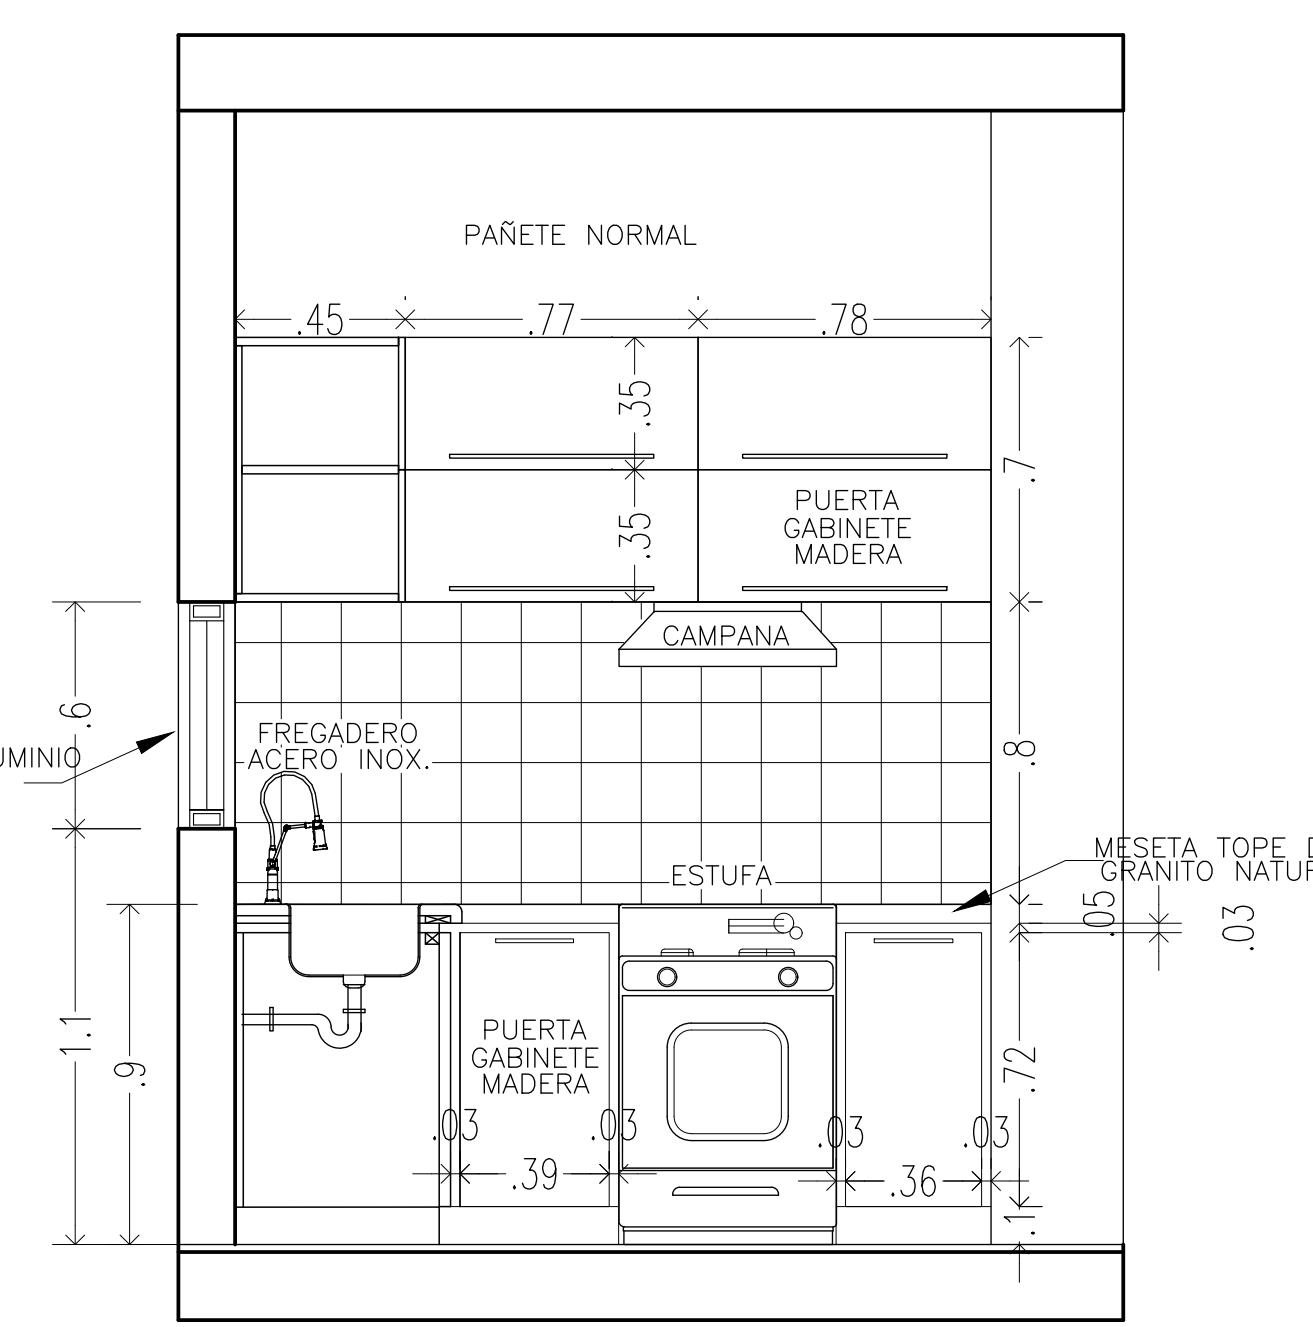


DETALLE DE COCINA/AREA DE LAVADO
(1er. Nivel) ESC.1:20

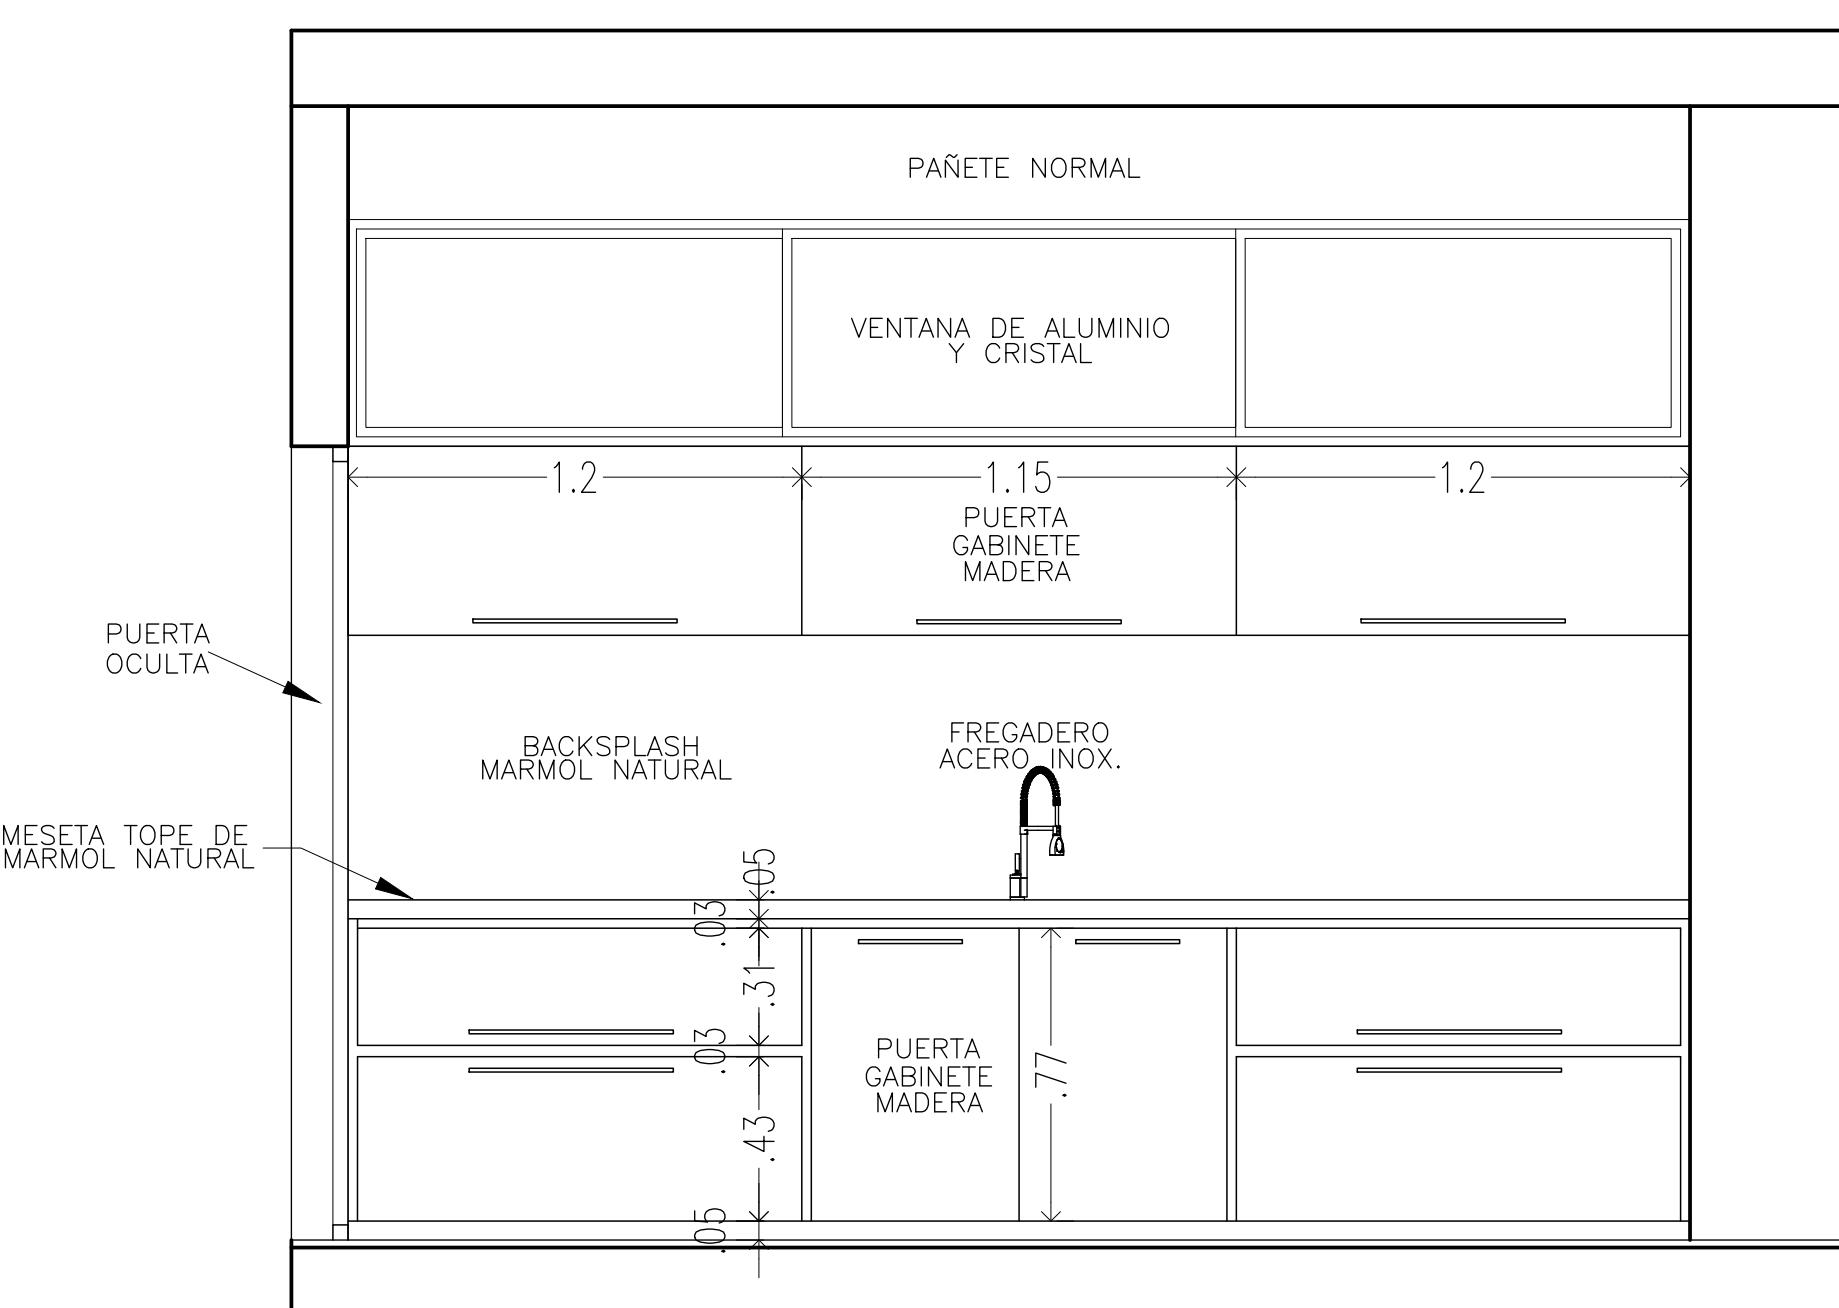


DETALLE DE COCINA
(1er. Nivel) ESC.1:20

Este proyecto es propiedad única y exclusivamente del arquitecto EDDY J. LOPEZ C. el cual sede la ejecución con estos planos de un solo proyecto en un solo lugar específico ya previamente establecido, si usted es destinatario o no de este proyecto, debe abstenerse totalmente de copiar, reproducir, distribuir, ceder a un familiar o particular, robar conceptos del mismo. La violación a esta disposición sería procesada legalmente con todo el peso de la justicia Dominicana por violar la ley sobre derecho de autor.


Villa Beato Reyes	LOCALIZACION: GUAGUI, LA VEGA		
PROPIETARIOS:			
JOSE LUIS BEATO PEÑA CED. 402-2763926-3			FIRMA
JOSELYN ANTONELIA REYES A. CED. 402-2737538-9			FIRMA
DISEÑO ARQUITECTONICO: SHERYL LOPEZ R.	CODA : 46298		
DISEÑO SANITARIO: ING. FRANK FELIZ LOPEZ	CODA : 19796		
DISEÑO ESTRUCTURAL: HIPOLITO MORONI LILONG	CODA : 4166		
RESPONSABLE DEL PROYECTO: ARQUITECTO: EDDY J. LOPEZ CODA : 13.638	DIBUJO : D 18 U J 0 AVENIDA AMERICANA #40 809-575-7056 809-399-8344 FECHA: 1 - 9 - 2021	ESCALA : INDICADA	HOJA # 6/23

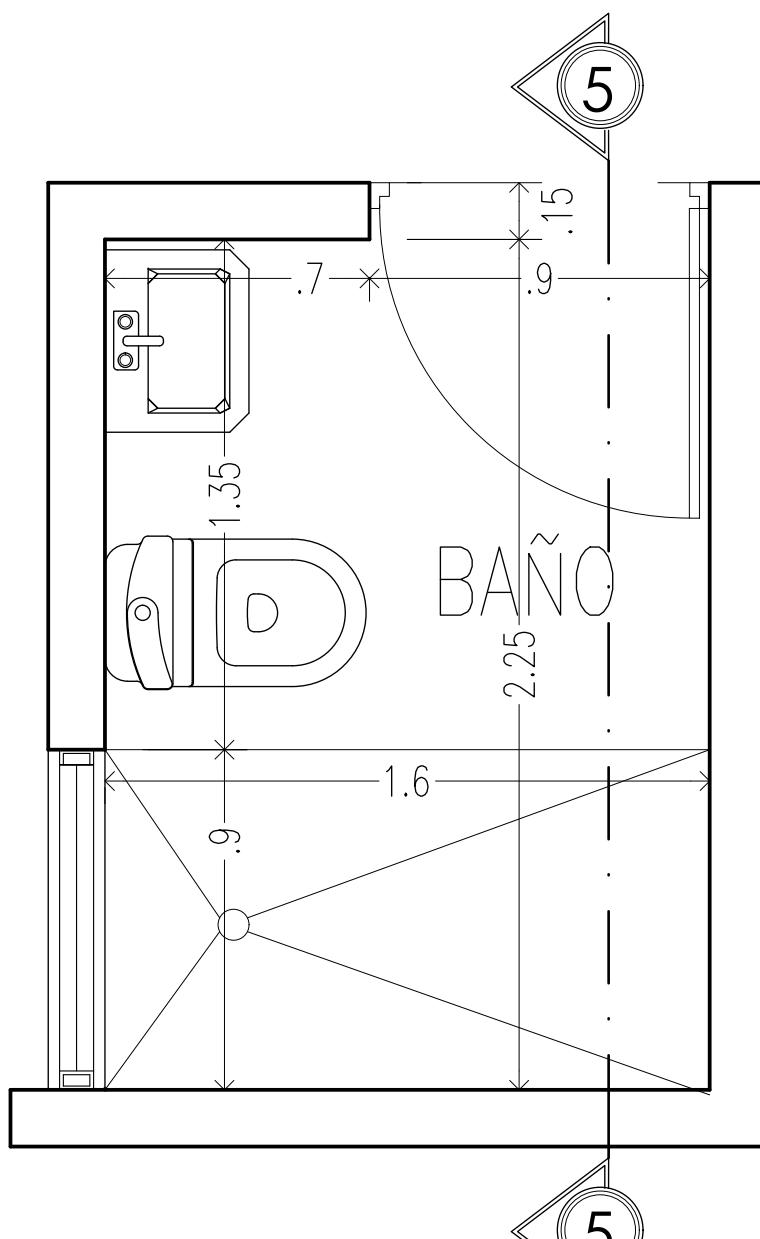

PLANTA DE BAÑO
(1er. Nivel) ESC.1:20

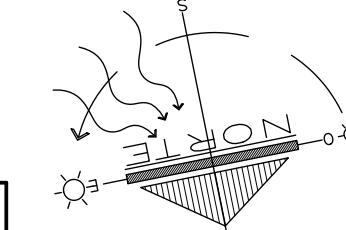

VENTANA DE ALUMINIO Y CRISTAL

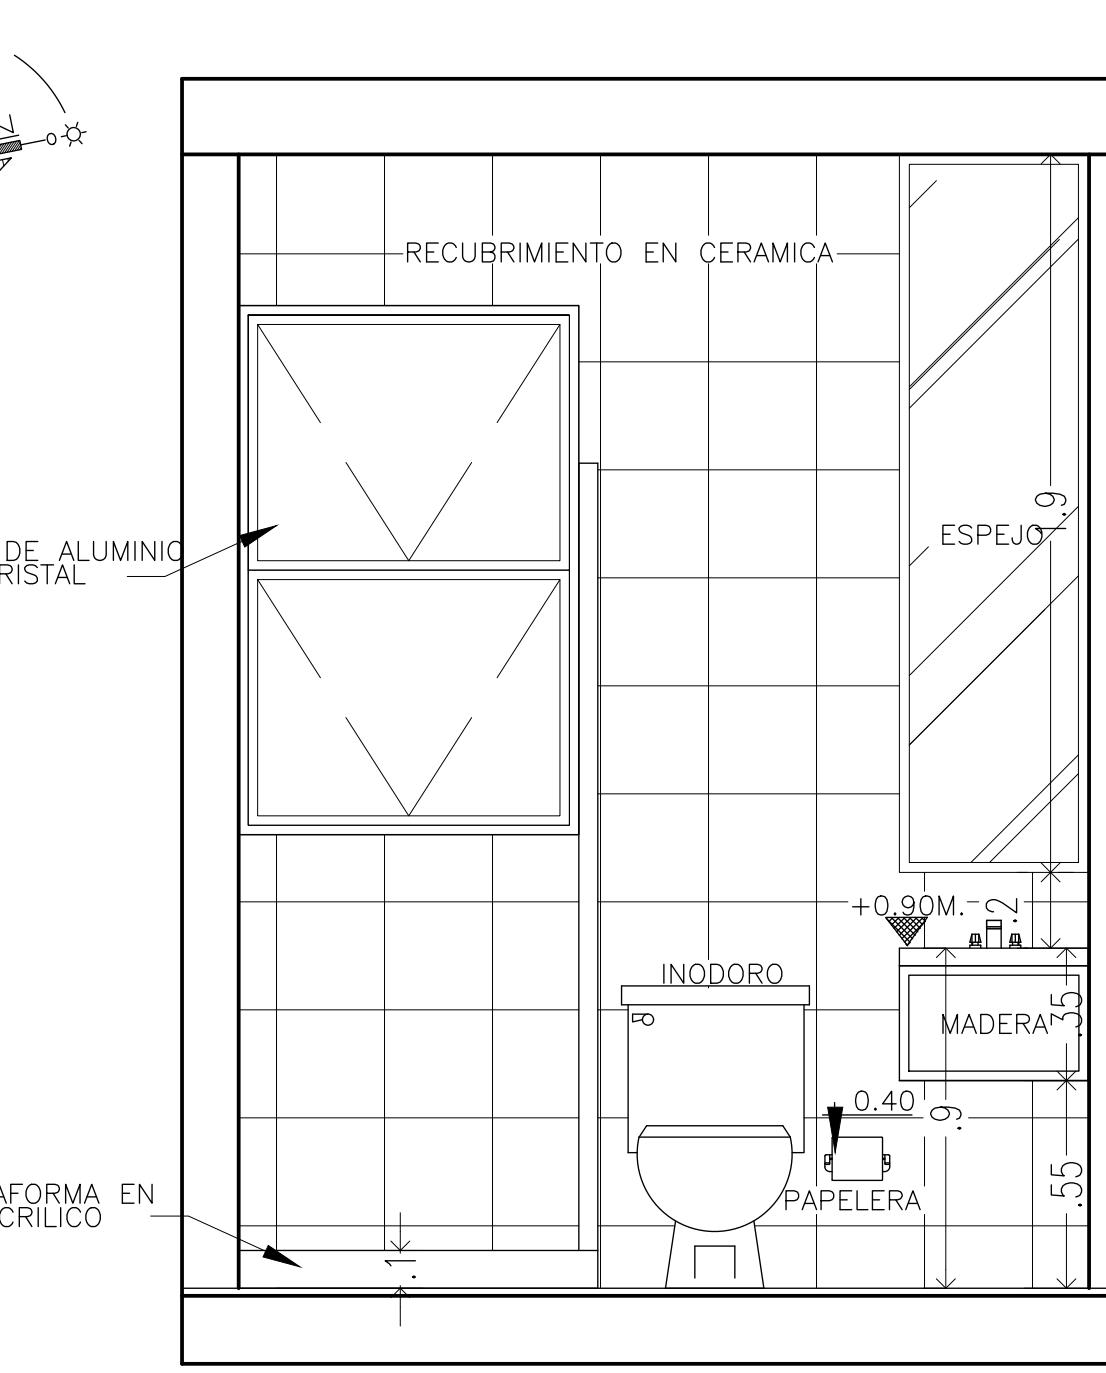

RECOBERTIMIENTO EN CERAMICA

ESPEJO

INODORO

PAPELERA

MADERA

PLATAFORMA EN ACRILICO

BAÑO



VENTANA DE ALUMINIO Y CRISTAL

RECOBERTIMIENTO EN CERAMICA

ESPEJO

INODORO

PAPELERA

MADERA

PLATAFORMA EN ACRILICO

BAÑO



VENTANA DE ALUMINIO Y CRISTAL

RECOBERTIMIENTO EN CERAMICA

ESPEJO

INODORO

PAPELERA

MADERA

PLATAFORMA EN ACRILICO

BAÑO



VENTANA DE ALUMINIO Y CRISTAL

RECOBERTIMIENTO EN CERAMICA

ESPEJO

INODORO

PAPELERA

MADERA

PLATAFORMA EN ACRILICO

BAÑO



VENTANA DE ALUMINIO Y CRISTAL

RECOBERTIMIENTO EN CERAMICA

ESPEJO

INODORO

PAPELERA

MADERA

PLATAFORMA EN ACRILICO

BAÑO



VENTANA DE ALUMINIO Y CRISTAL

RECOBERTIMIENTO EN CERAMICA

ESPEJO

INODORO

PAPELERA

MADERA

PLATAFORMA EN ACRILICO

BAÑO



VENTANA DE ALUMINIO Y CRISTAL

RECOBERTIMIENTO EN CERAMICA

ESPEJO

INODORO

PAPELERA

MADERA

PLATAFORMA EN ACRILICO

BAÑO



VENTANA DE ALUMINIO Y CRISTAL

RECOBERTIMIENTO EN CERAMICA

ESPEJO

INODORO

PAPELERA

MADERA

PLATAFORMA EN ACRILICO

BAÑO



VENTANA DE ALUMINIO Y CRISTAL

RECOBERTIMIENTO EN CERAMICA

ESPEJO

INODORO

PAPELERA

MADERA

PLATAFORMA EN ACRILICO

BAÑO



VENTANA DE ALUMINIO Y CRISTAL

RECOBERTIMIENTO EN CERAMICA

ESPEJO

INODORO

PAPELERA

MADERA

PLATAFORMA EN ACRILICO

BAÑO



VENTANA DE ALUMINIO Y CRISTAL

RECOBERTIMIENTO EN CERAMICA

ESPEJO

INODORO

PAPELERA

MADERA

PLATAFORMA EN ACRILICO

BAÑO



VENTANA DE ALUMINIO Y CRISTAL

RECOBERTIMIENTO EN CERAMICA

ESPEJO

INODORO

PAPELERA

MADERA

PLATAFORMA EN ACRILICO

BAÑO



VENTANA DE ALUMINIO Y CRISTAL

RECOBERTIMIENTO EN CERAMICA

ESPEJO

INODORO

PAPELERA

MADERA

PLATAFORMA EN ACRILICO

BAÑO



VENTANA DE ALUMINIO Y CRISTAL

RECOBERTIMIENTO EN CERAMICA

ESPEJO

INODORO

PAPELERA

MADERA

PLATAFORMA EN ACRILICO

BAÑO



VENTANA DE ALUMINIO Y CRISTAL

RECOBERTIMIENTO EN CERAMICA

ESPEJO

INODORO

PAPELERA

MADERA

PLATAFORMA EN ACRILICO

BAÑO

VENTANA DE ALUMINIO Y CRISTAL

RECOBERTIMIENTO EN CERAMICA

ESPEJO

INODORO

PAPELERA

MADERA

PLATAFORMA EN ACRILICO

BAÑO

VENTANA DE ALUMINIO Y CRISTAL

RECOBERTIMIENTO EN CERAMICA

ESPEJO

INODORO

PAPELERA

MADERA

PLATAFORMA EN ACRILICO

BAÑO

VENTANA DE ALUMINIO Y CRISTAL

RECOBERTIMIENTO EN CERAMICA

ESPEJO

INODORO

PAPELERA

MADERA

PLATAFORMA EN ACRILICO

BAÑO

VENTANA DE ALUMINIO Y CRISTAL

RECOBERTIMIENTO EN CERAMICA

ESPEJO

INODORO

PAPELERA

MADERA

PLATAFORMA EN ACRILICO

BAÑO

VENTANA DE ALUMINIO Y CRISTAL

RECOBERTIMIENTO EN CERAMICA

ESPEJO

INODORO


PAPELERA

MADERA


PLATAFORMA EN ACRILICO

BAÑO


VENTANA DE ALUMINIO Y CRISTAL

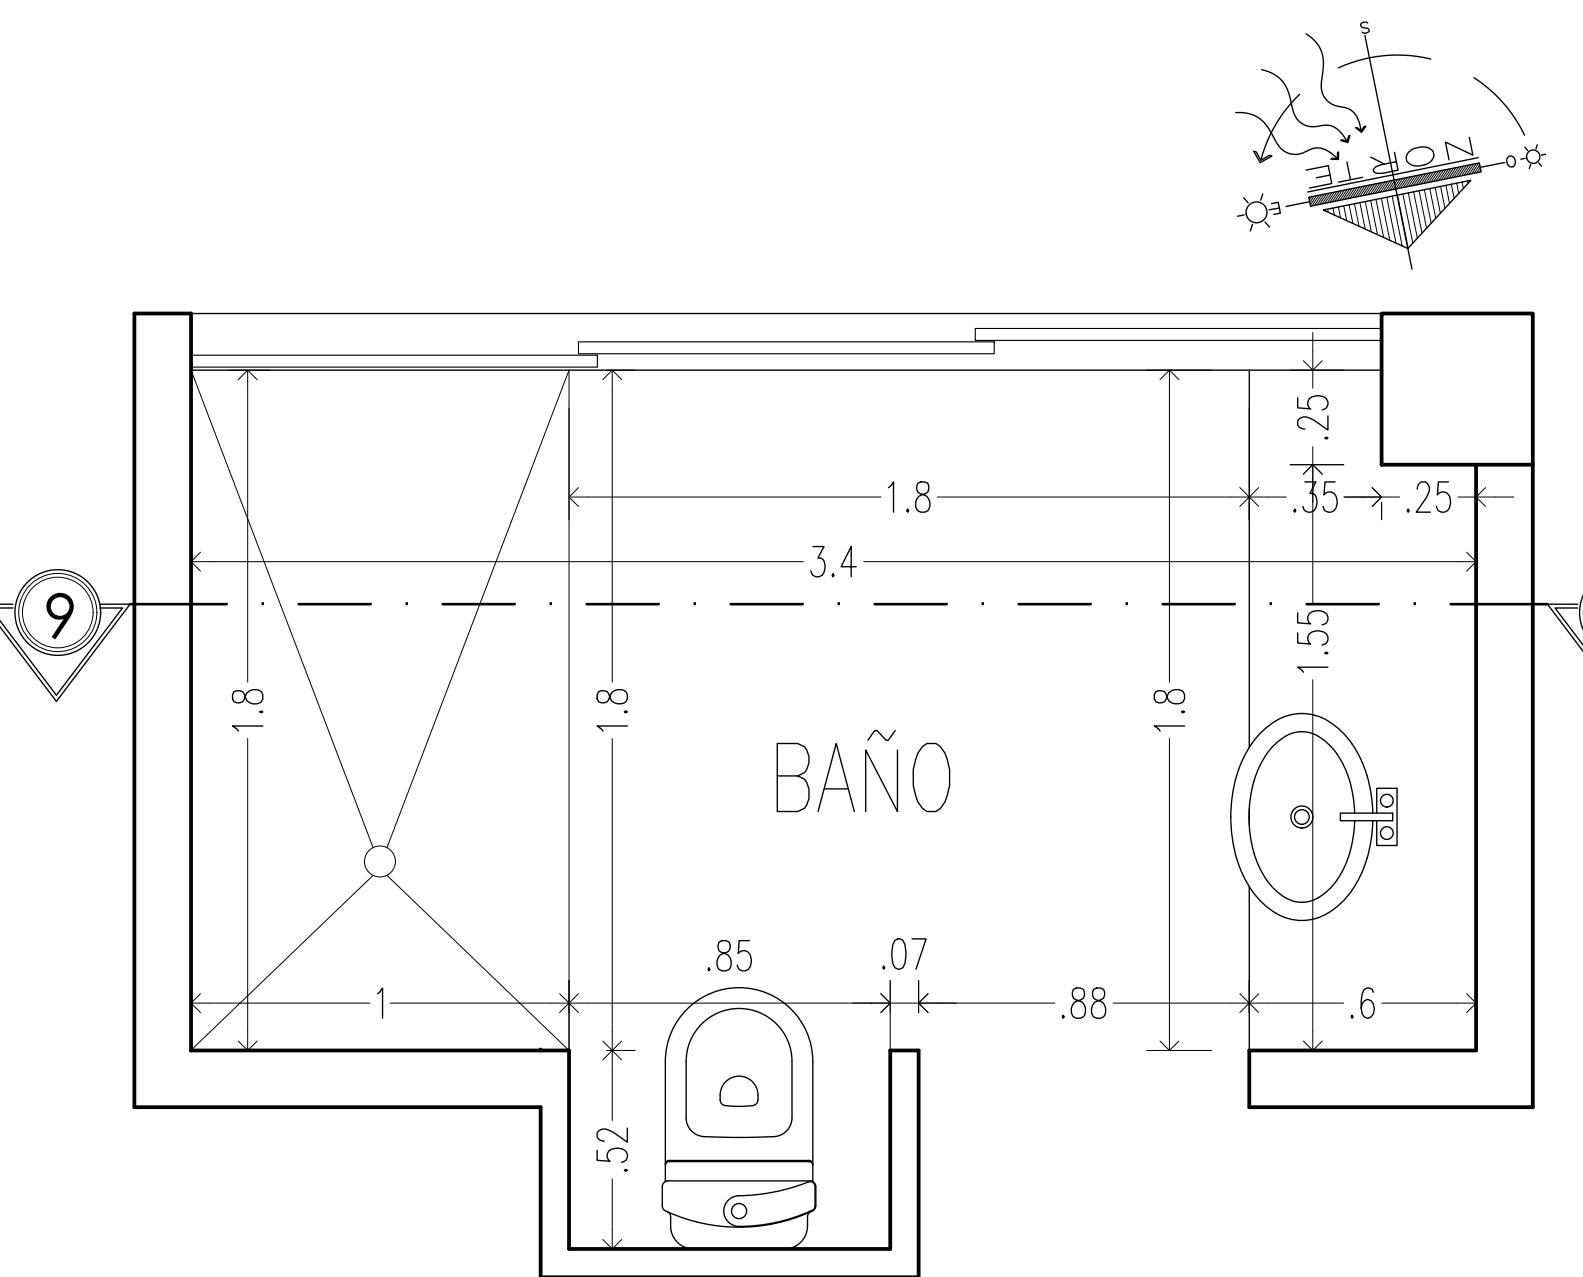


PLANTA DE BAÑO
(2do. Nivel) ESC.1:20

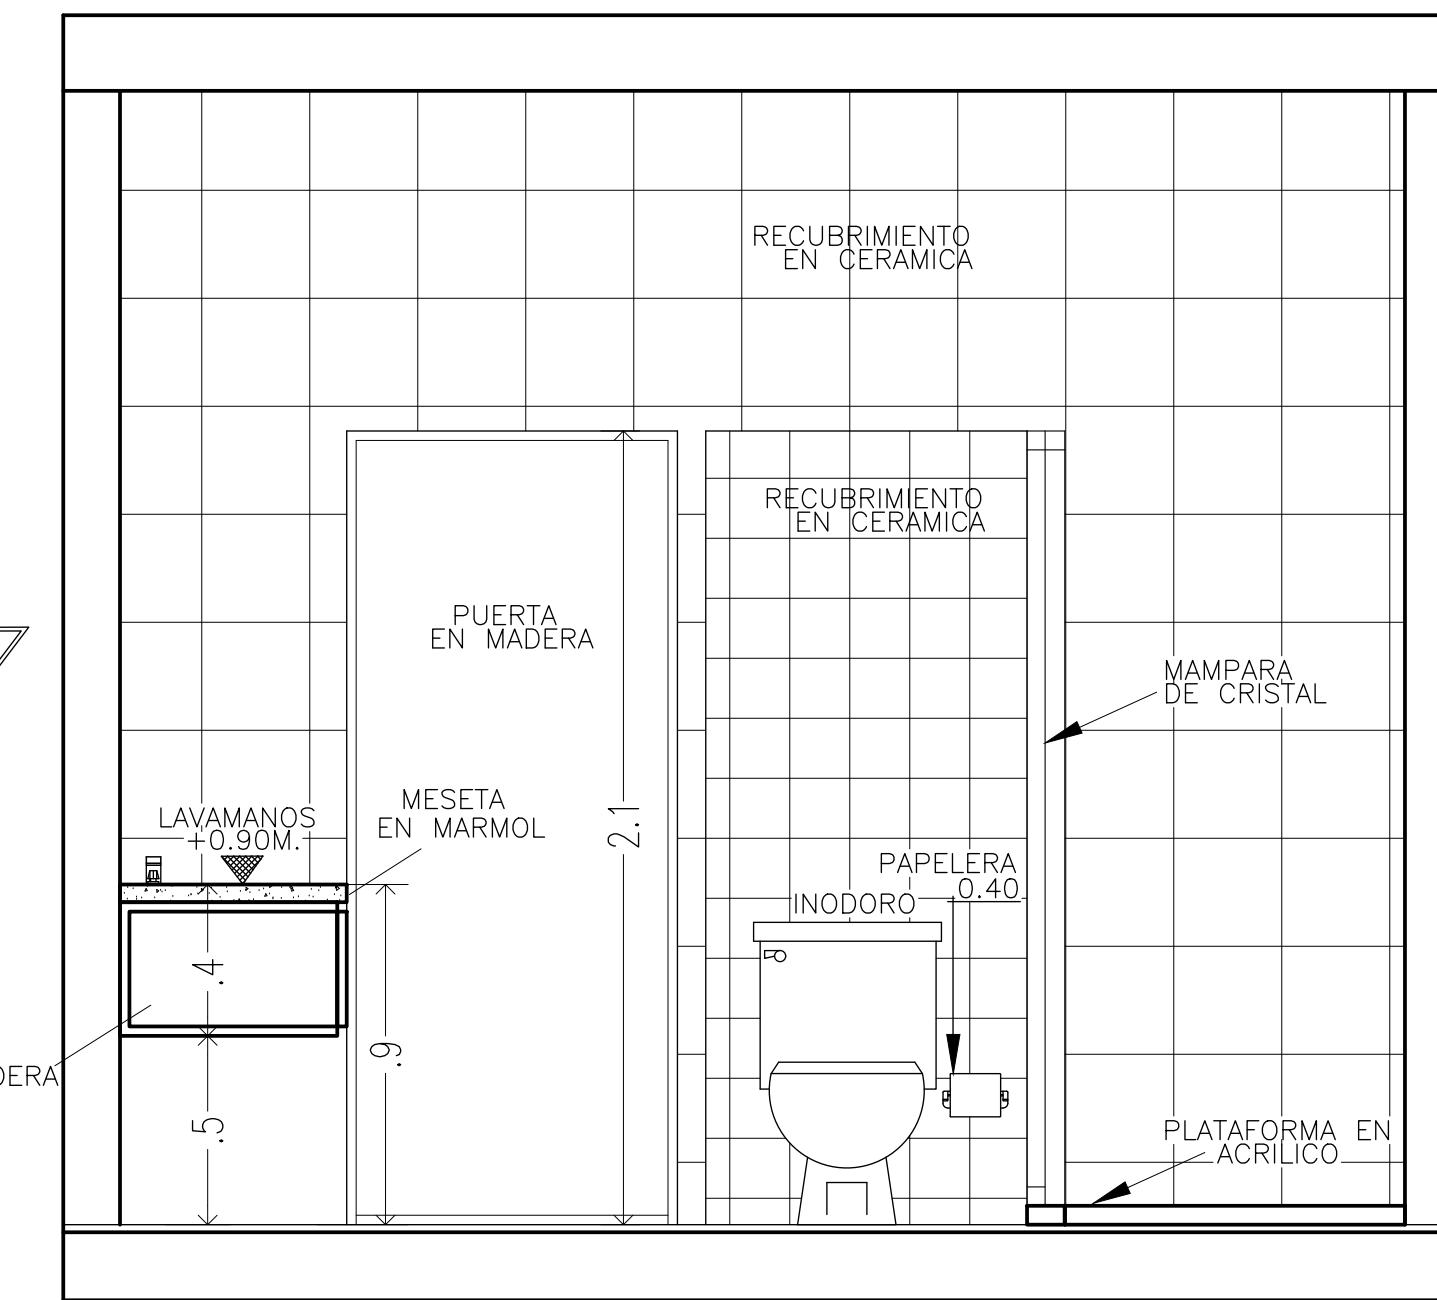


DETALLE DE BAÑO
(1er. Nivel) ESC.1:20

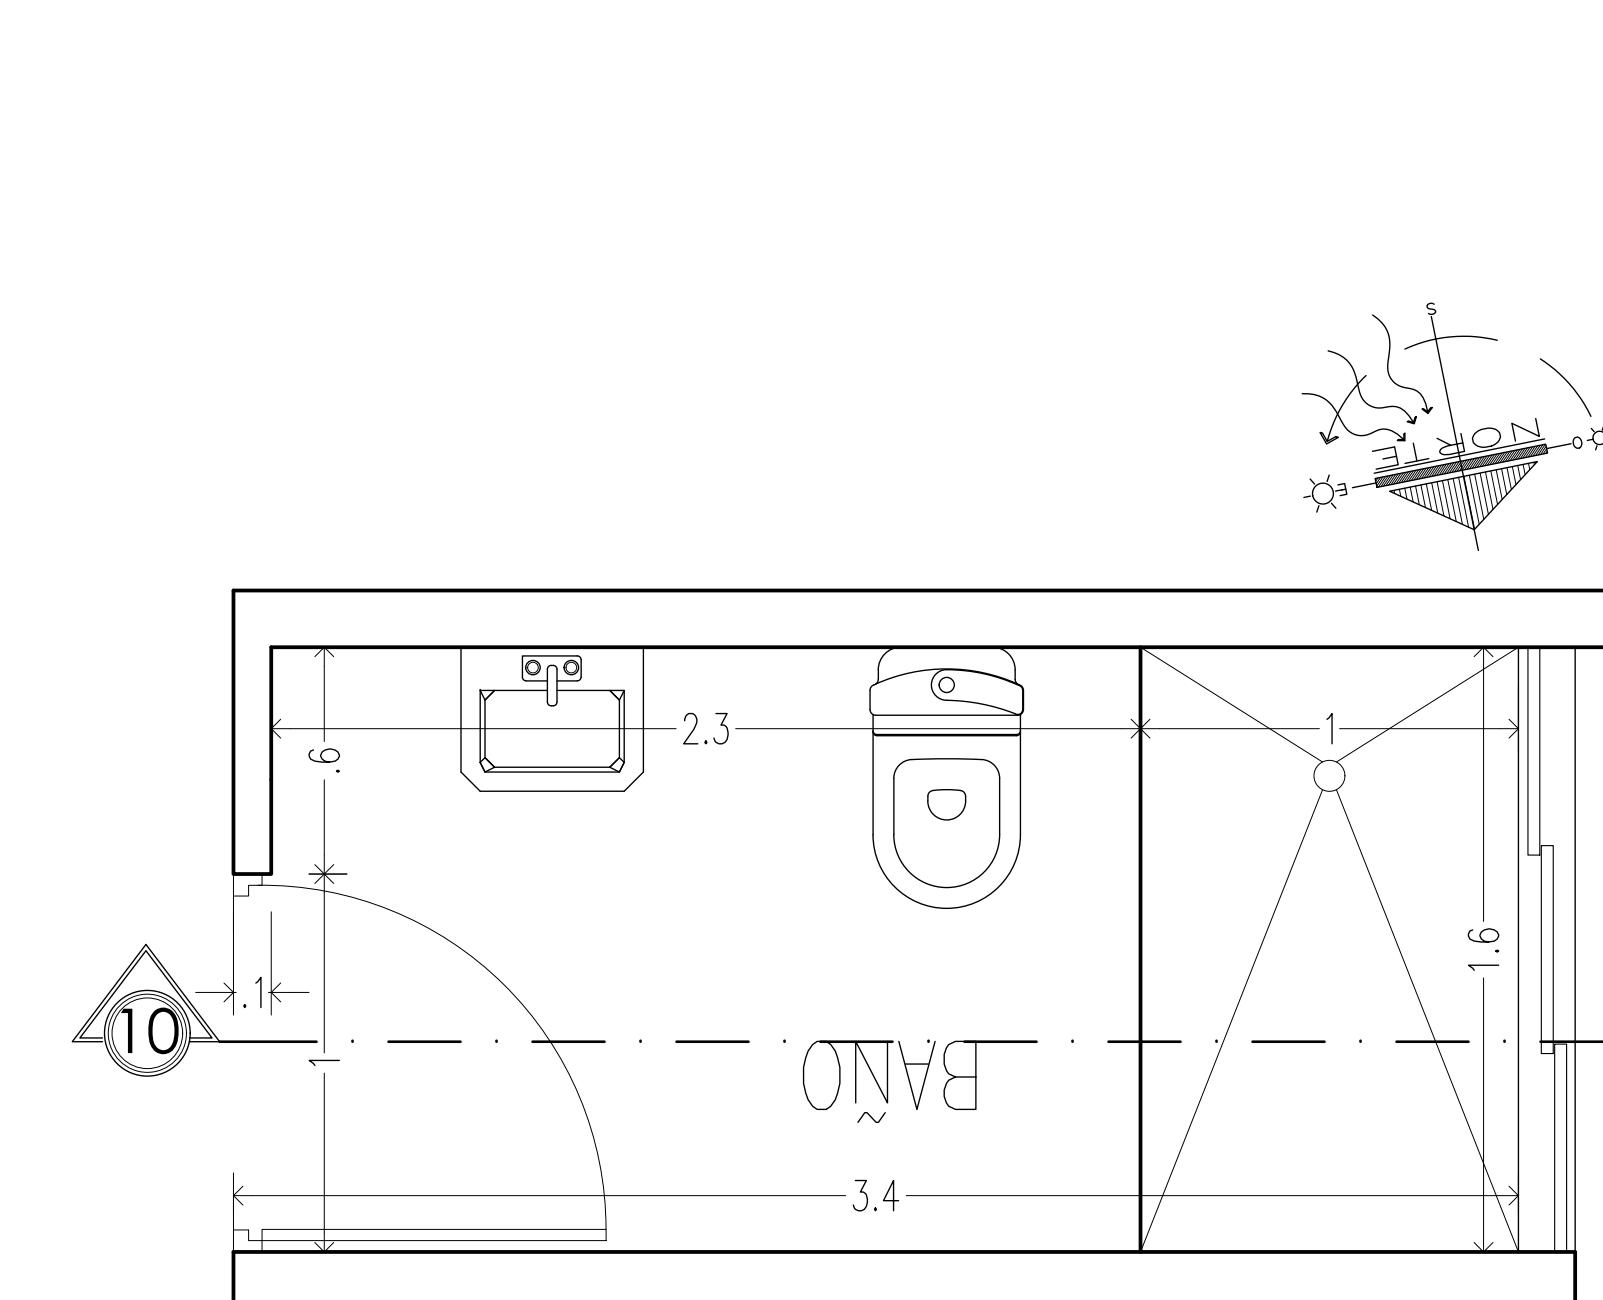


PLANTA DE BAÑO
(2do. Nivel) ESC.1:20

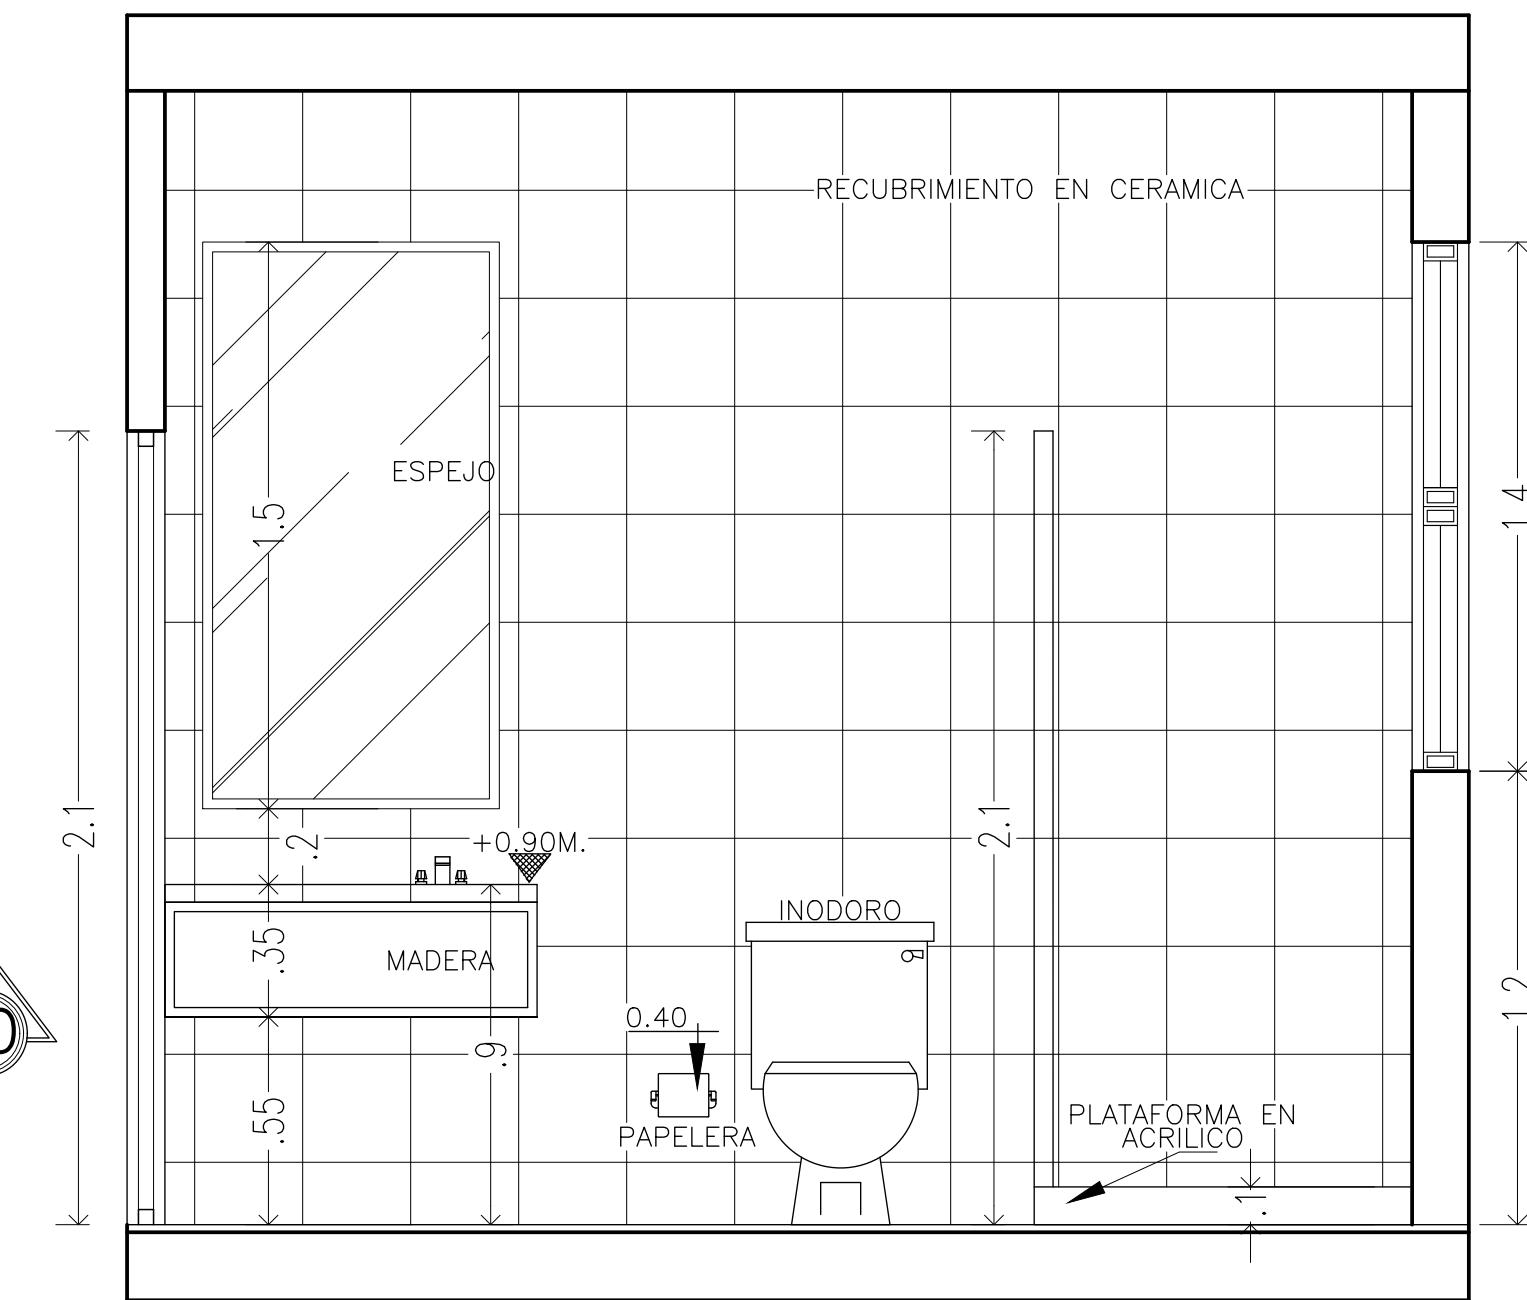

DETALLE DE BAÑO
(1er. Nivel) ESC.1:20

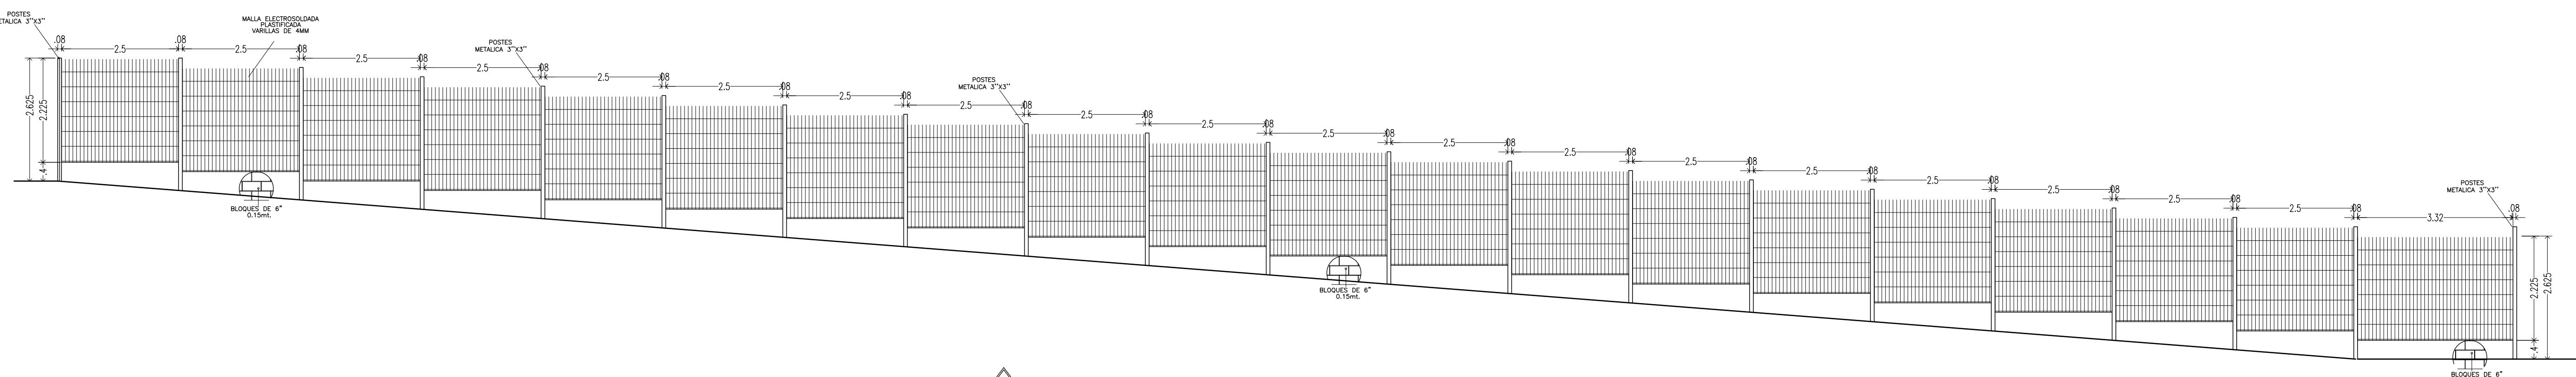


DETALLE DE VERJA
ESCALA: 1:75

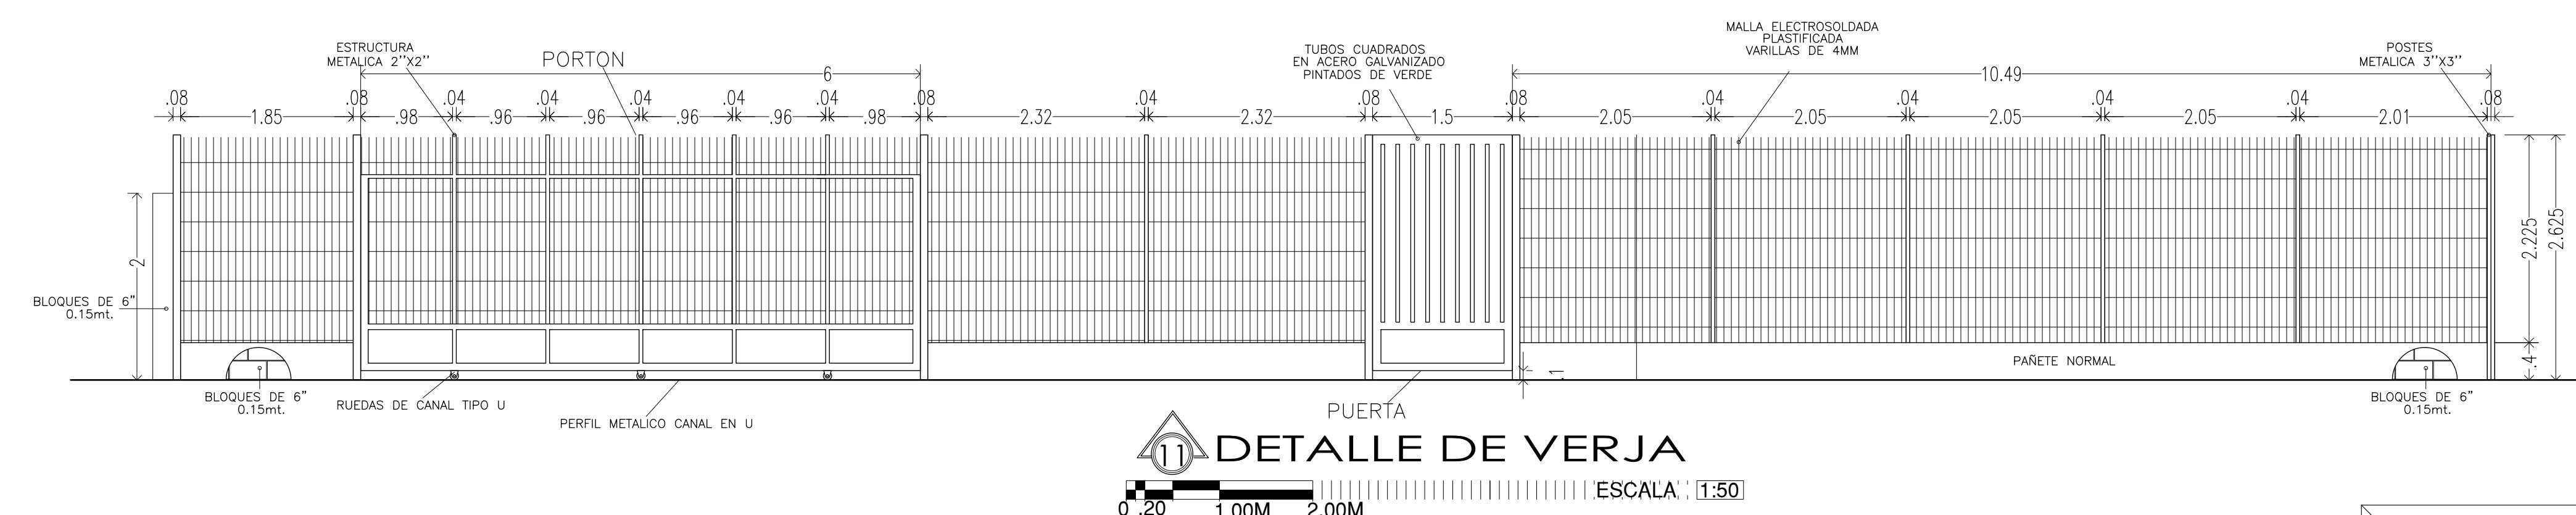


DETALLE DE VERJA
ESCALA: 1:50

Este proyecto es propiedad única y exclusivamente del arquitecto EDDY J. LOPEZ C. el cual sede la ejecución con estos planos de un solo proyecto en un solo lugar específico ya previamente establecido, si usted es destinatario o no de este proyecto, debe de abstenerse totalmente de copiar, reproducir, distribuir, ceder a un familiar o particular, robar conceptos del mismo. La violación a esta disposición sería procesada legalmente con todo el peso de la justicia Dominicana por violar la ley sobre derecho de autor.

Villa Beato Reyes	LOCALIZACION: GUAIGU, LA VEGA
PROPIETARIOS:	
JOSE LUIS BEATO PEÑA CED. 402-2763926-3	FIRMA
JOSELYN ANTONELIA REYES A. CED. 402-2737538-9	FIRMA
DISEÑO ARQUITECTONICO: SHERYL LOPEZ R. CODA :46298	
DISEÑO SANITARIO: INC. FRANK FELIZ LOPEZ CODA :19796	
DISEÑO ESTRUCT: HIPOLITO MORONTA LILONG CODA : 4166	
DISEÑO ELECTRICO: HIPOLITO MORONTA LILONG CODA : 4166	
RESPONSABLE DEL PROYECTO: ARQUITECTO: EDDY J. LOPEZ CODA :13,638	
DIBUJO : 01 B I J O EL ARQUITECTURA AVENIDA INBERT #4 LA VEGA 809-573-7056 809-399-8344	ESCALA
FECHA: 1 - 9 - 2021	HOJA #
INDICADA	

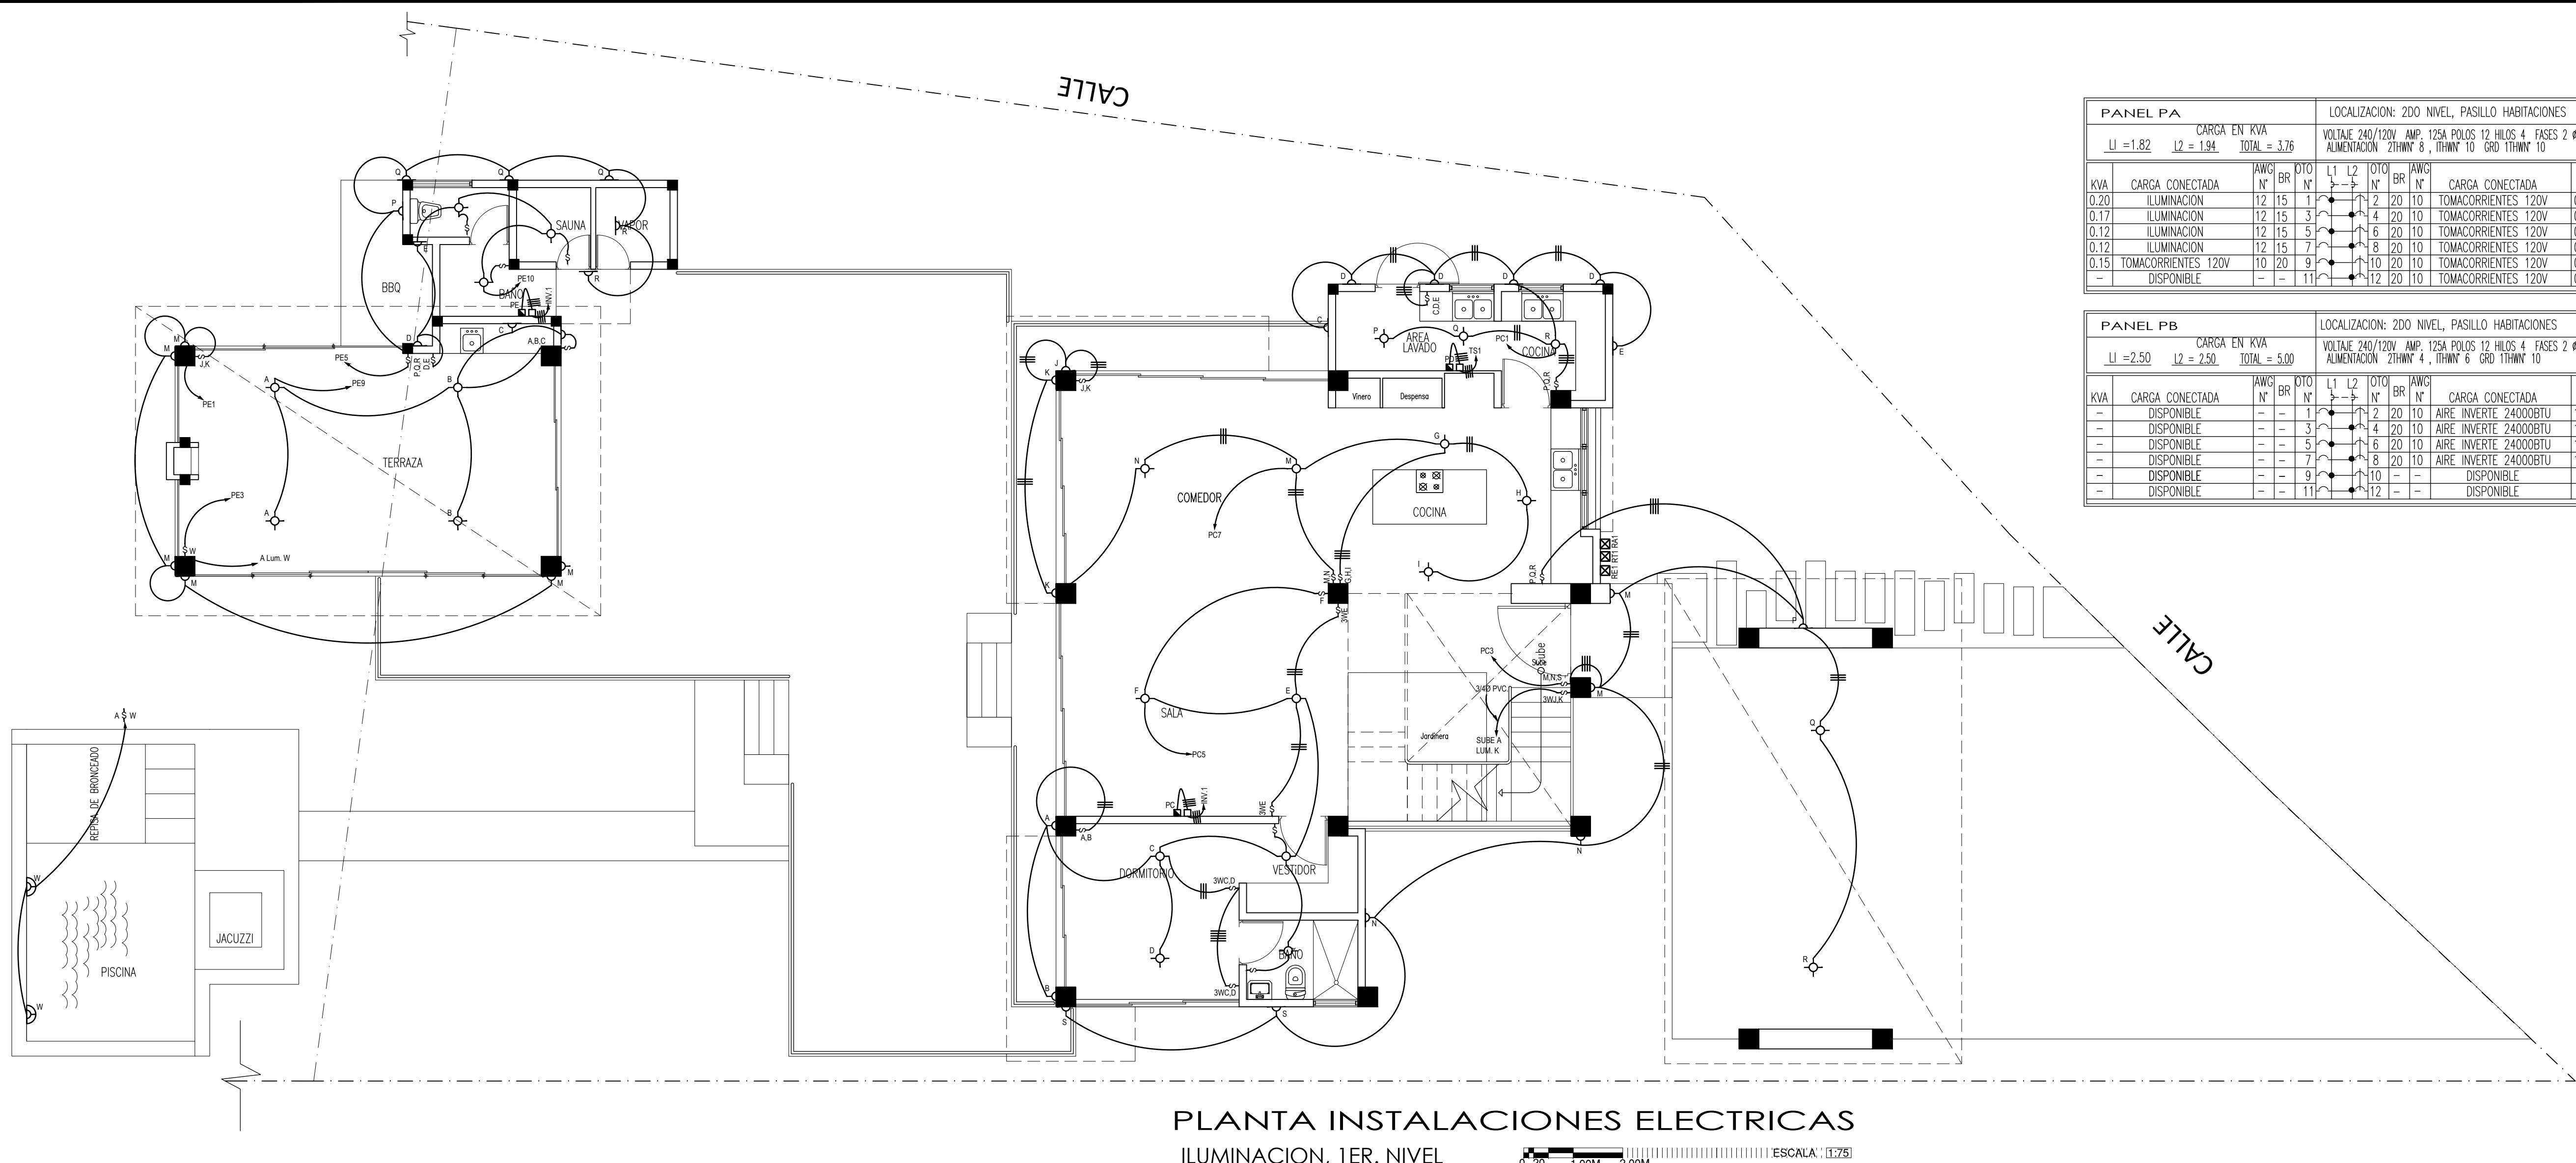

FACTOR DE USO		
PANEL		
PA	3.76 X 0.45	= 1.6920
PB	5.00 X 0.45	= 2.2500
PC	2.19 X 0.45	= 0.9855
PD	6.60 X 0.45	= 2.9700
PE	4.77 X 0.45	= 2.1465
<hr/> 10.0440 KVA		
10.0440 KVA < 14.5 KVA ENTONCES NO SE NECESA TRANSFORMADOR		
BALANCE DE CARGA		
PANEL	SUB TOTAL L1 N° KVA	SUB TOTAL L2 KVA
PA	1.82	1.94
PB	2.50	2.50
PC	1.17	1.02
PD	3.05	3.55
PE	2.47	2.30
<hr/> TOTAL L1=11.01KVA TOTAL L2=11.31KVA TOTAL=22.32 KVA		
TOTAL CARGA CONECTADA 22.32 KVA		
CORRIENTE TOTAL DEMANDADA 93.00AMP.		

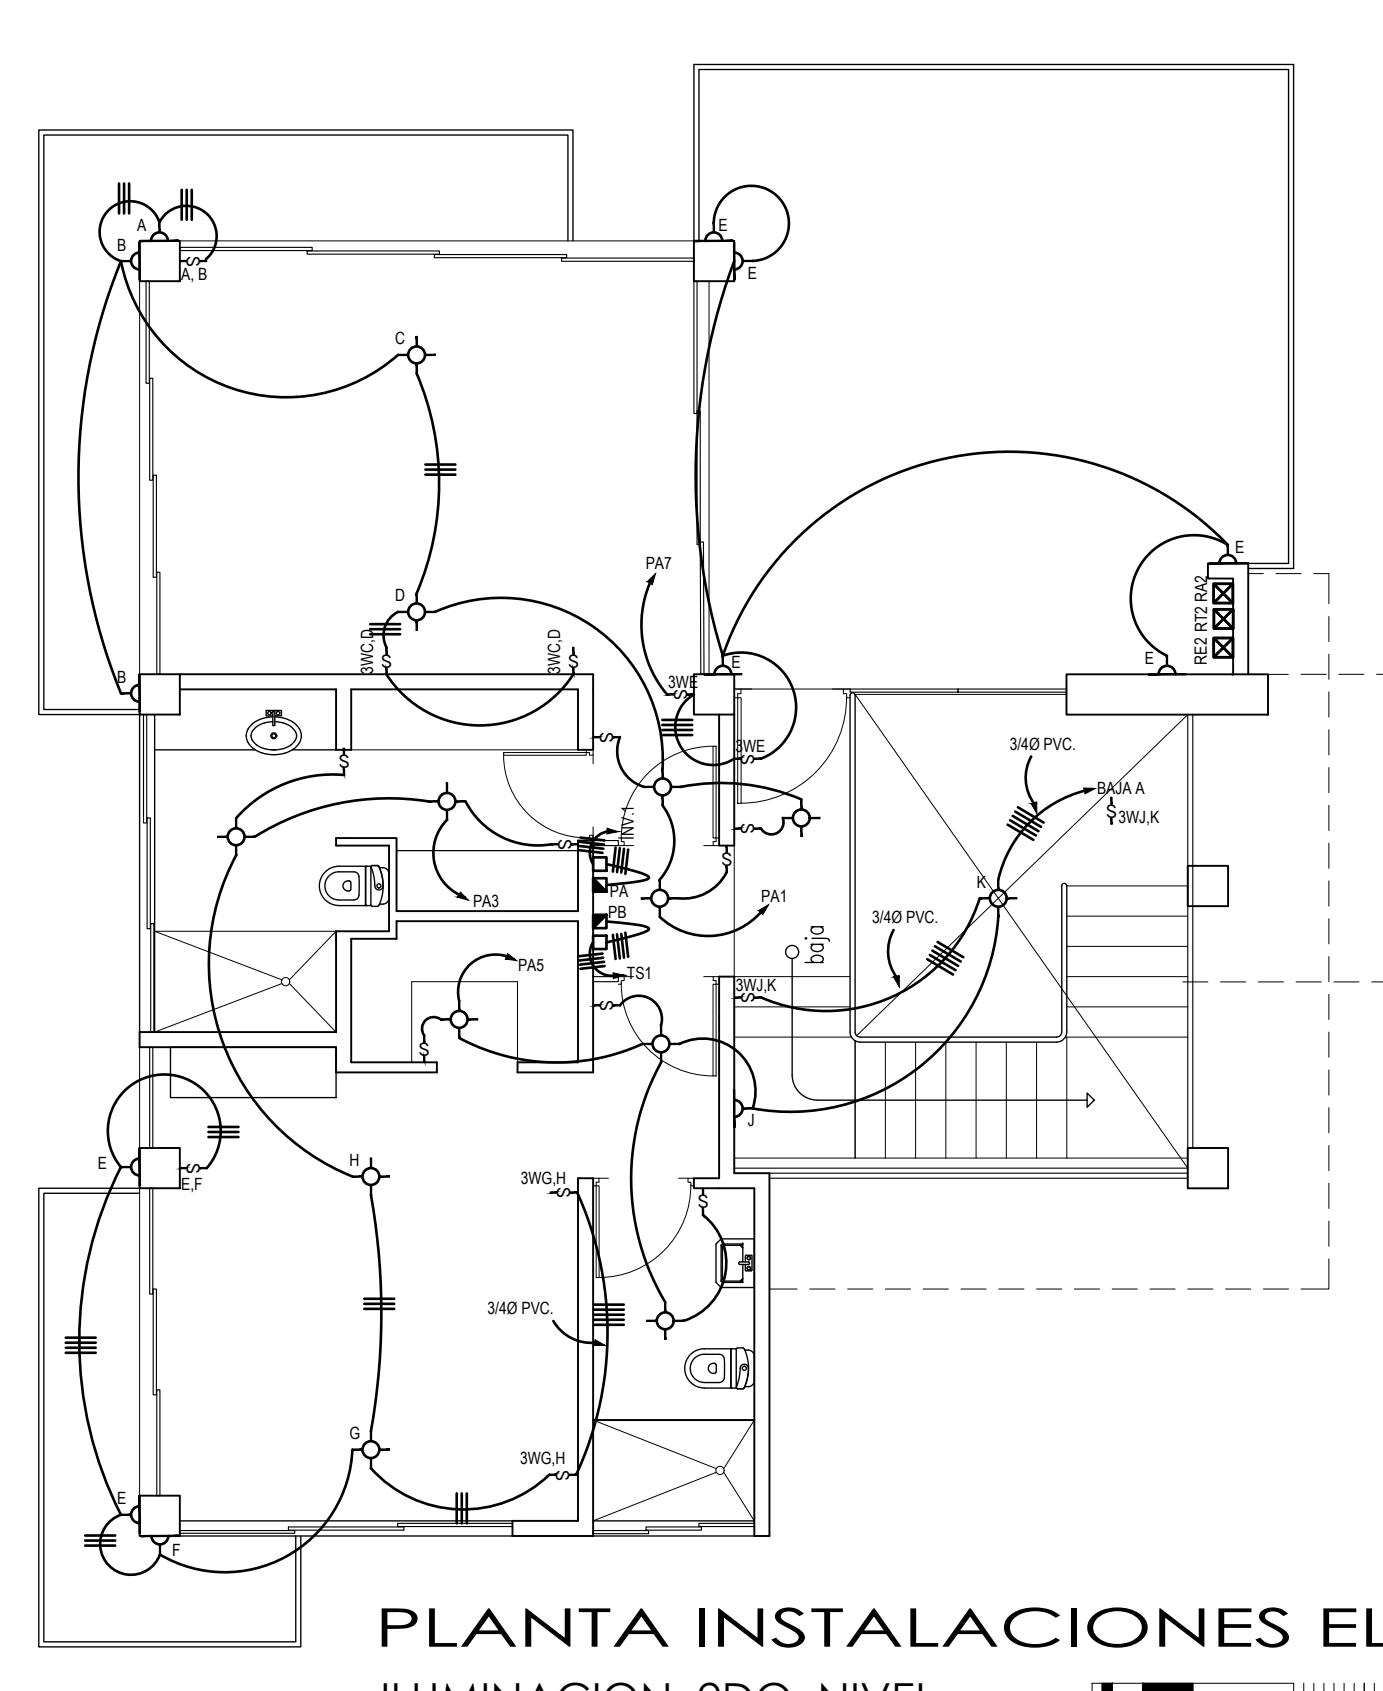


PANEL PA		LOCALIZACION: 2DO NIVEL, PASILLO HABITACIONES										
LI = 1.82	L2 = 1.94	CARGA EN KVA TOTAL = 3.76										
KVA	CARGA CONECTADA	AWG N°	BR	OT	N°	L1	L2	OTO	BR	AWG N°	CARGA CONECTADA	KVA
0.20	ILUMINACION	12	15	1		2	20	10	TOMACORRIENTES	120V	0.60	
0.17	ILUMINACION	12	15	3		4	20	10	TOMACORRIENTES	120V	0.60	
0.12	ILUMINACION	12	15	5		6	20	10	TOMACORRIENTES	120V	0.60	
0.12	ILUMINACION	12	15	7		8	20	10	TOMACORRIENTES	120V	0.60	
0.15	TOMACORRIENTES 120V	10	20	9		10	20	10	TOMACORRIENTES	120V	0.15	
-	DISPONIBLE	-	-	11		12	20	10	TOMACORRIENTES	120V	0.45	
-	DISPONIBLE	-	-	11		12	20	10	TOMACORRIENTES	120V	0.45	

PANEL PB		LOCALIZACION: 2DO NIVEL, PASILLO HABITACIONES										
LI = 2.50	L2 = 2.50	CARGA EN KVA TOTAL = 5.00										
KVA	CARGA CONECTADA	AWG N°	BR	OT	N°	L1	L2	OTO	BR	AWG N°	CARGA CONECTADA	KVA
-	DISPONIBLE	-	-	1		2	20	10	AIRE INVERTE	24000BTU	1.25	
-	DISPONIBLE	-	-	3		4	20	10	AIRE INVERTE	24000BTU	1.25	
-	DISPONIBLE	-	-	5		6	20	10	AIRE INVERTE	24000BTU	1.25	
-	DISPONIBLE	-	-	7		8	20	10	AIRE INVERTE	24000BTU	1.25	
-	DISPONIBLE	-	-	9		10	-	-	DISPONIBLE	-	-	
-	DISPONIBLE	-	-	11		12	-	-	DISPONIBLE	-	-	


PANEL PD		LOCALIZACION: 1ER NIVEL, AREA DE LAVADO EDIF. 1 DER.										
LI = 3.05	L2 = 3.55	CARGA EN KVA TOTAL = 6.60										
KVA	CARGA CONECTADA	AWG N°	BR	OT	N°	L1	L2	OTO	BR	AWG N°	CARGA CONECTADA	KVA
1.50	TOMACORRIENTES 120V	10	20	1		2	20	10	AIRE INVERTE	24000BTU	1.25	
1.50	TOMACORRIENTES 120V	10	20	3		4	20	10	AIRE INVERTE	24000BTU	1.25	
0.80	LAVADORA	10	20	5		6	-	-	DISPONIBLE	-	-	
0.80	LAVADORA	10	20	7		8	-	-	DISPONIBLE	-	-	
0.50	NEVERA	10	20	9		10	-	-	DISPONIBLE	-	-	
1.00	PLANCHA	10	20	11		12	-	-	DISPONIBLE	-	-	

PANEL PE		LOCALIZACION: 1ER NIVEL,PESILLO LOCAL IZQ.										
LI = 2.47	L2 = 2.30	CARGA EN KVA TOTAL = 4.77										
KVA	CARGA CONECTADA	AWG N°	BR	OT	N°	L1	L2	OTO	BR	AWG N°	CARGA CONECTADA	KVA
0.15	ILUMINACION	12	15	1		2	20	10	BOMBA CISTERNA	0.40		
1.00	ILUMINACION	12	16	3		4	20	10	BOMBA CISTERNA	0.49		
0.15	ILUMINACION	12	15	5		6	20	10	TOMACORRIENTES	120V	1.50	
0.15	ILUMINACION	12	15	9		8	20	10	TOMACORRIENTES	120V	0.75	
-	DISPONIBLE	-	-	7		10	20	10	TOMACORRIENTES	120V	0.12	
-	DISPONIBLE	-	-	11		12	20	10	TOMACORRIENTES	120V	0.15	
-	DISPONIBLE	-	-	13		14	-	-	DISPONIBLE	-	-	
-	DISPONIBLE	-	-	15		16	-	-	DISPONIBLE	-	-	

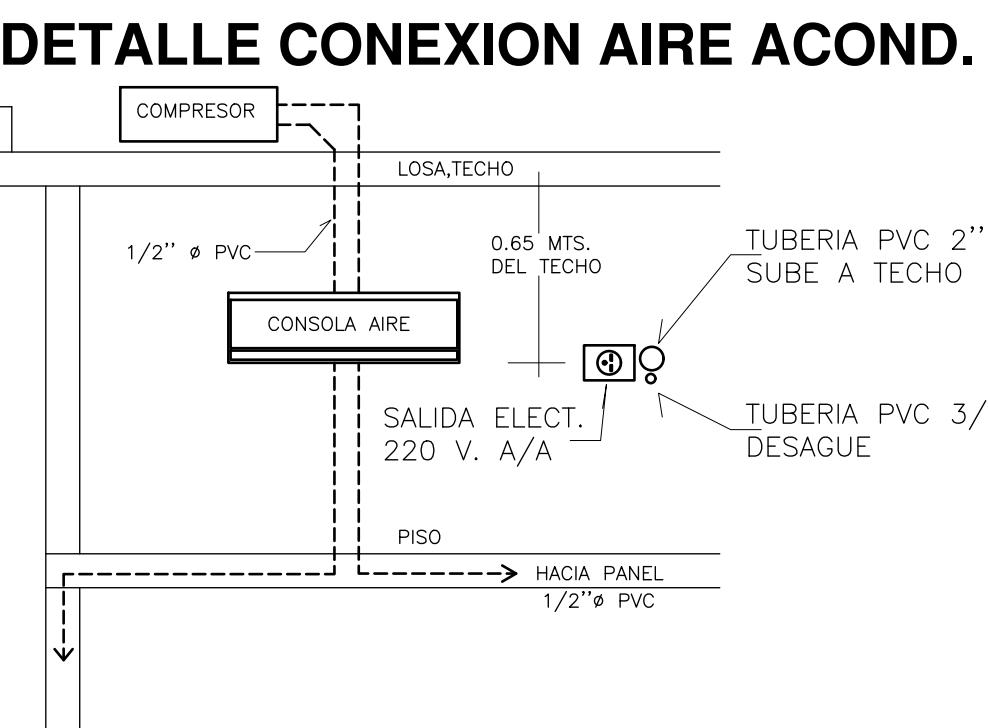

SIMB.	DESCRIPCION	SIMB.	DESCRIPCION
○	LUMINARIA CENTRAL LED 24W	◀	SALIDA DE TELEFONO 0.40M
▷	LUMINARIA PARED LED 24W	—C	SALIDA DE ANTENA TV 0.40M
\$	INTERRUPTOR SENCILLO 1.20M	—	TUBERIA PVC ELEC 1/2" POR TECHO
\$..	INTERRUPTOR DOBLE 1.20M	—	TUBERIA PVC ELEC 1/2" POR PISO
\$... _{AC}	INTERRUPTOR TRIPLE 1.20M	—	TUBERIA PVC ELEC 1/2" POR TECHO PARED
—	TOMACORRIENTE 120 V 0.40M	—	TUBERIA PVC ELEC 3/4" POR PISO
—	TOMACORRIENTE 120 V 1.20M	—	PULSADOR DETIMBRE 1.40M
—	TOMACORRIENTE 120 V 1.60M	—	CAMPANA DE TIMBRE 1.80M
—	SALIDA 240V 0.40M	—	PANEL DE DISTRIBUCION 1.60
—	CONTADOR CON MAIN BREAKER 1.80M	—	REGISTRO TELEFONICO 0.40M
*****	TRANSFORMADOR PROPUESTO	—	REGISTRO DE ANTENAS 0.40M
—	VARILLA DE TIERRA	—	REGISTRO ELECTRICO 0.40M
CUT OUT	PARARRAYOS	—	TRANSFER SWITCH 1.40M
—	TRANSFER SWITCH 1.40M	—	INVERSORES 1.60M
—	INTERRUPTOR THREE WAY 1.20M	—	PLANTA DE EMERGENCIA 0.40M
—	INTERRUPTOR FOUR WAY 1.20M	—	LUMINARIAS LED EN QUIRÓFANO 90W
—	DOS LAMPAR		


DIAGRAMA DE UNIFILAR DE EDIFICIO 1

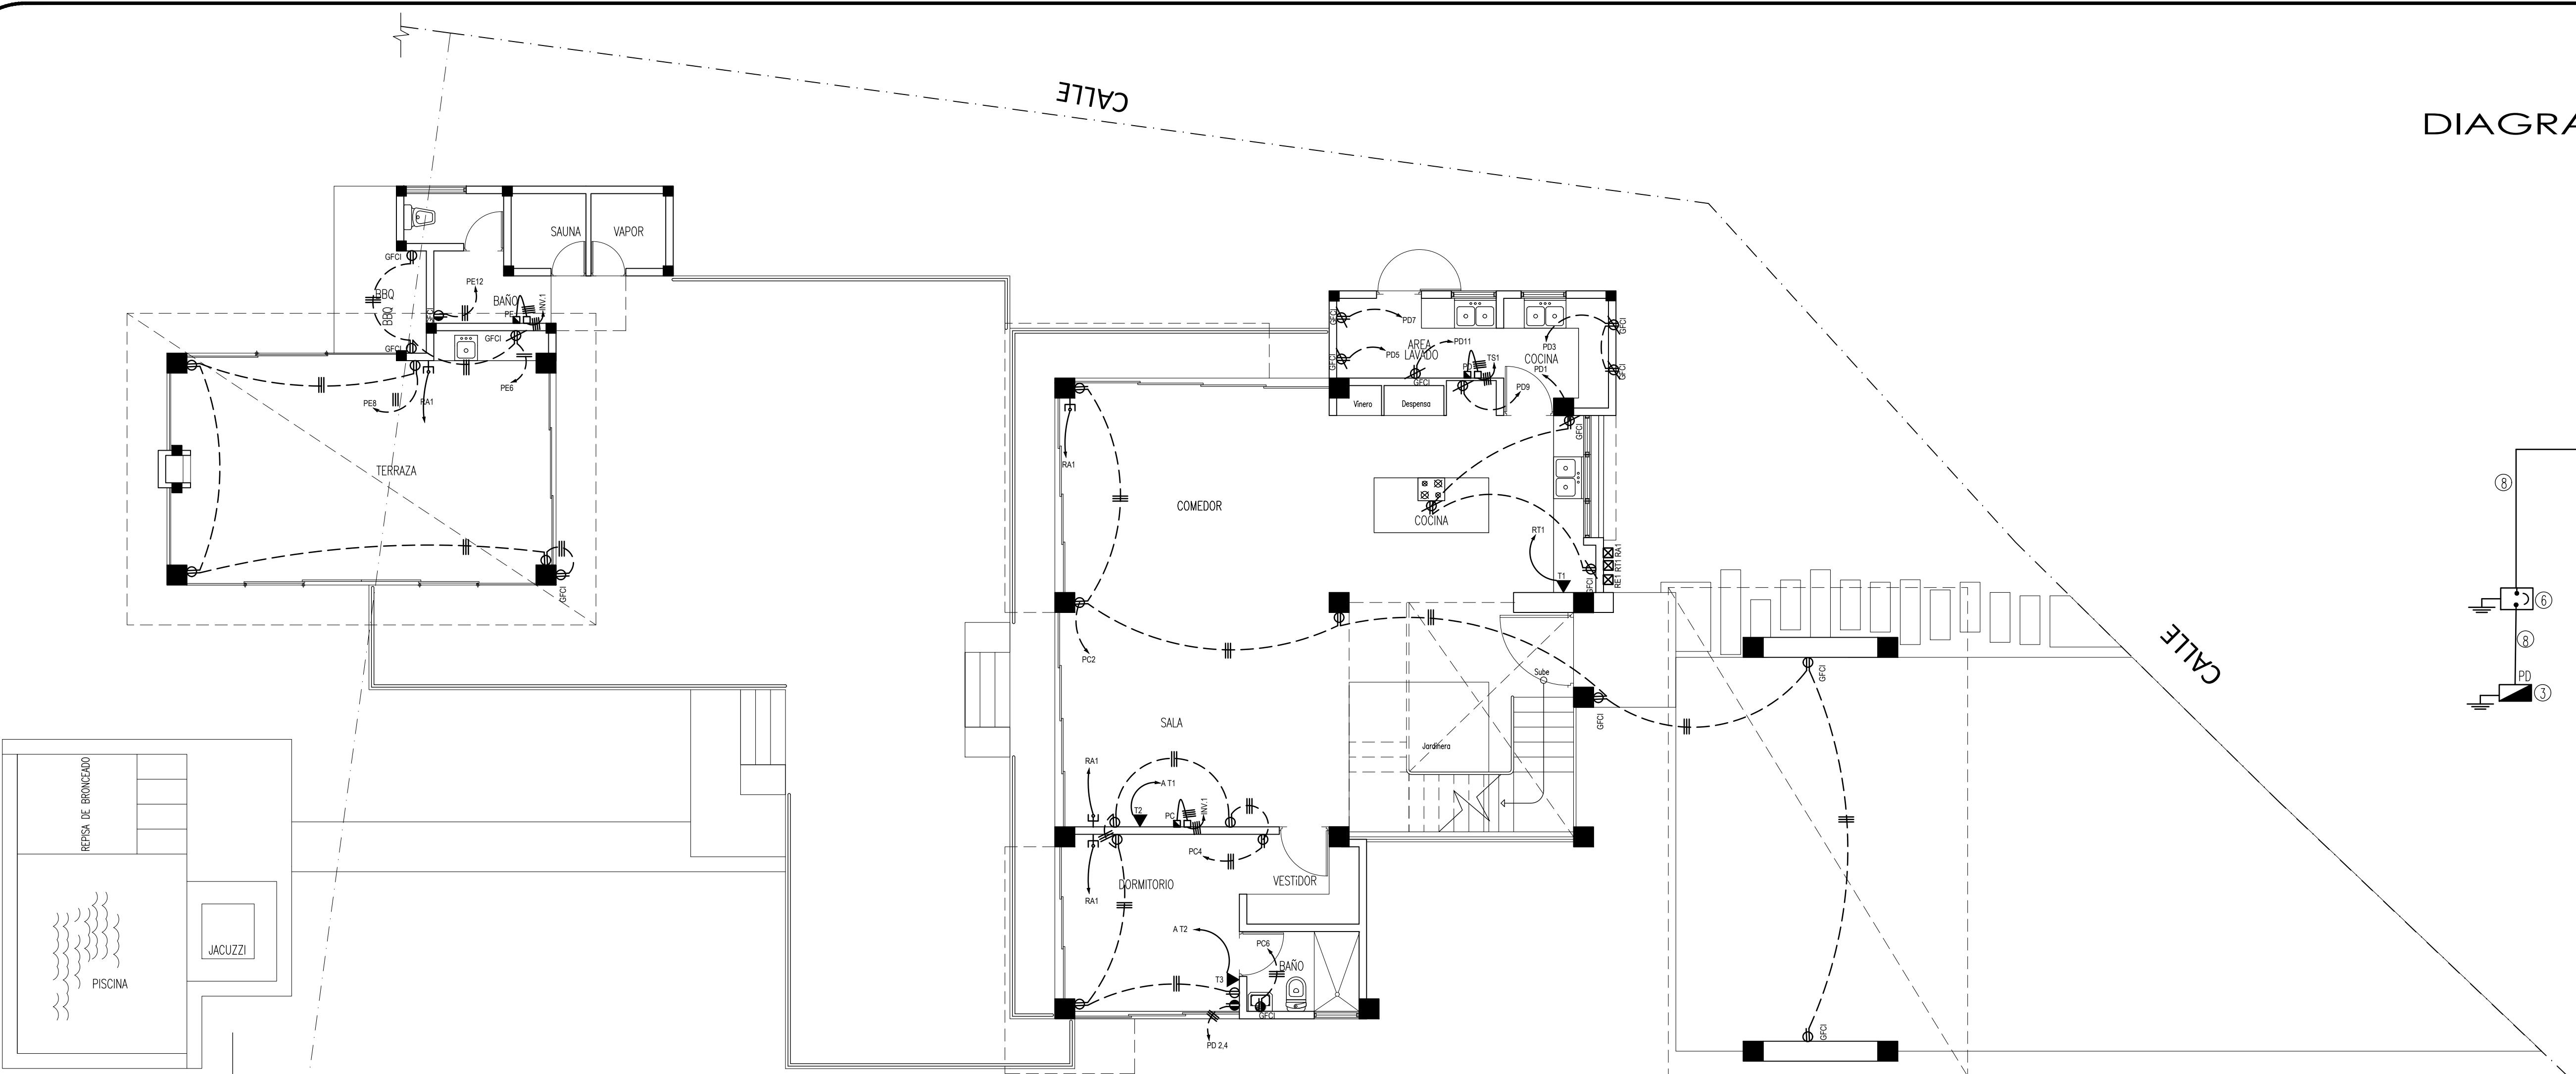

CÓDIGO DE COLORES


VERDE	TIERRA
NEGRO	NEUTRO
ROJO	LÍNEA L1
AMARILLO	LÍNEA L2

DIAGRAMA DE ANTENA

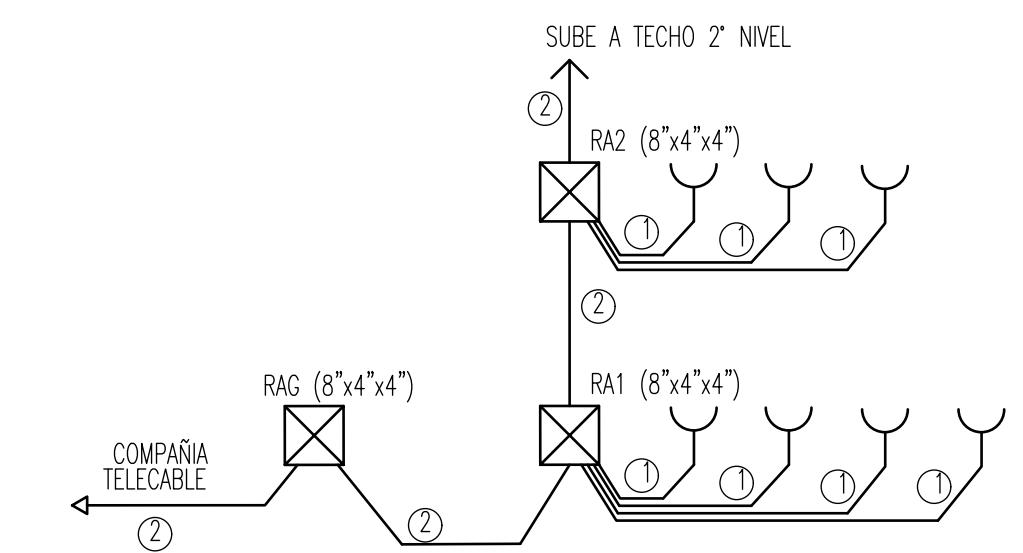

PLANTA INSTALACIONES ELECTRICAS

T.C. TELEFONOS Y CABLE T.V., 1ER. NIVEL ESCALA: 1:75

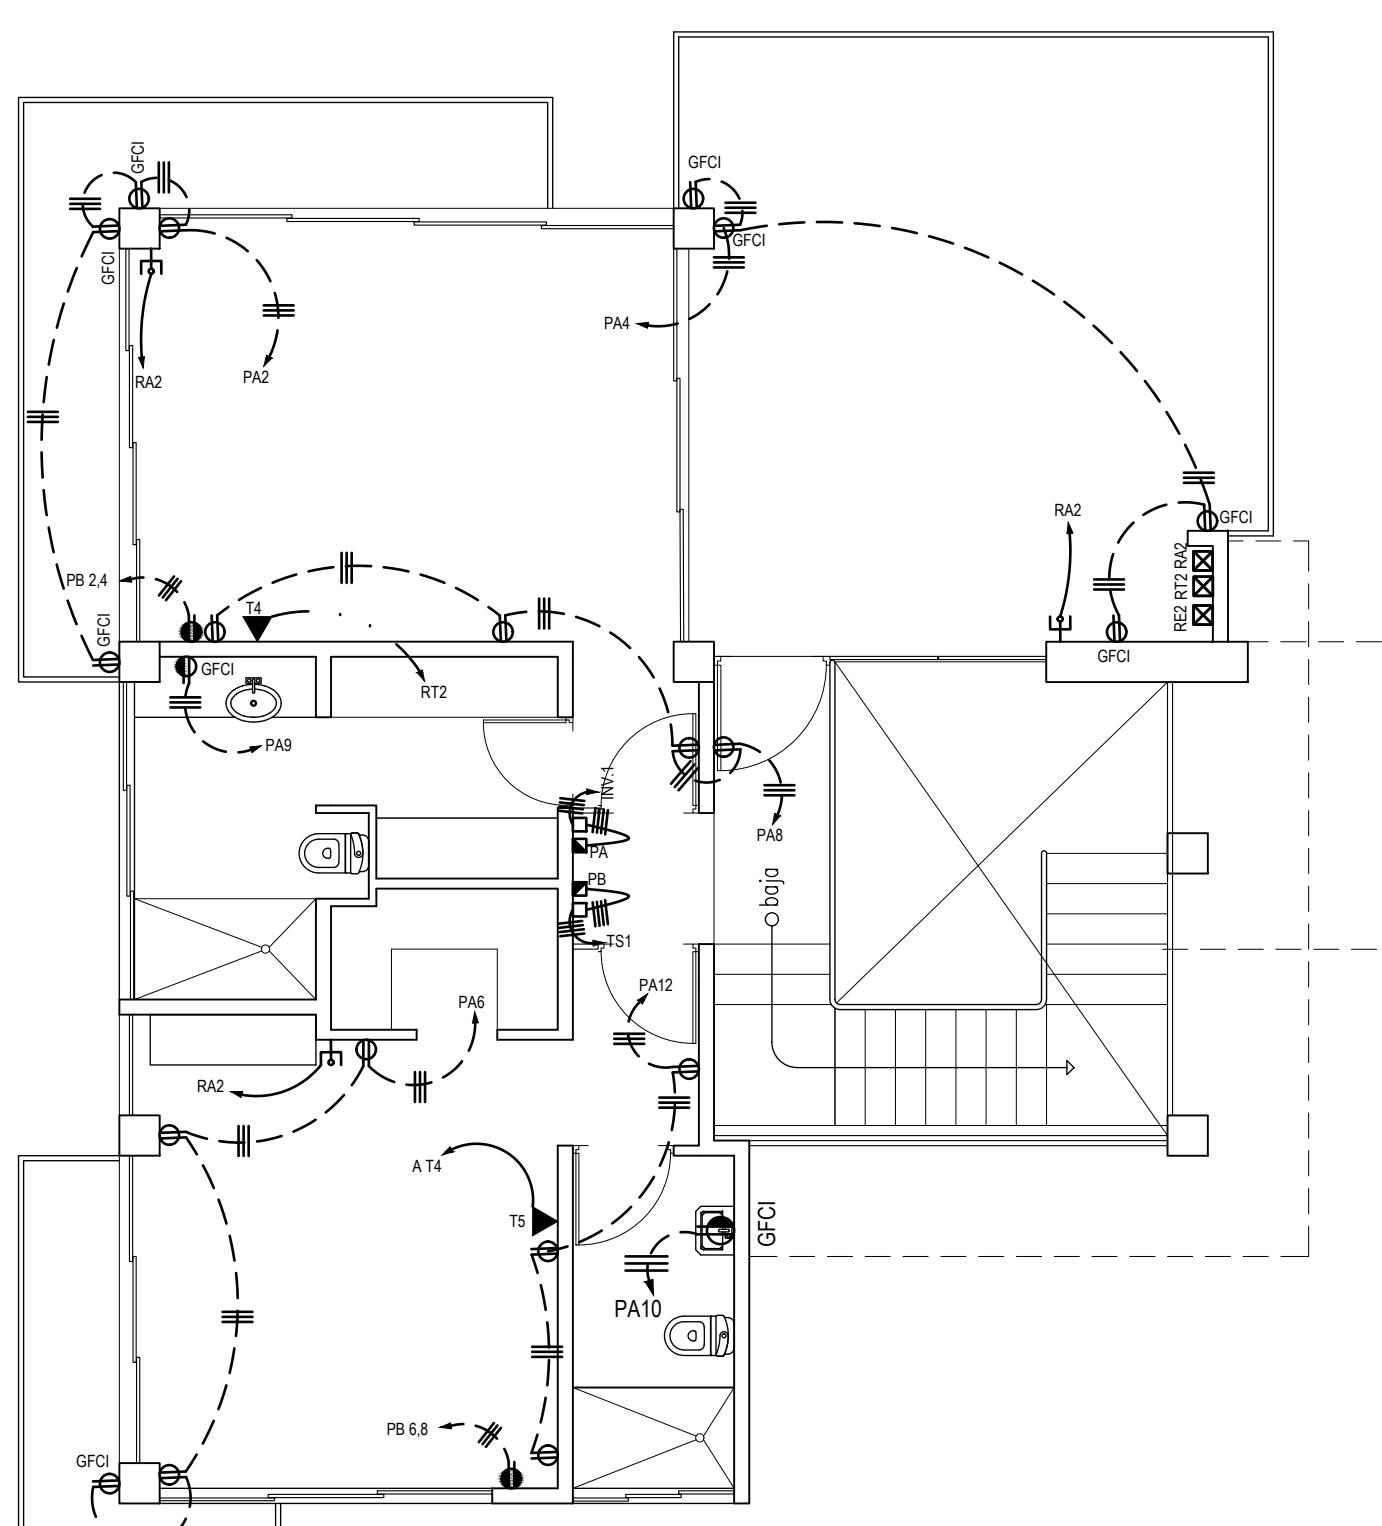


PLANTA INSTALACIONES ELECTRICAS

T.C. TELEFONOS Y CABLE T.V., 2DO. NIVEL ESCALA: 1:75

- (3) PANEL DE DISTRIBUCIÓN ELÉCTRICA
- (4) VARILLA DE TIERRA 5/8" X 8' GRD 1' CU N° 6
- (5) MAIN BREAKER 40A/2
- (6) MAIN BREAKER 60A/2
- (7) 2THW#2 , 1THW#10 GRD 1THW N°10 TUB. PVC ELECT. 1"
- (8) 2THW#2 , 1THW#4 GRD 1THW N°8 TUB. PVC ELECT. 2"
- (9) TS (TRANSFER SWITCH) BARRAS(240/120V,100A/2,2φ)
- (10) MC (MODULO DE CONTADORES) BARRAS(240/120V,200A/2,2φ)

DIAGRAMA TELEFONICO

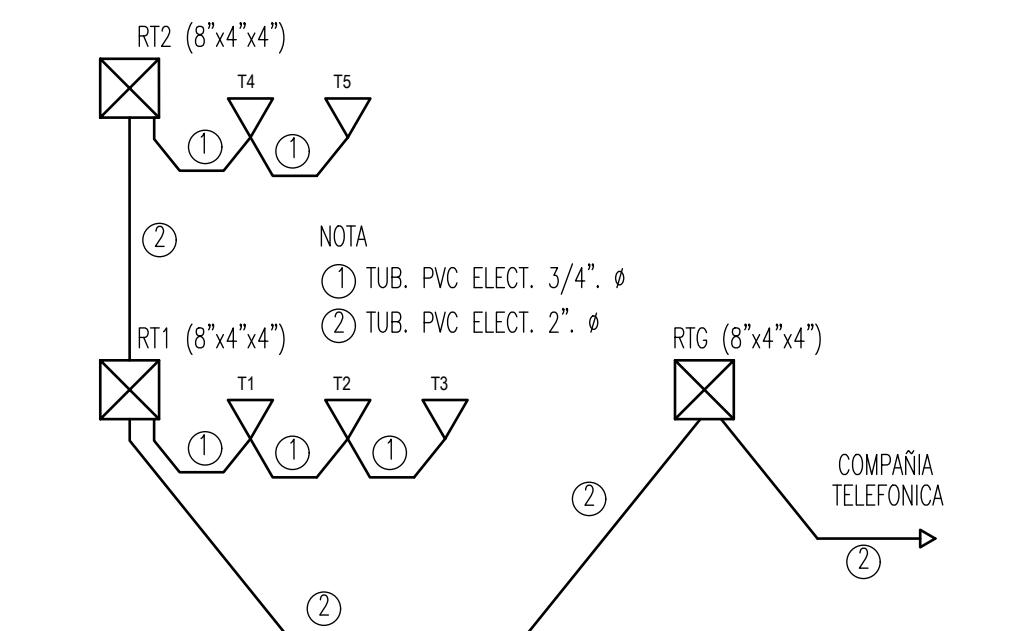

Villa Beato Reyes

LOCALIZACION: GUAIQUI, LA VEGA
PROPIETARIOS:

JOSE LUIS BEATO PEÑA CED. 402-2763926-3 FIRMA
JOSELYN ANTONELIA REYES A. CED. 402-2737538-9 FIRMA

DISEÑO ARQUITECTONICO: SHERYL LOPEZ R. CODA :46298

DISEÑO SANITARIO: INC. FRANK FELIZ LOPEZ CODA :19796

DISEÑO ESTRUCT: HIPOLITO MORONTA LLONG CODA : 4166


DISEÑO ELECTRICO: HIPOLITO MORONTA LLONG CODA : 4166

DIBUJO : D 1 B U 1 0
AVENIDA AMERICA #4 LA VEGA
CODA :13,638

ESCALA : 1:75


FECHA: 1 - 9 - 2021



HOJA # 10/23

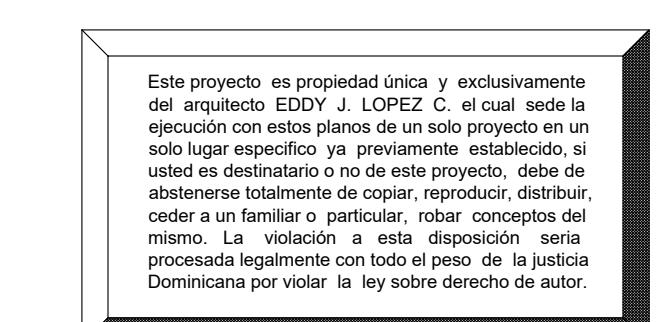

ARQ. EDDY LOPEZ C.

809-399 8344

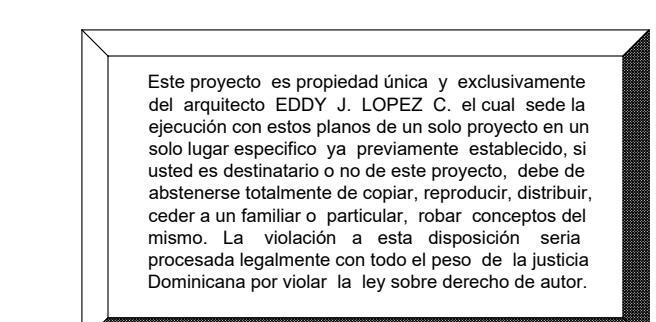

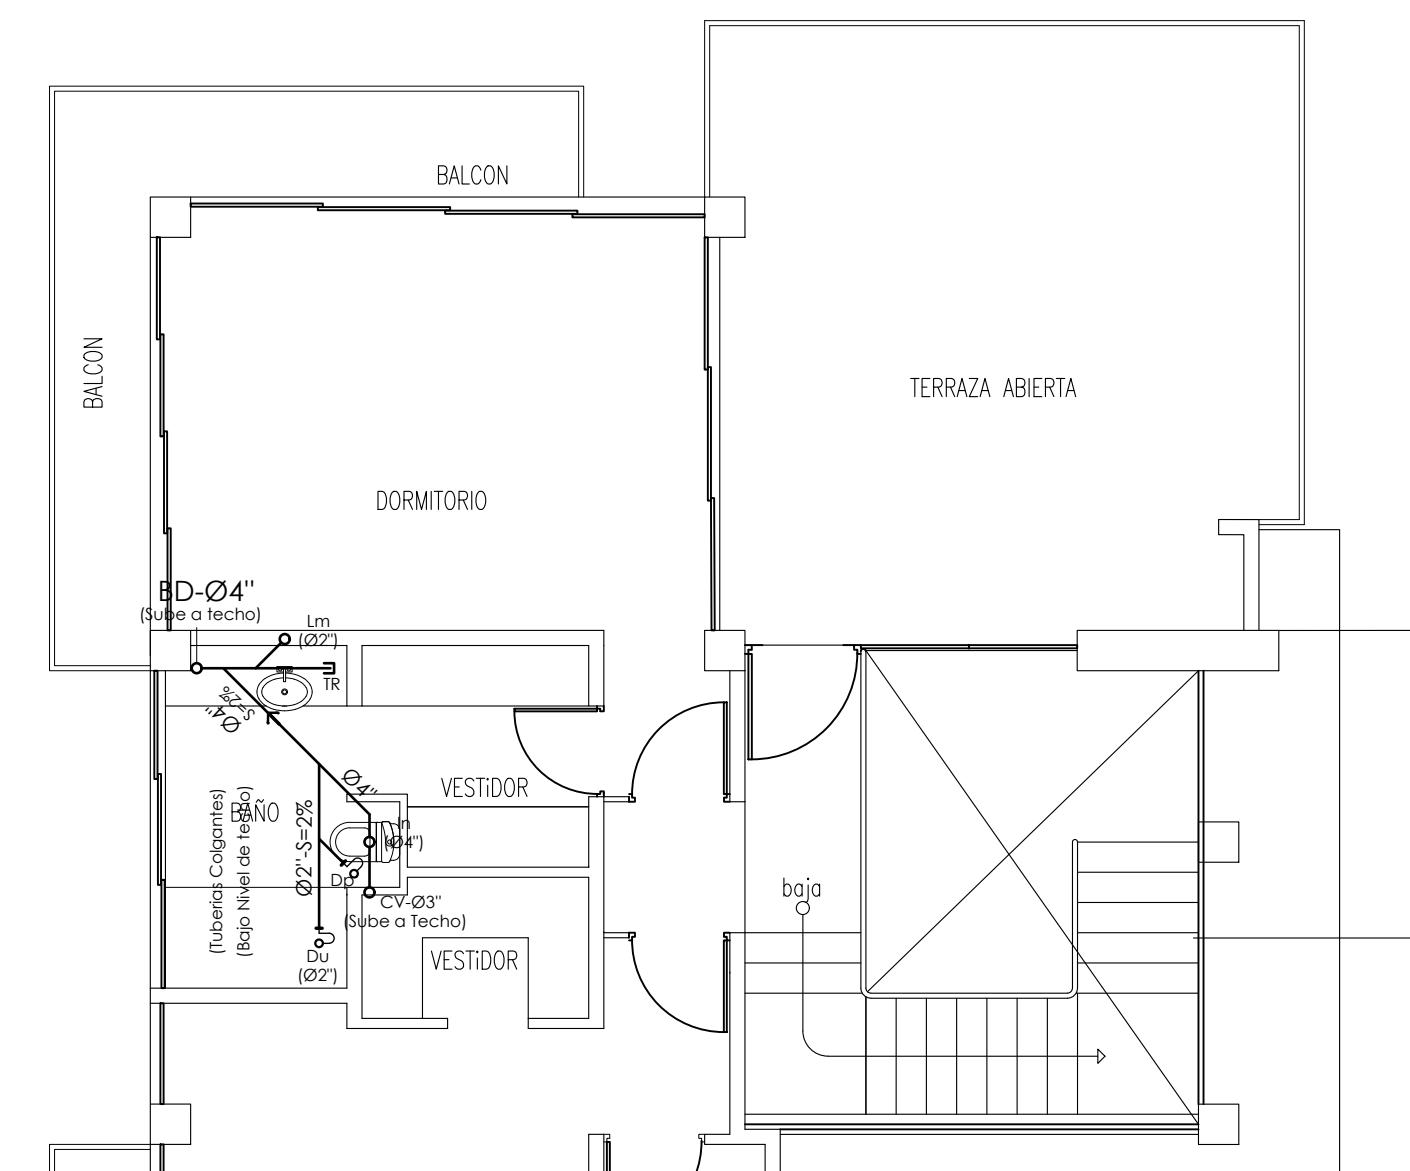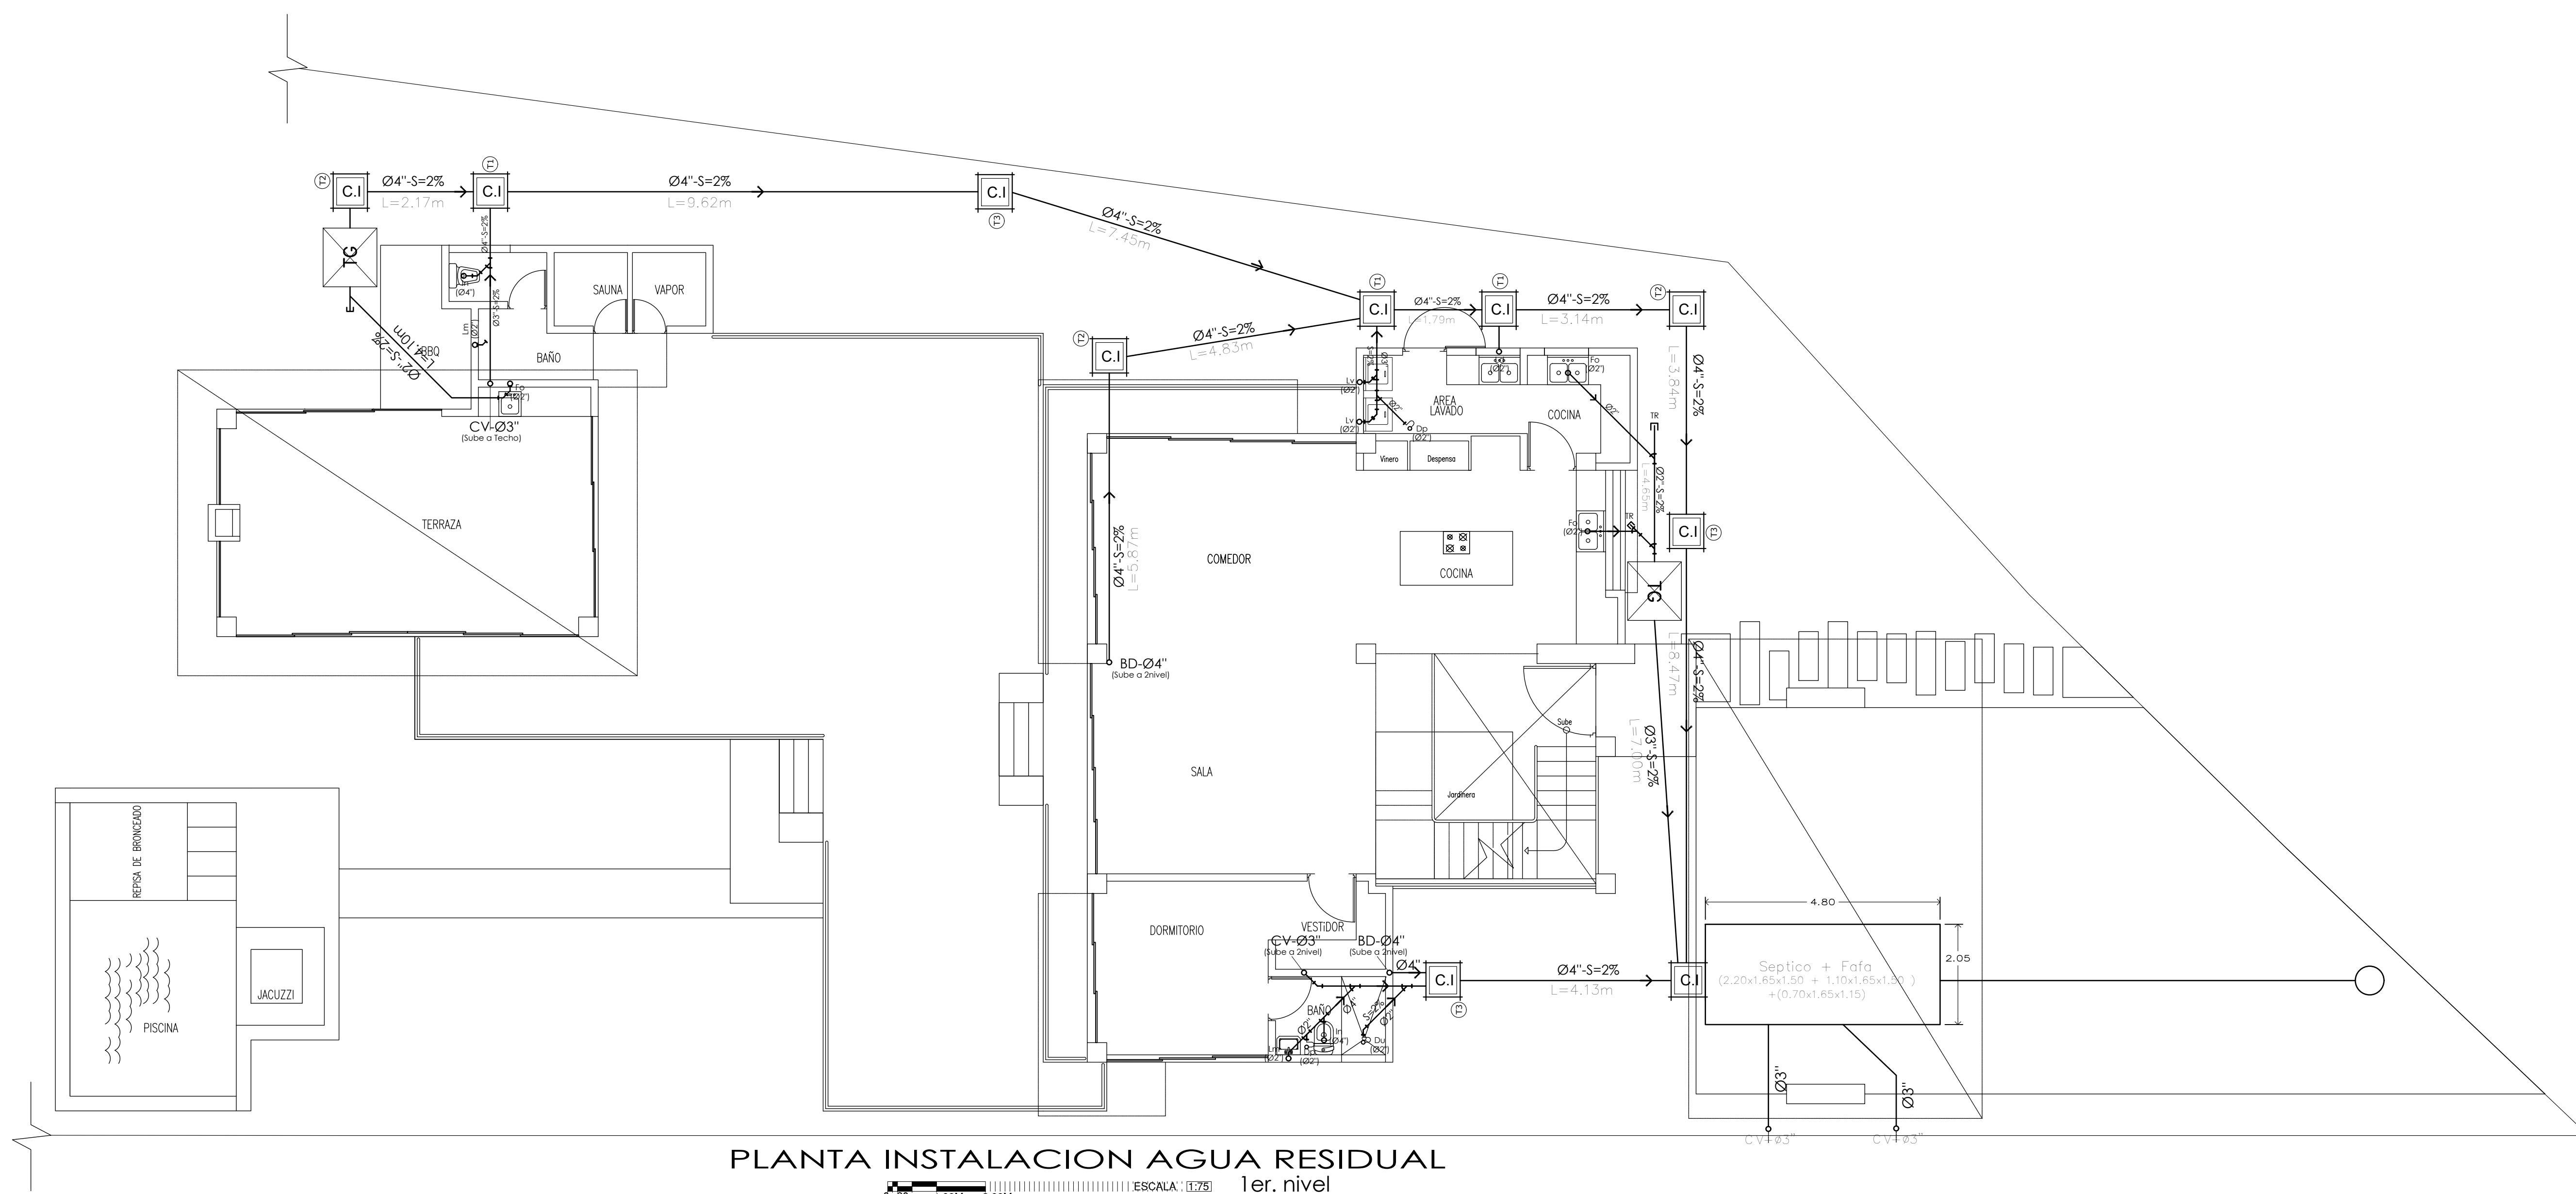

PLANTA INSTALACION AGUA RESIDUAL
2do. nivel
ESCALA: 1:75

Este proyecto es propiedad única y exclusivamente del arquitecto EDDY J. LOPEZ C. el cual sede la ejecución con estos planos de un solo proyecto en un solo lugar específico ya previamente establecido, si usted es destinatario o no de este proyecto, debe de abstenerse totalmente de copiar, reproducir, distribuir, ceder a un familiar o particular, robar conceptos del mismo. La violación a esta disposición sería procesada legalmente con todo el peso de la justicia Dominicana por violar la ley sobre derecho de autor.



ARQ. EDDY LOPEZ C.
809-399 8344

Villa Beato Reyes
LOCALIZACION: GUAIGUI, LA VEGA
PROPIETARIOS:

JOSE LUIS BEATO PEÑA
CED. 402-2763926-3
FIRMA
JOSELYN ANTONELIA REYES A.
CED. 402-2737538-9
FIRMA

DISEÑO ARQUITECTONICO: SHERYL LOPEZ R. CODIA: 46288



DISEÑO SANITARIO: ING. FRANK FELIZ LOPEZ CODIA: 19796

DISEÑO ESTRUCT.: HIPOLITO MORON LILONG CODIA: 4166

DISEÑO ELECTRICO: HIPOLITO MORON LILONG CODIA: 4166





DIBUJO: DIBUJO: EL ARQUITECTURA AVENIDA LIBERTAD #4 LA VEGA 809-573-7056 809-399-8344
CODIA: 13638

ESCALA INDICADA
HOJA # 11/23

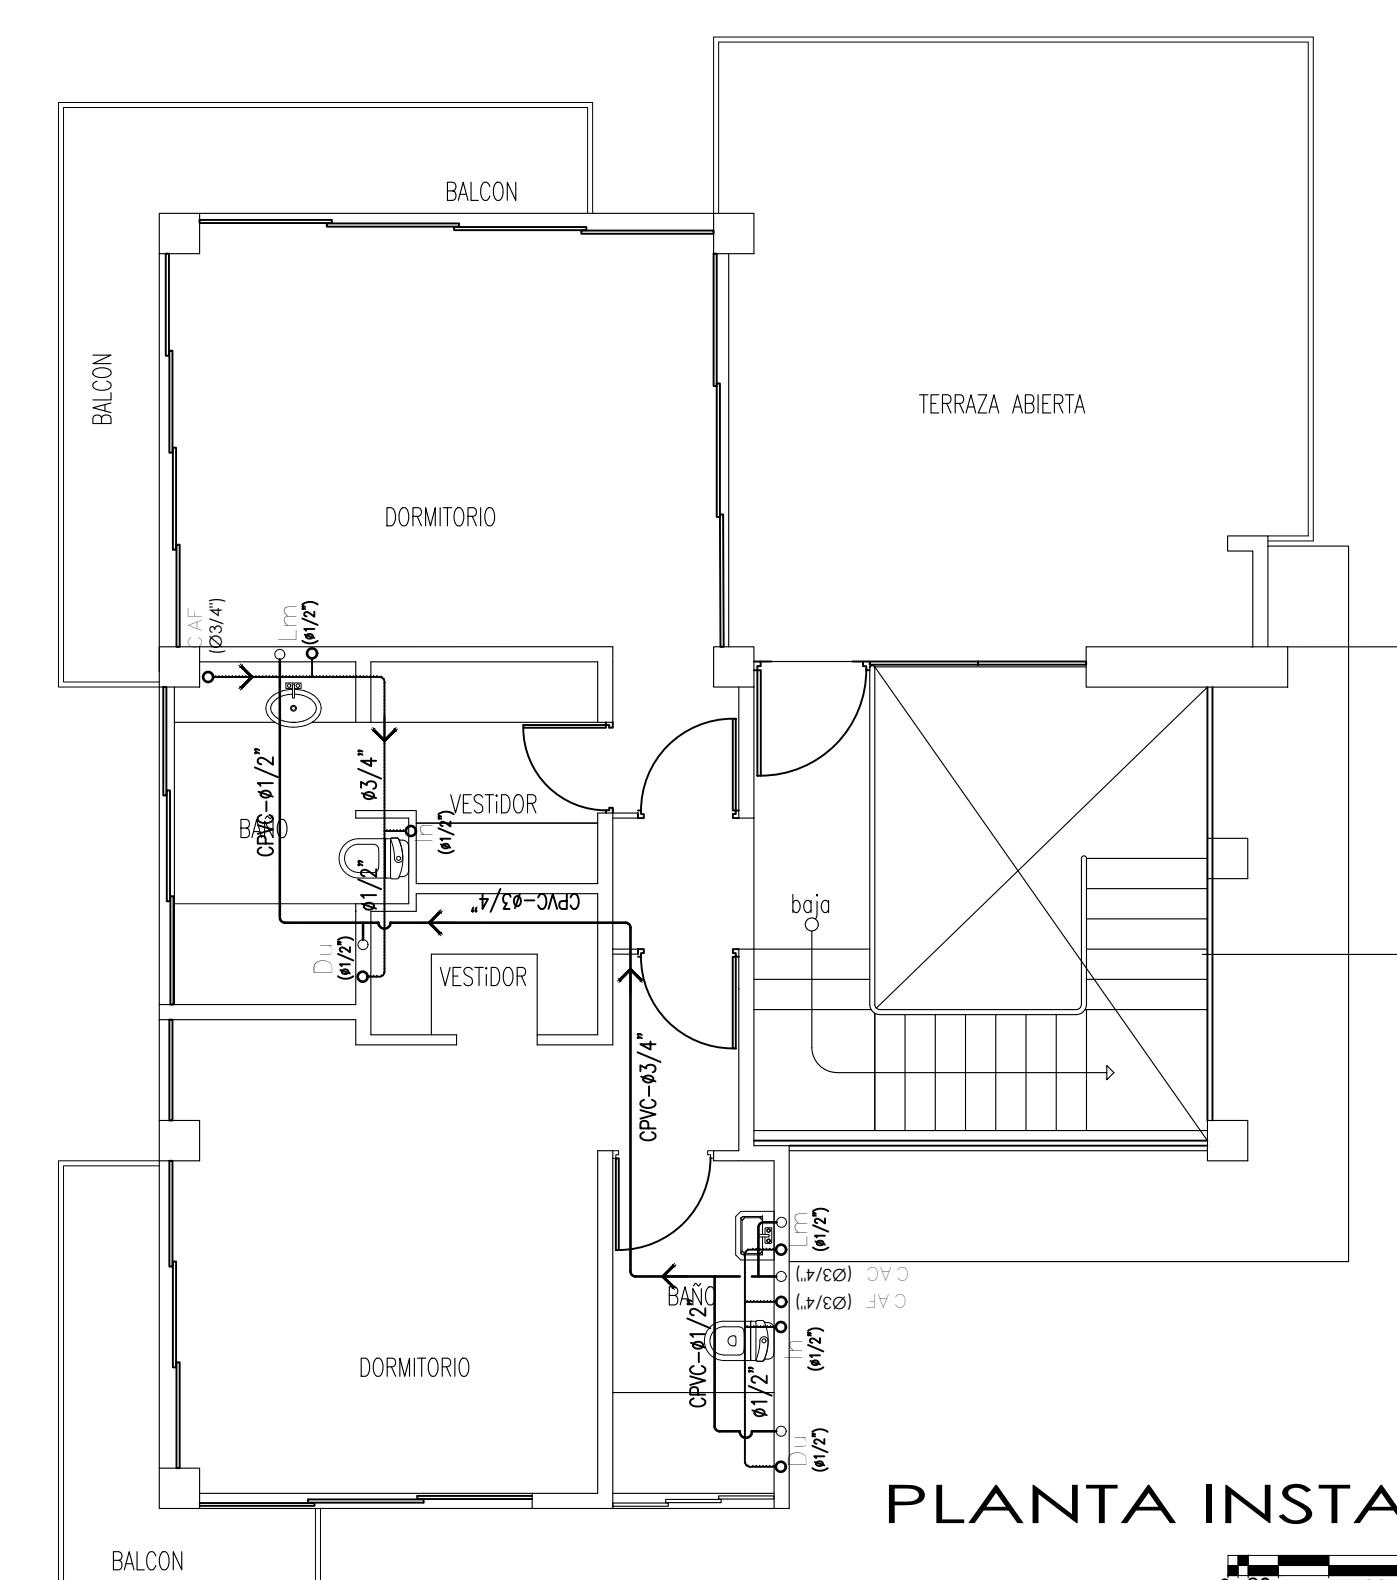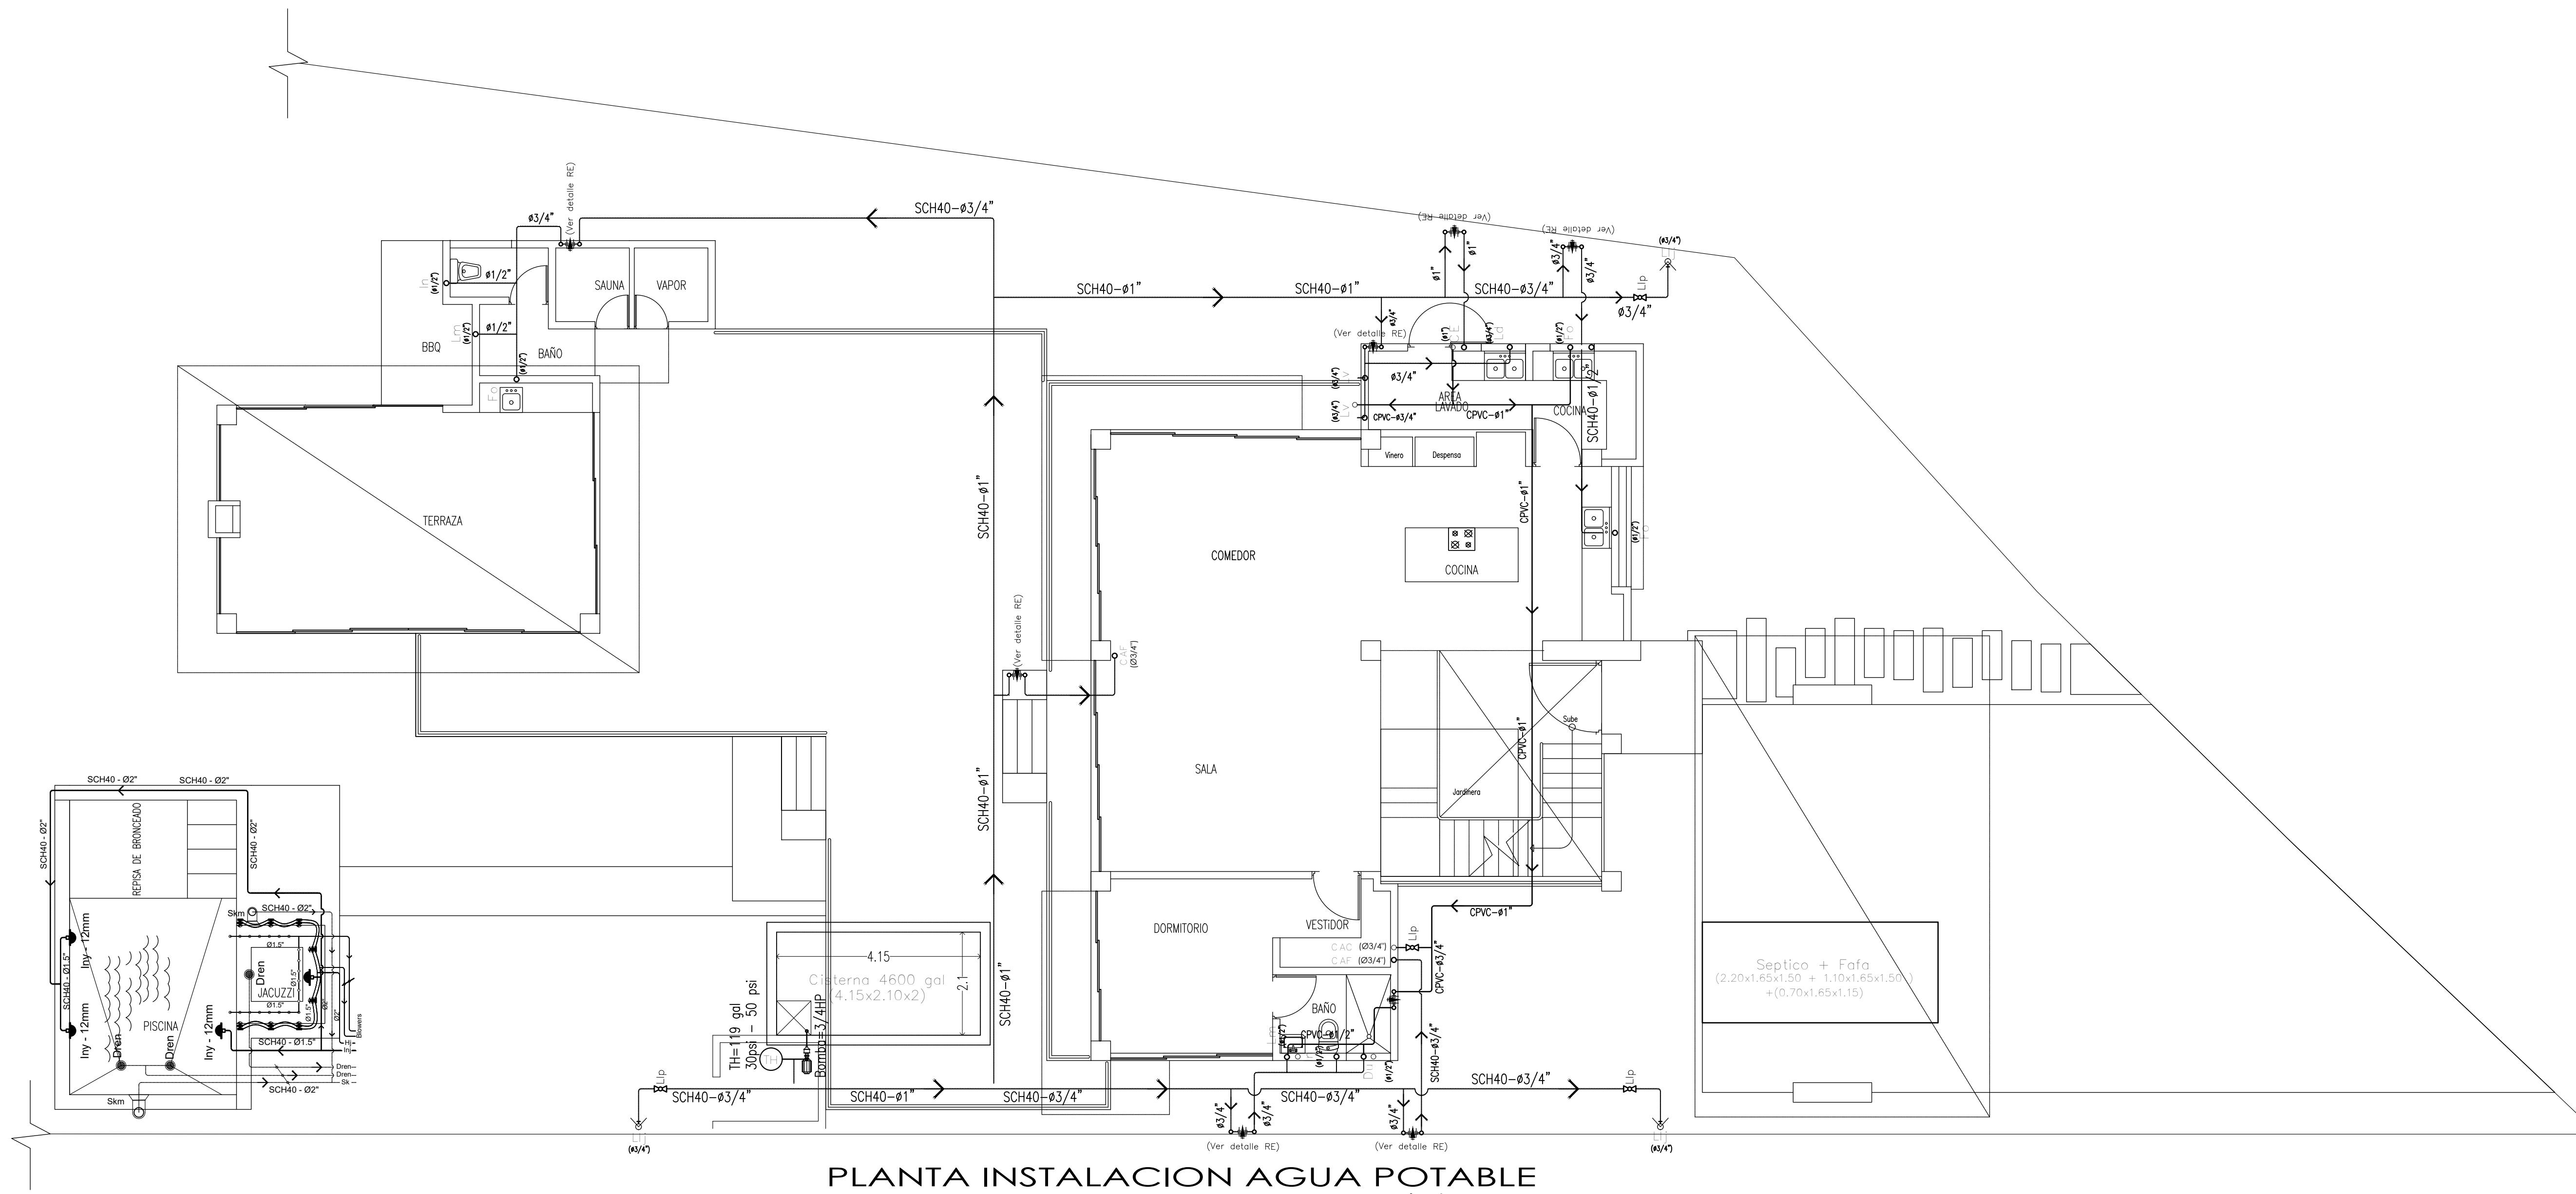



Este proyecto es propiedad única y exclusivamente del arquitecto EDDY J. LOPEZ C. el cual sede la ejecución con estos planos de un solo proyecto en un solo lugar específico ya previamente establecido, si usted es destinatario o no de este proyecto, debe de abstenerse totalmente de copiar, reproducir, distribuir, ceder a un familiar o particular, robar conceptos del mismo. La violación a esta disposición sería procesada legalmente con todo el peso de la justicia Dominicana por violar la ley sobre derecho de autor.

Villa Beato Reyes	LOCALIZACION: GUAIGUI, LA VEGA
PROPIETARIOS:	
JOSE LUIS BEATO PEÑA CED. 402-2763926-3	FIRMA
JOSELYN ANTONELIA REYES A. CED. 402-2737538-9	FIRMA
DISEÑO ARQUITECTONICO: SHERYL LOPEZ R.	CODIA: 46288
DISEÑO SANITARIO: ING. FRANK FELIZ LOPEZ	CODIA: 19796
DISEÑO ESTRUCT.: HIPOLITO MORON LILONG	CODIA: 4166
DISEÑO ELECTRICO: HIPOLITO MORON LILONG	CODIA: 4166
RESPONSABLE DEL PROYECTO: ARQUITECTO: EDDY J. LOPEZ CODIA: 13.638	DIBUJO: EL ARQUITECTURA AVENIDA LIBERTAD #4 LA VEGA 809.573.7056 809.399.8344 FECHA: 1-9-2021
INDICADA	ESCALA
HOJA #	12/23

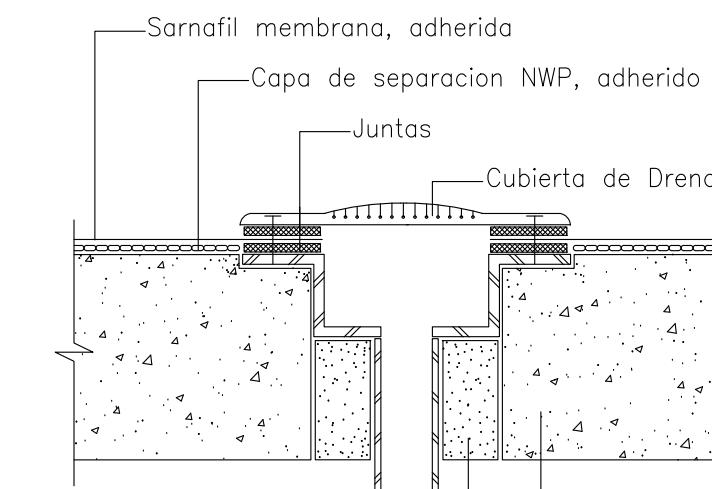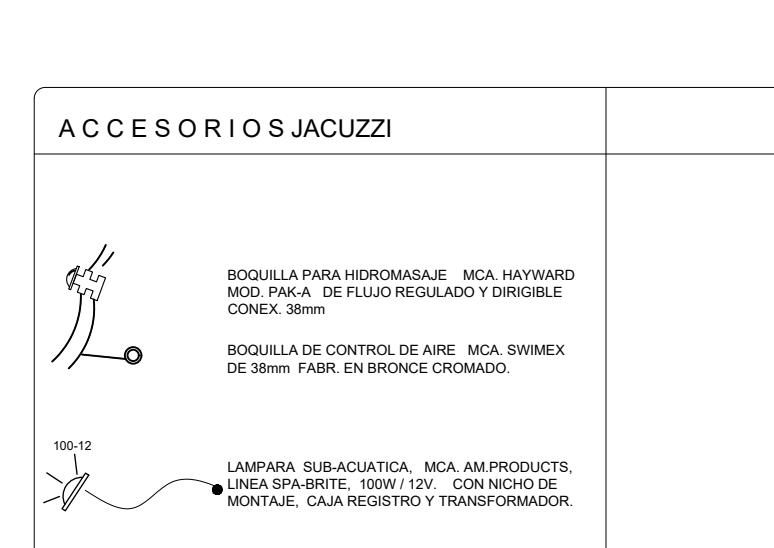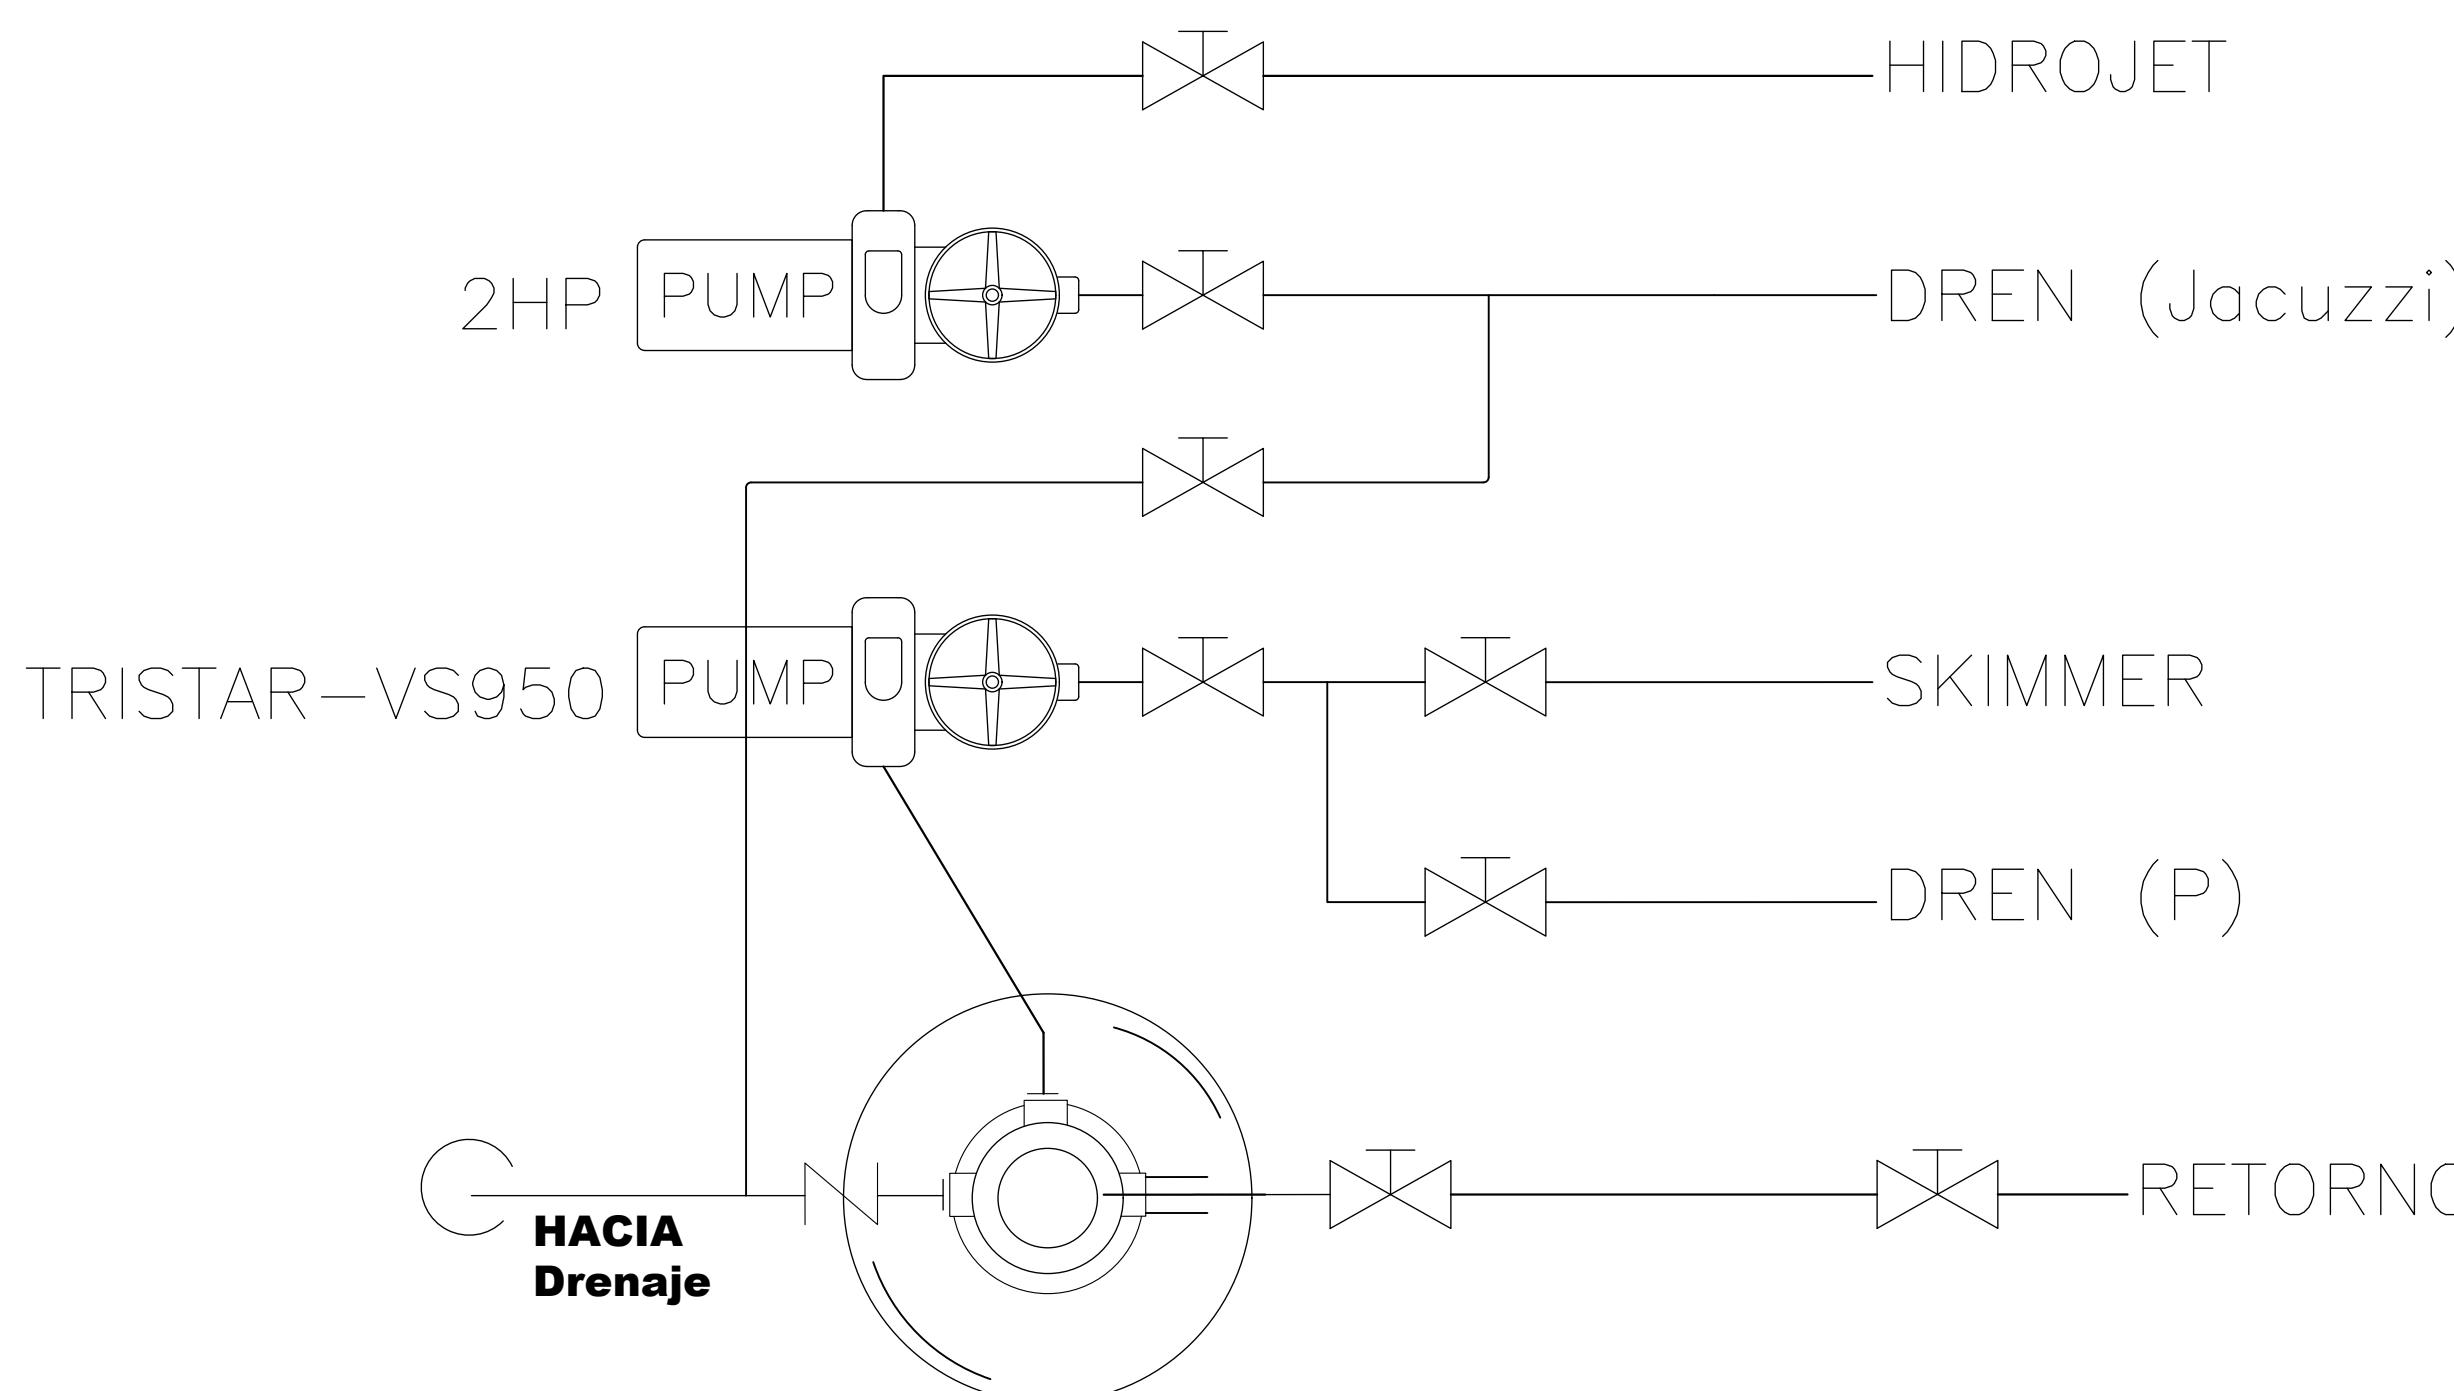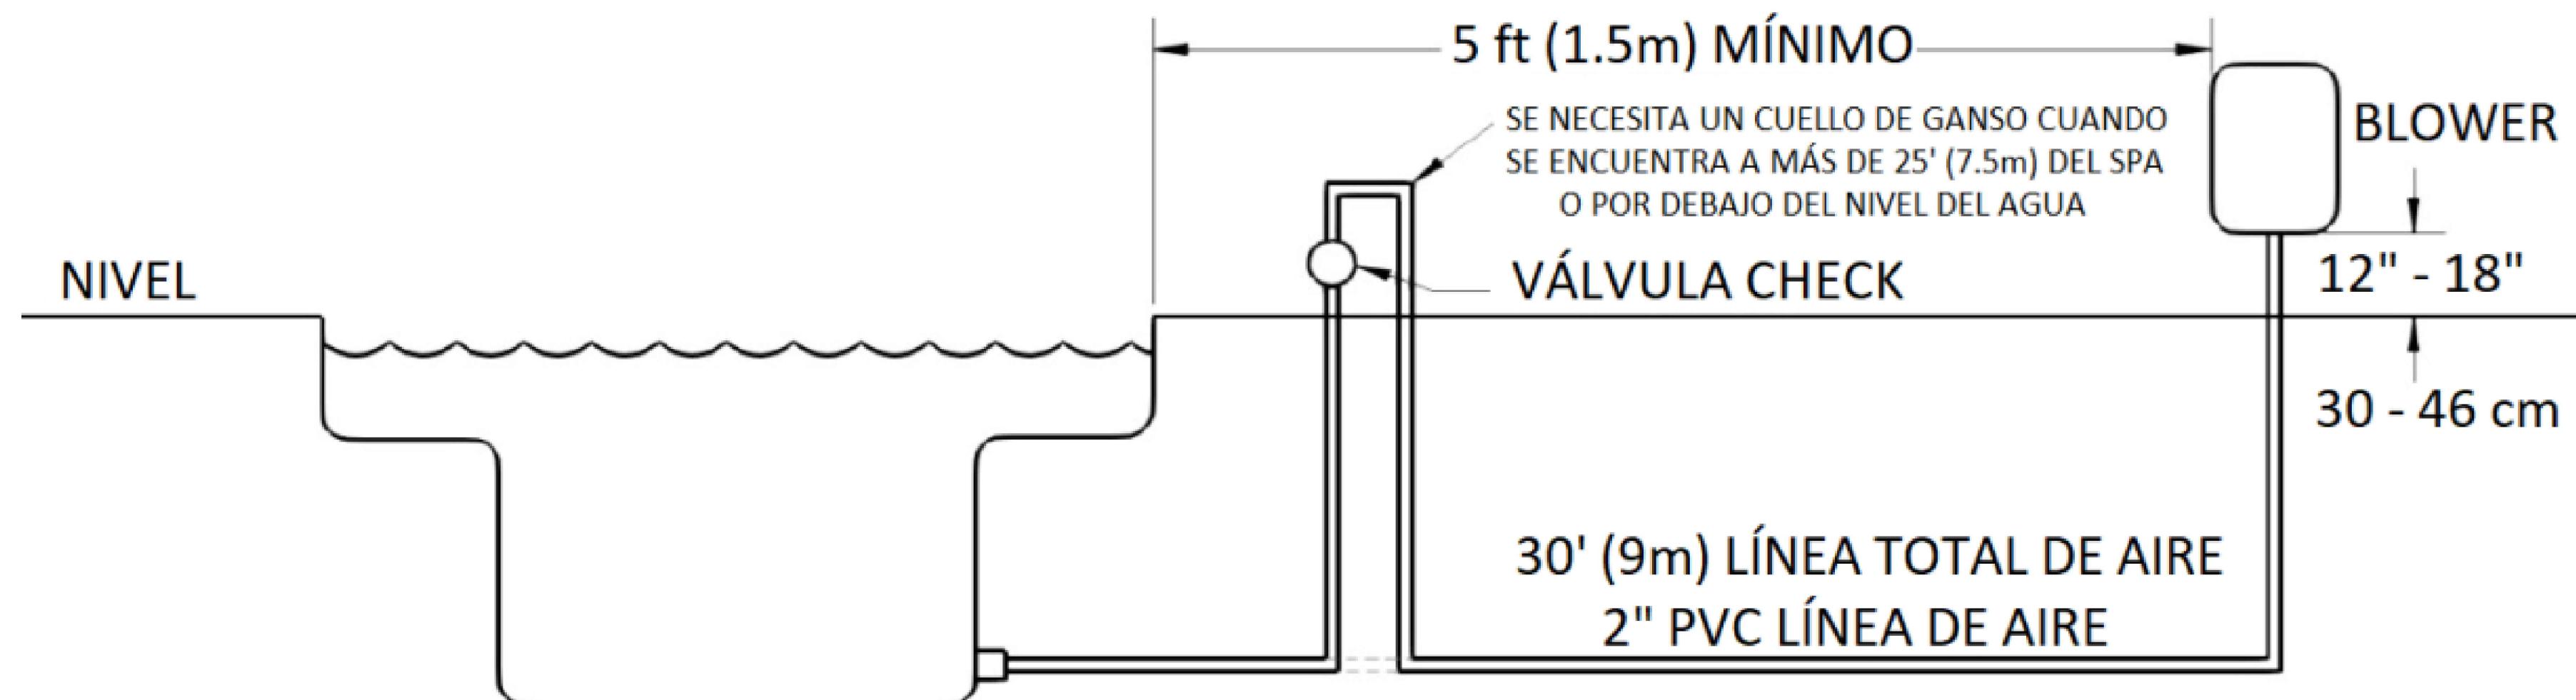

Notas:
 1) Debe seguirse las recomendaciones de su suplidor de accesorios para sellar y sujetar.
 2) El sellador, si se usa, es un elemento que se debe dar mantenimiento.

DRENAGE DE FONDO

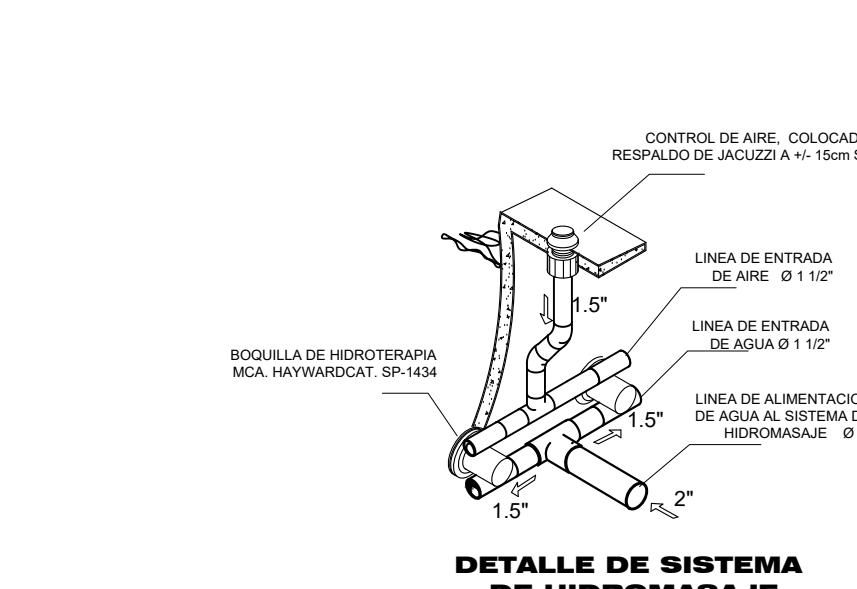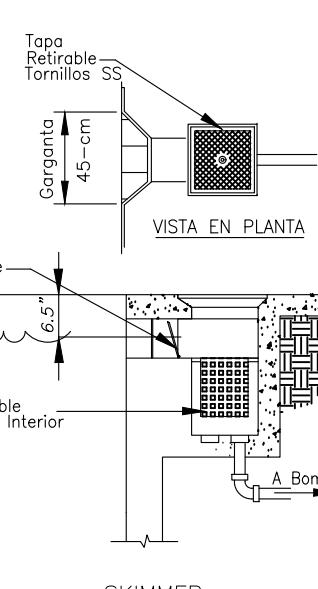

DETALLE DE SISTEMA DE HIDROMASAJE


Este proyecto es propiedad única y exclusivamente del arquitecto EDDY J. LOPEZ C. el cual sede la ejecución con estos planos de un solo proyecto en un solo lugar específico ya previamente establecido, si usted es destinatario o no de este proyecto, debe de abstenerse totalmente de copiar, reproducir, distribuir, ceder a un familiar o particular, robar conceptos del mismo. La violación a esta disposición sería procesada legalmente con todo el peso de la justicia Dominicana por violar la ley sobre derecho de autor.

ARQ. EDDY LOPEZ C. 809-399 8344

DIBUJO: EL ARQUITECTURA AVENIDA LIBERTAD #4 LA VEGA 809 573-7056 809 399-8344



FICHA: 1-9 - 2021

DATOS GENERALES	
SISTEMA DE FILTRACION PISCINA PRIVADA	
AREA DE SUPERFICIE.-	0 m ²
PROFUNDIDAD MAXIMA.-	0 m
VOLUMEN TOTAL A FILTRAR.-	22.00 m ³
TIEMPO DE RECUPERACION.-	6:00 hrs.
GASTO DE FILTRACION.-	16 GPM
ACCESORIOS	
DREN	SUCCION DE FONDO
skm	DESNAVIDOR DE SUPERFICIE, HAYWARD, CONEX. 2", CON BOCA CEDAZO Y TAPA.
Iny	BOQUILLA DE RETORNO, MCA. HAYWARD FABRICADA EN PVC BLANCO CONEX. Ø 2" CEMENTABLE.
300-12	LAMPARA SUB-AQUATICA, MCA AM PRODUCTS, LINEA AMERLITE, DE 300W / 12V. CON NICHO DE MONTAJE, CAJA REGISTRO Y TRANSFORMADOR.
BOMBA VS 950 TRISTAR	BOMBA VS 950 TRISTAR

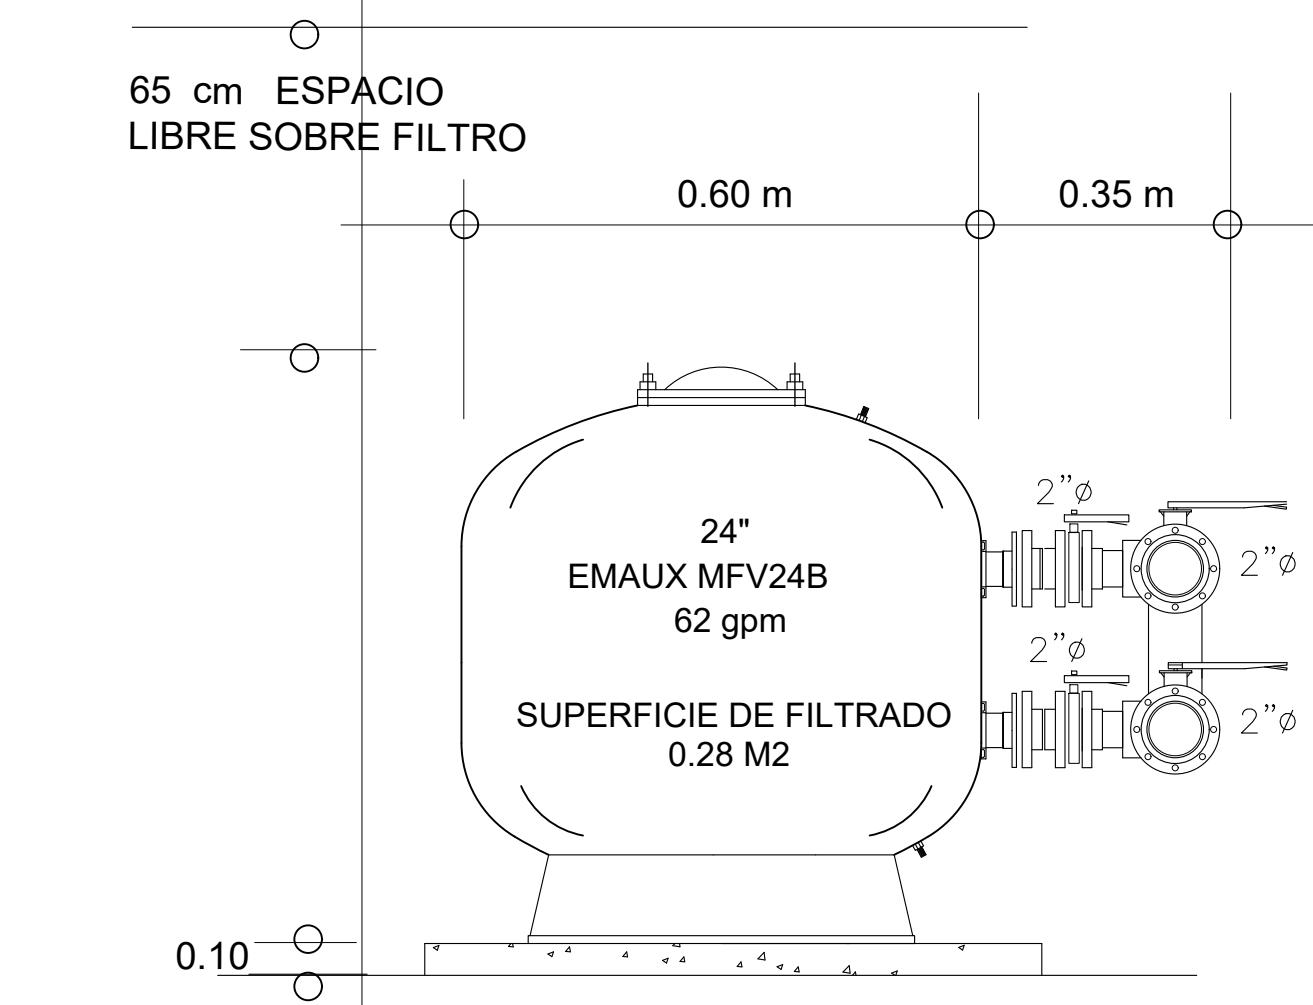

DETALLE LATERAL DE FILTRO



	Villa Beato Reyes LOCALIZACION: GUAIGUI, LA VEGA PROPIETARIOS: JOSE LUIS BEATO PEÑA CED. 402-2763926-3 FIRMA JOSELYN ANTONELIA REYES A. CED. 402-2737538-9 FIRMA
DISENO ARQUITECTONICO: SHERYL LOPEZ R. CODIA 46288	
DISENO SANITARIO: ING. FRANK FELIZ LOPEZ CODIA 19796	
DISENO ESTRUCT.: HIPOLITO MORON LILONG CODIA 4166	
DISENO ELECTRICO: HIPOLITO MORON LILONG CODIA 4166	
RESPONSABLE DEL PROYECTO: ARQUITECTO: EDDY J. LOPEZ CODIA 13.638	DIBUJO: DIBUJO: EL ARQUITECTURA AVENIDA LIBERTAD #4 LA VEGA 809 573-7056 809 399-8344
	ESCALA: INDICADA
	HOJA #: 13/23

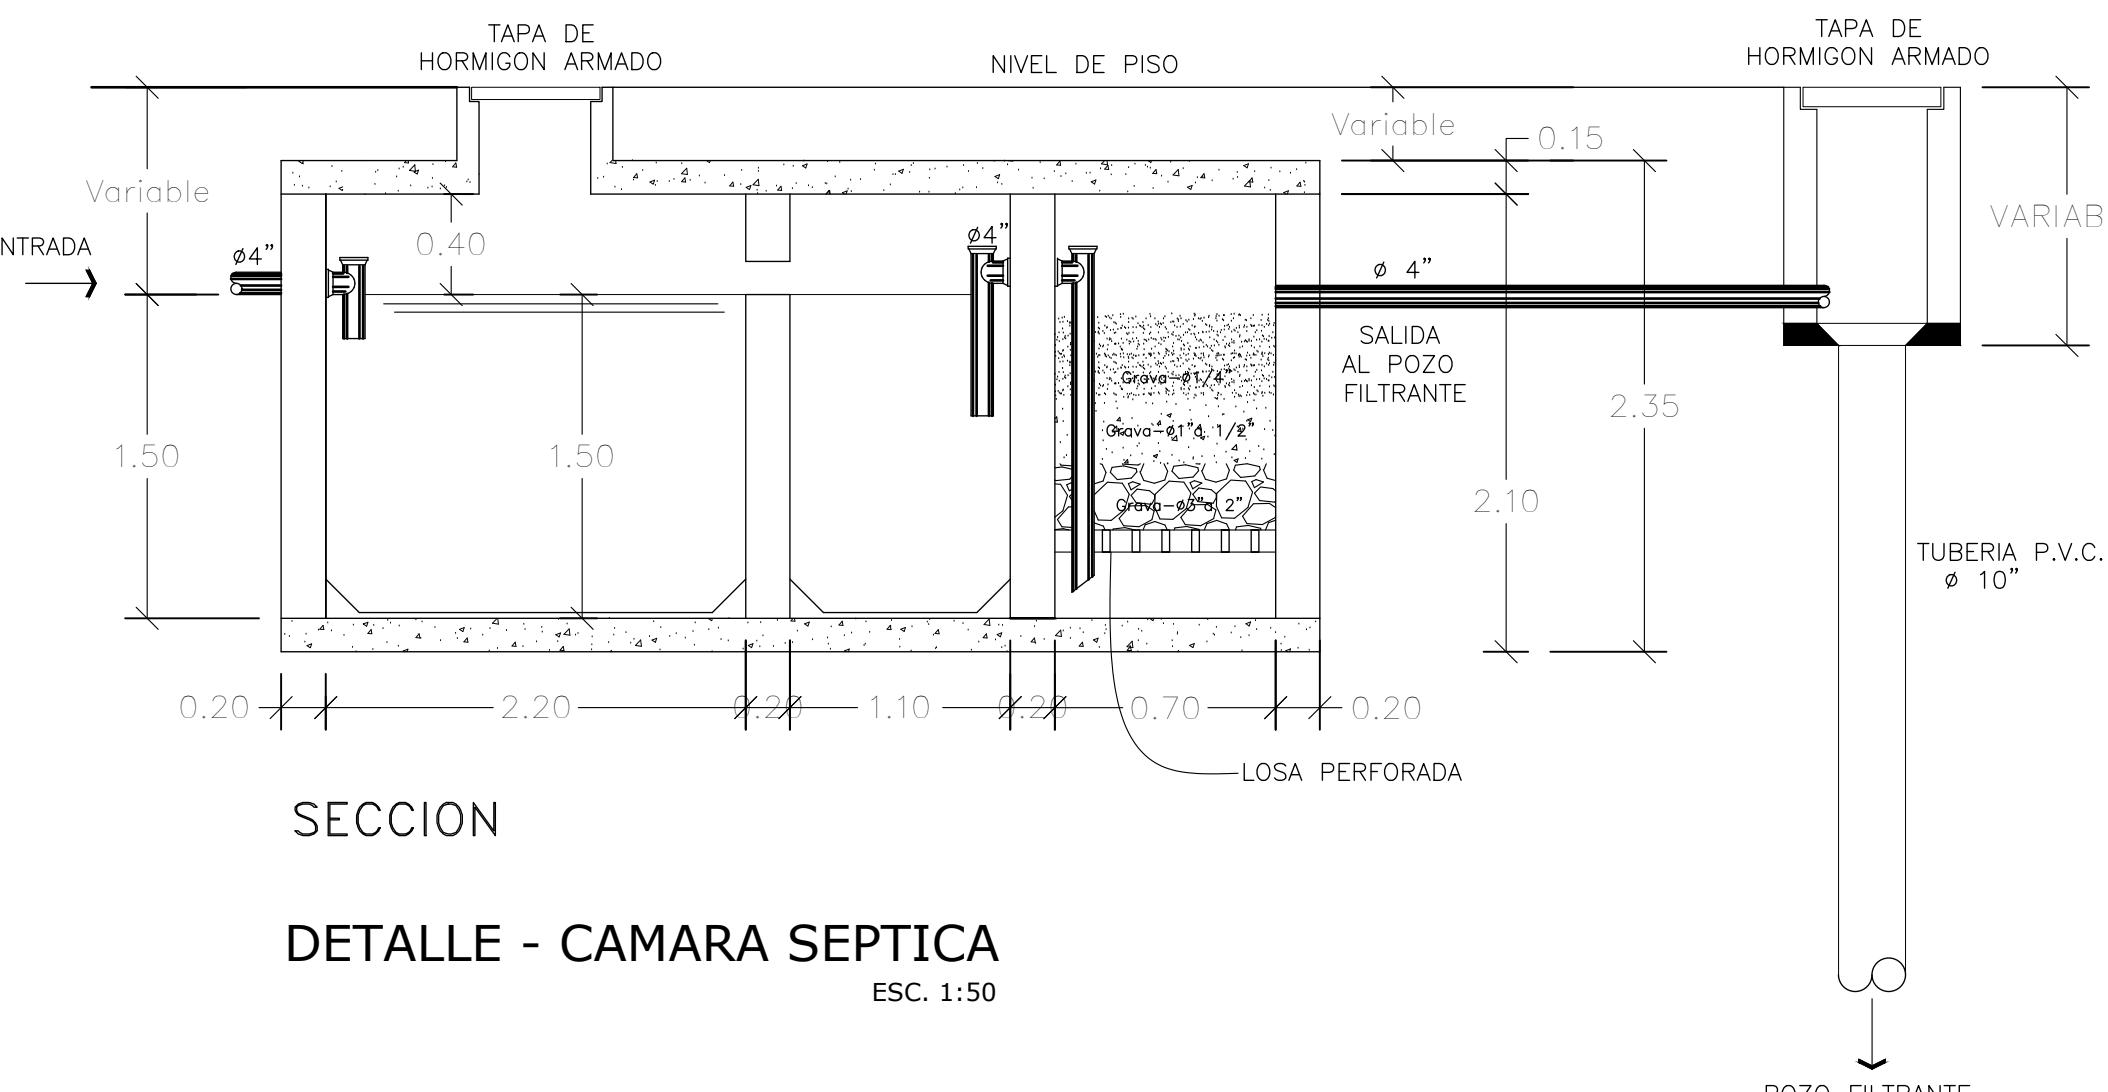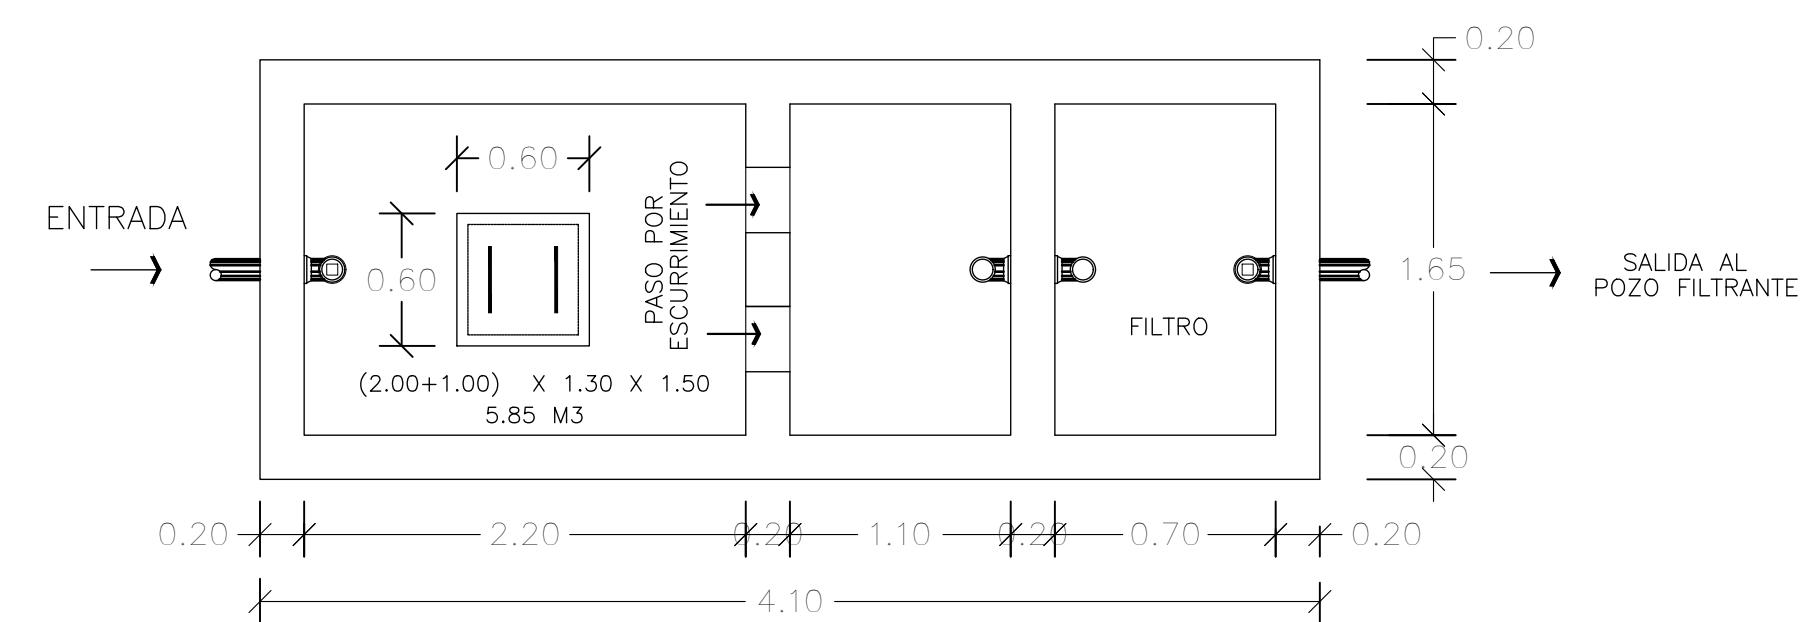

SECCION

DETALLE - CAMARA SEPTICA

ESC. 1:50

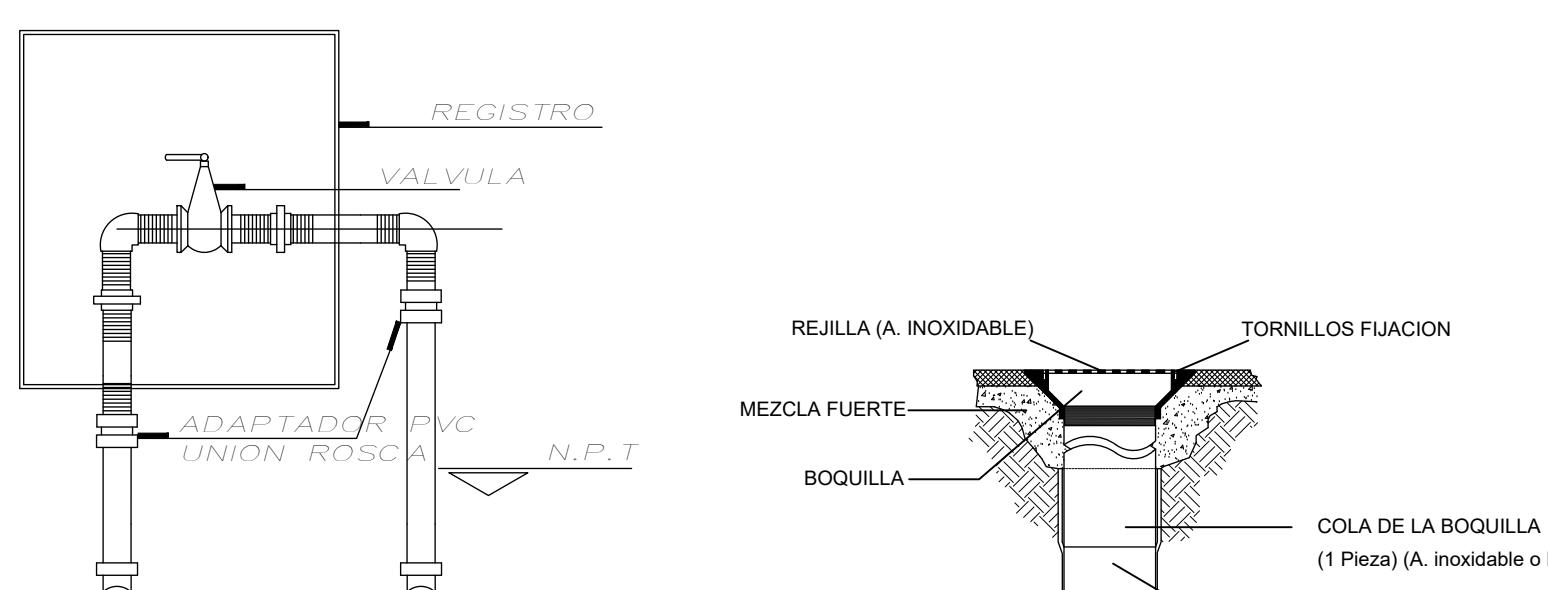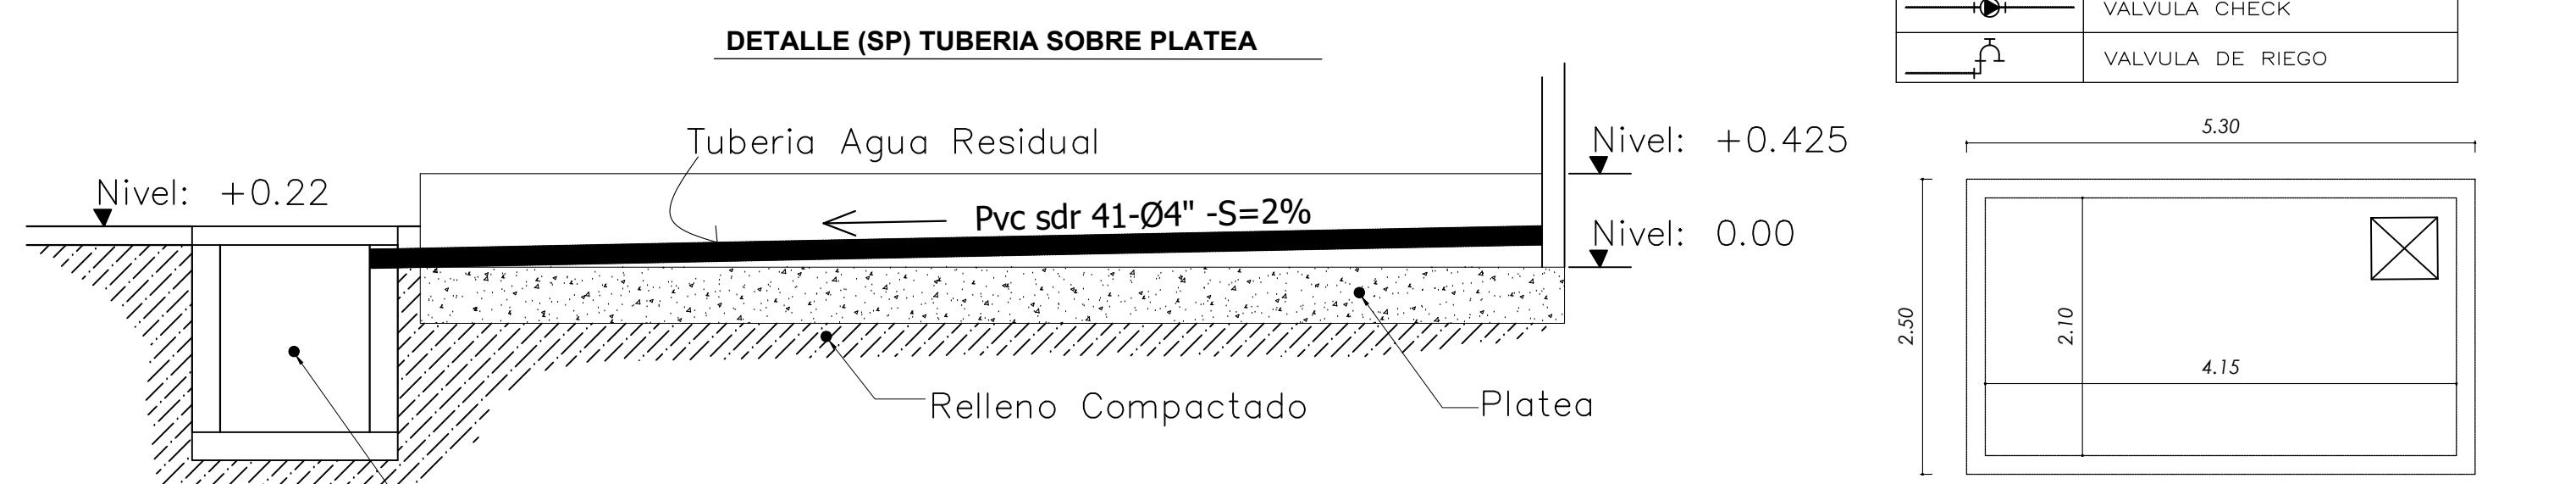

DETALLE (RE) TIPICO DE INSTALACION DE VALVULAS



REJILLA DE DESAGUE DE PISO

LEYENDA SANITARIA - DESAGÜE



CODO DE 90° SUBE	
CODO DE 90° BAJA	
CODO DE 45°	
CODO DE 90° CON VENTILACION	
CAJA DE INSPECCION	
DIRECCION DE LA PENDIENTE	
RAMAL "Y" SIMPLE	
TEE SANITARIA	
TRAMPA "P"	
SUMIDEROS DE PISO	
TUBERIA DE DESAGUE	

LEYENDA	
A G U A	
SIMBOLO	DESCRIPCION
	MEDIDOR DE AGUA
	TUBERIA DE AGUA FRIA
	TUBERIA DE AGUA CALIENTE
	TUBERIA DE IMPULSION
	CRUCE SIN CONEXION
	CODO DE 90°
	CODO DE 45°
	CODO DE 90° SUBE
	CODO DE 90° BAJA
	VALVULA DE COMPUERTA EN LA VERTICAL
	TEE
	TEE EN SUBIDA
	TEE EN BAJADA
	UNION UNIVERSAL
	UNION CON BRIDAS
	VALVULA DE COMPUERTA
	VALVULA CHECK
	VALVULA DE RIEGO



DETALLES DE PUNTOS DE AGUA Y DESAGUE

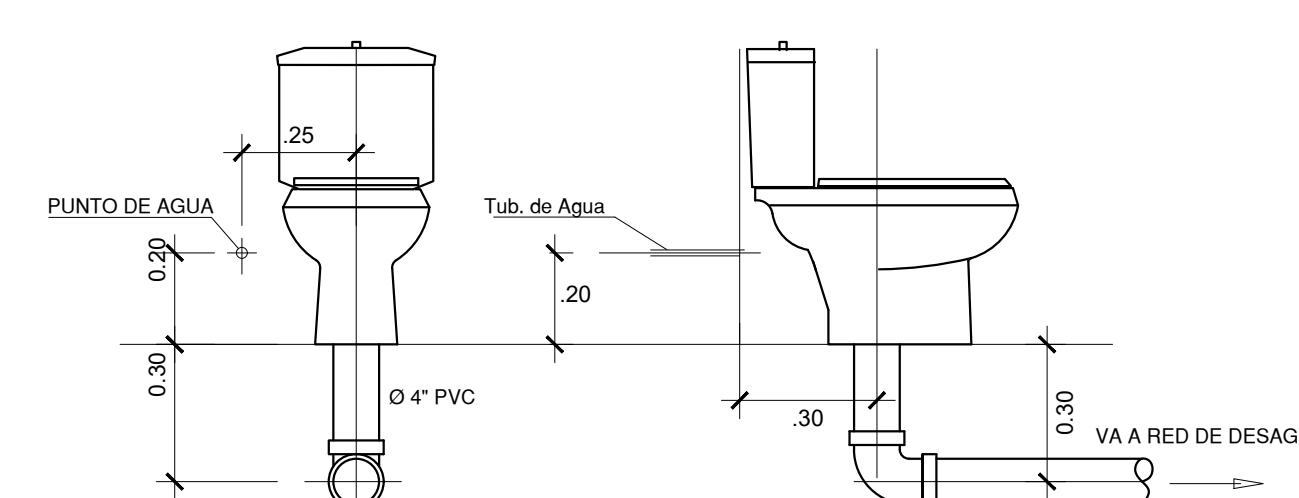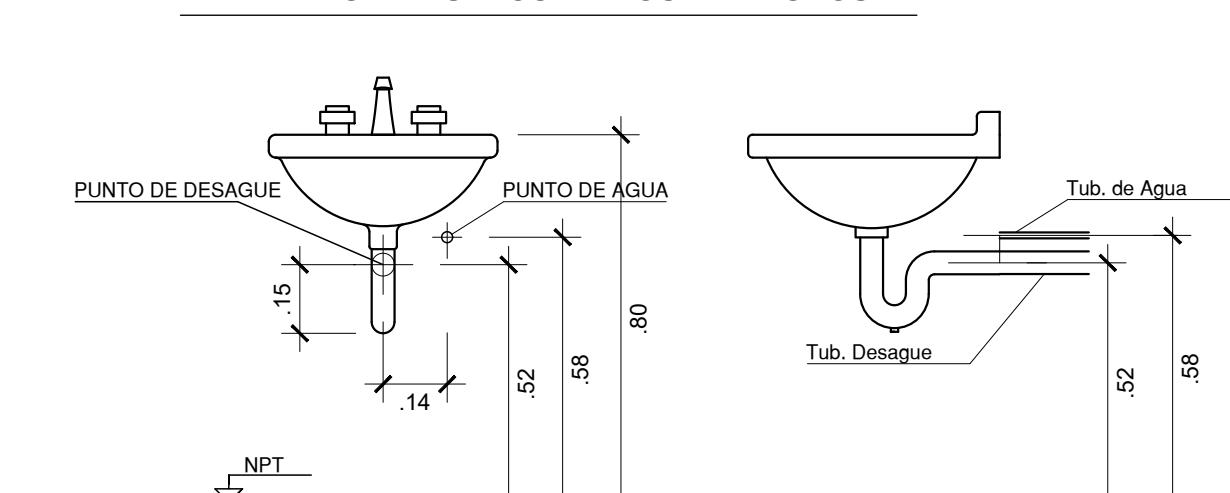


DETALLE TAPON REGISTRO (T.R.)

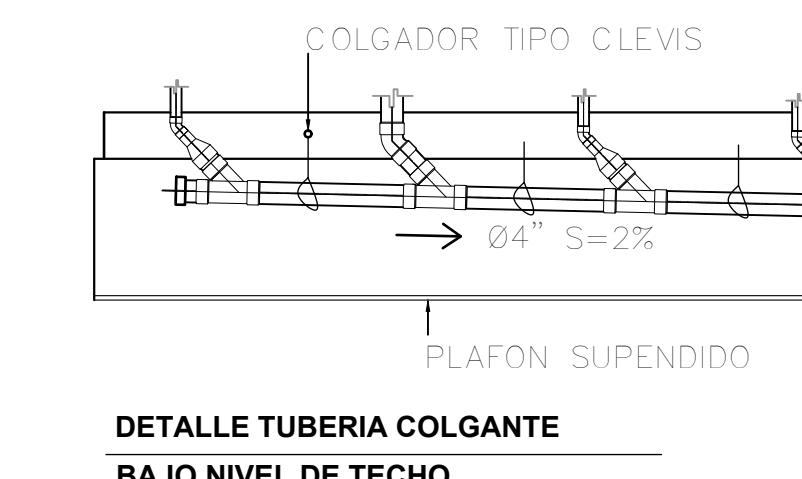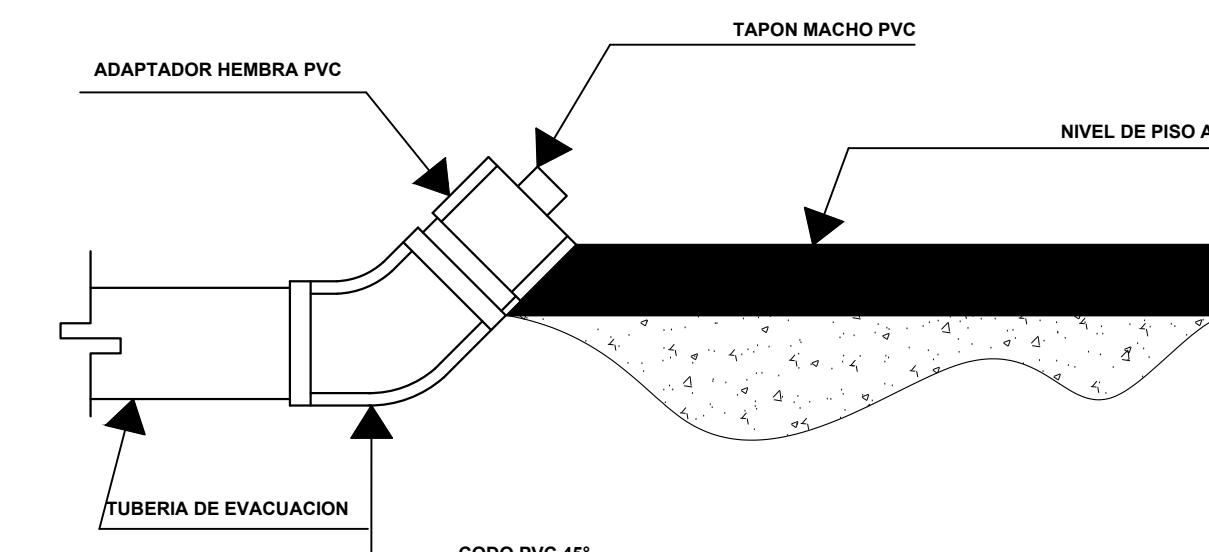


DETALLE DE INSTALACION DE CALENTADOR ELECTRICO

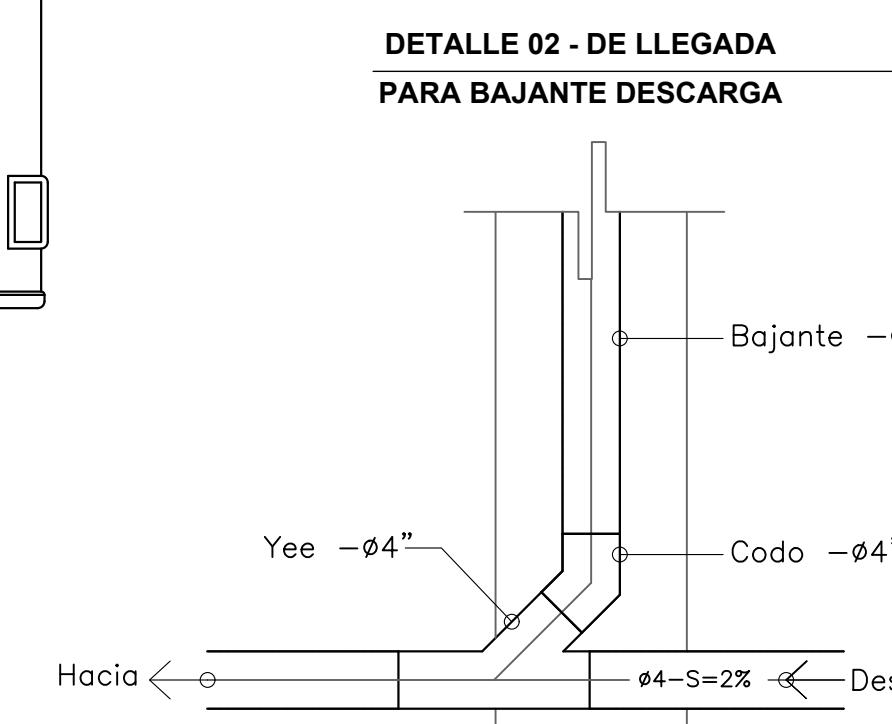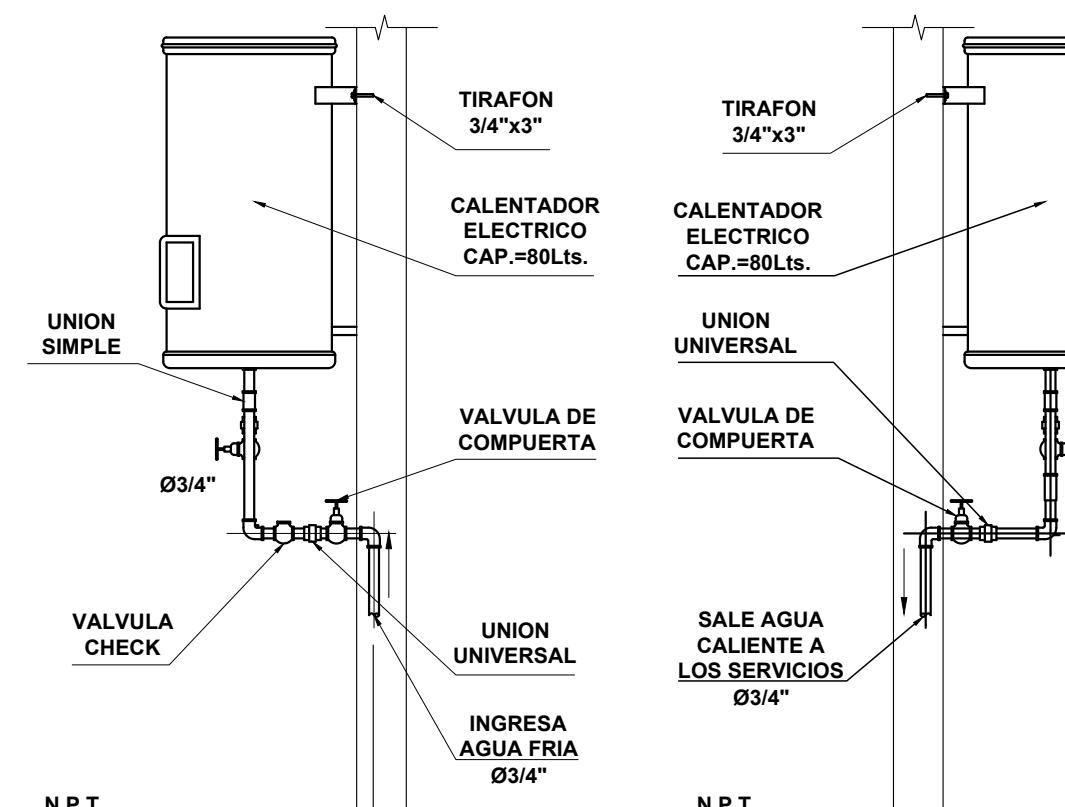

DETALLE 02 - DE LLEGADA PARA BAJANTE DESCARGA

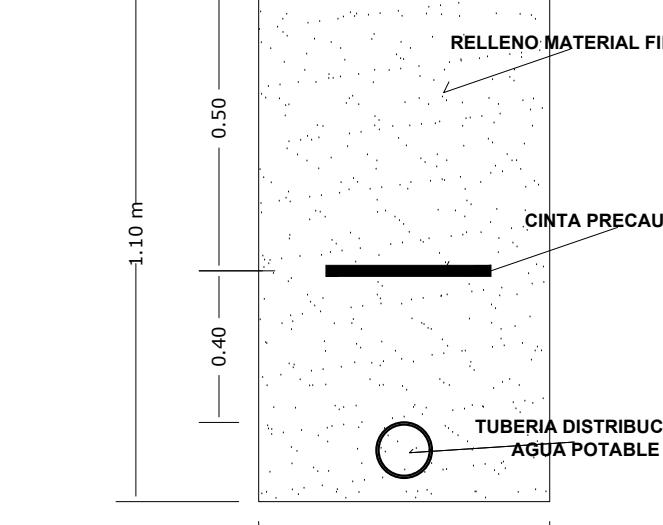

DETALLE DE CISTERNA (4600 gal/17.4m3) ESC. NO

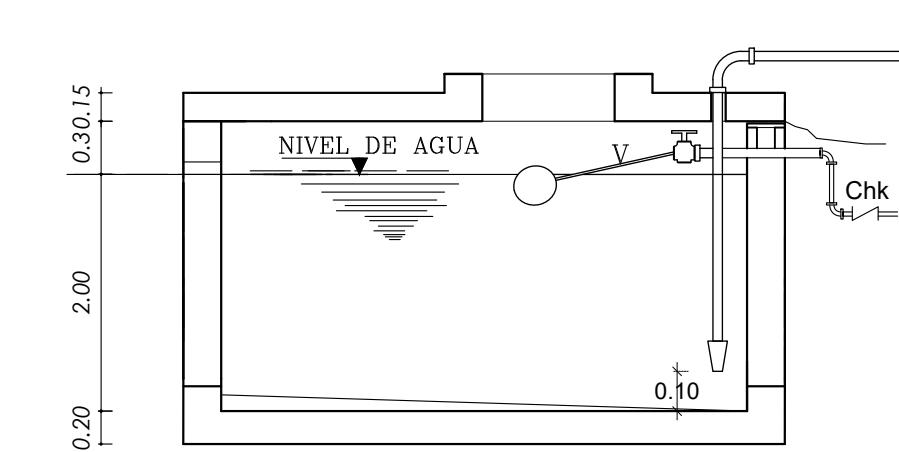

Este proyecto es propiedad única y exclusivamente del arquitecto EDDY J. LOPEZ C. el cual sede la ejecución con estos planos de un solo proyecto en un solo lugar específico ya previamente establecido. Si usted es destinatario o no de este proyecto, debe de abstenerse totalmente de copiar, reproducir, distribuir, ceder a un familiar o particular, robar conceptos del mismo. La violación a esta disposición sería procesada legalmente con todo el peso de la justicia Dominicana por violar la ley sobre derecho de autor.


EL ARQUITECTURA
ARQ. EDDY LOPEZ C.
809-399 8344


Villa Beato Reyes
LOCALIZACION: GUIGUI, LA VEGA
PROPIETARIOS:
JOSE LUIS BEATO PEÑA CED. 402-2763926-3 FIRMA
JOSELYN ANTONELIA REYES A. CED. 402-2737538-9 FIRMA
DISEÑO ARQUITECTONICO: SHERYL LOPEZ R. CODIA 46298
DISEÑO SANITARIO: ING. FRANK FELIZ LOPEZ CODIA 19796
DISEÑO ESTRUCT.: HIPOLITO MORONITA LILONG CODIA 4166
DISEÑO ELECTRICO: HIPOLITO MORONITA LILONG CODIA 4166
RESPONSABLE DEL PROYECTO: ARQUITECTO: EDDY J. LOPEZ CODIA 13638
DIBUJO: DIBUJO: EL ARQUITECTURA AVENIDA LIBERTAD #4 LA VEGA 809-573-7056 809-399-8344
FECHA: 14/23

DETALLE VIGAS


DETALLE VIGAS

DETALLE VIGAS

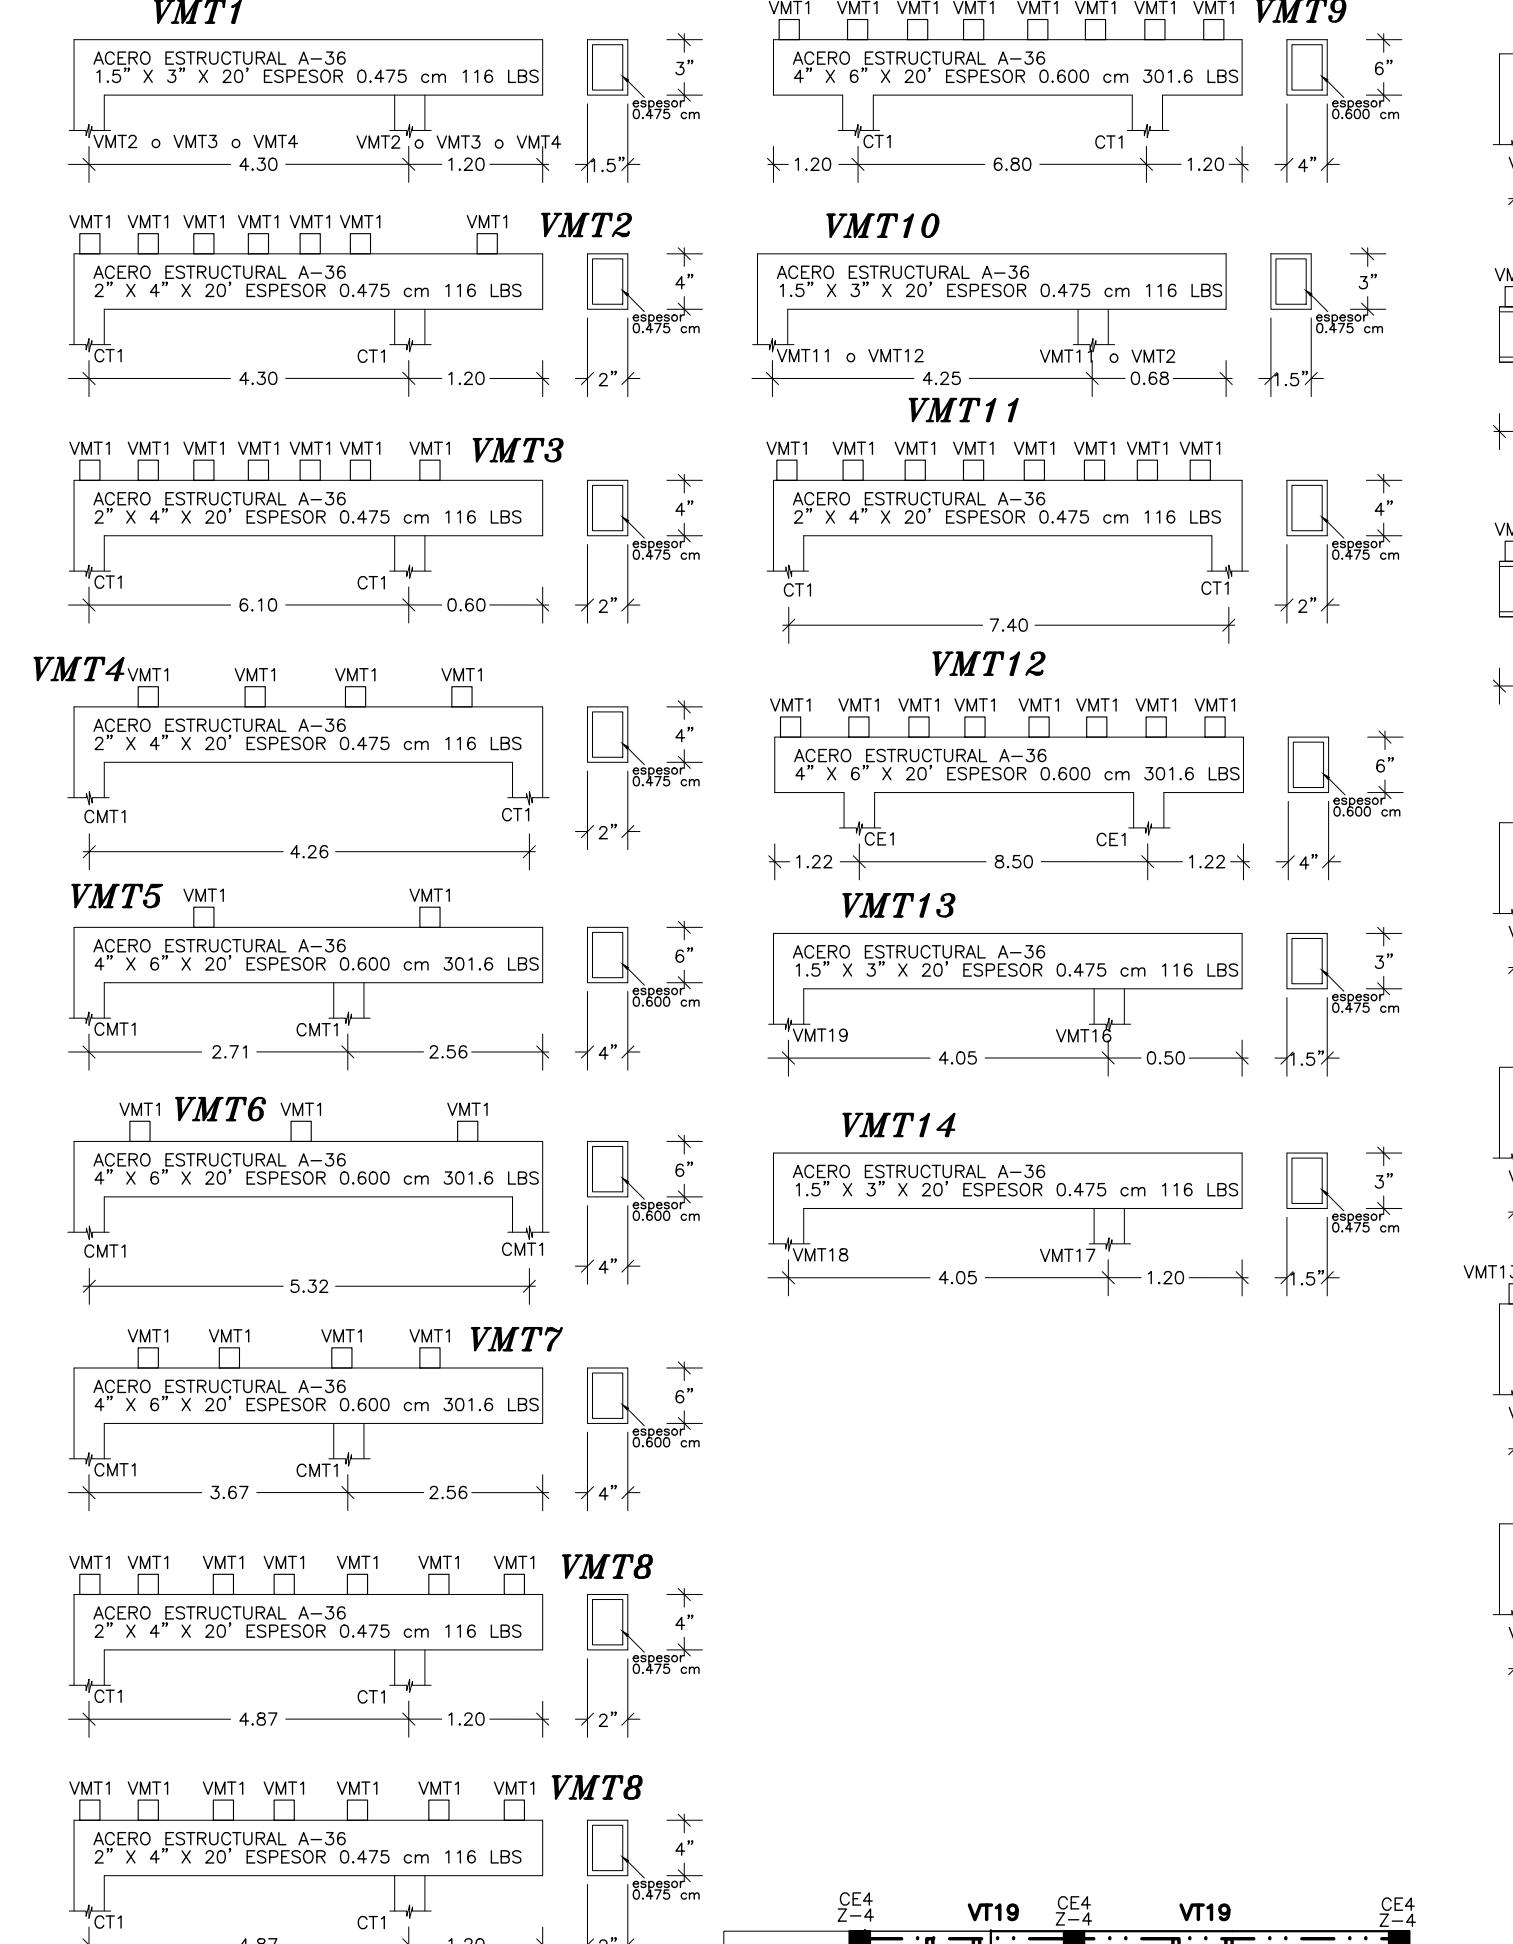


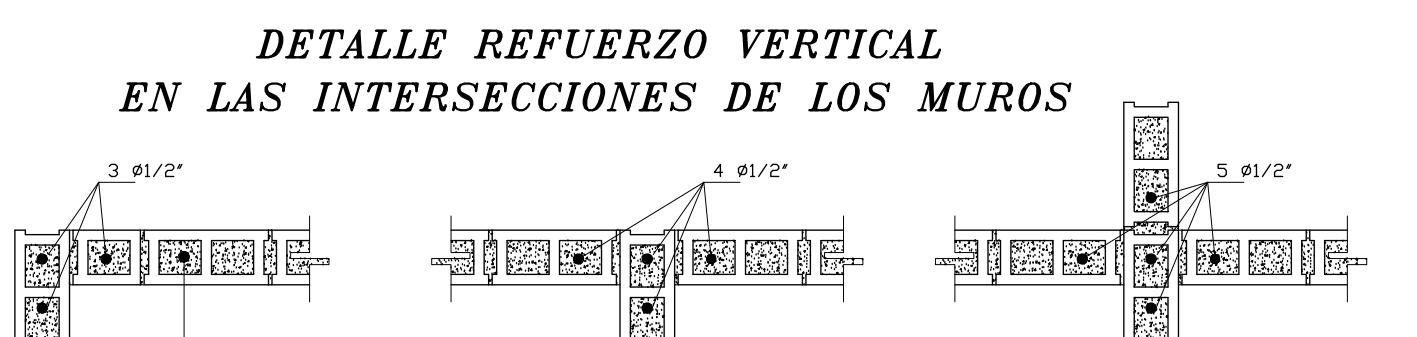




DETALLE REFUERZO HORIZONTAL EN LAS INTERSECCIONES DE LOS MUROS

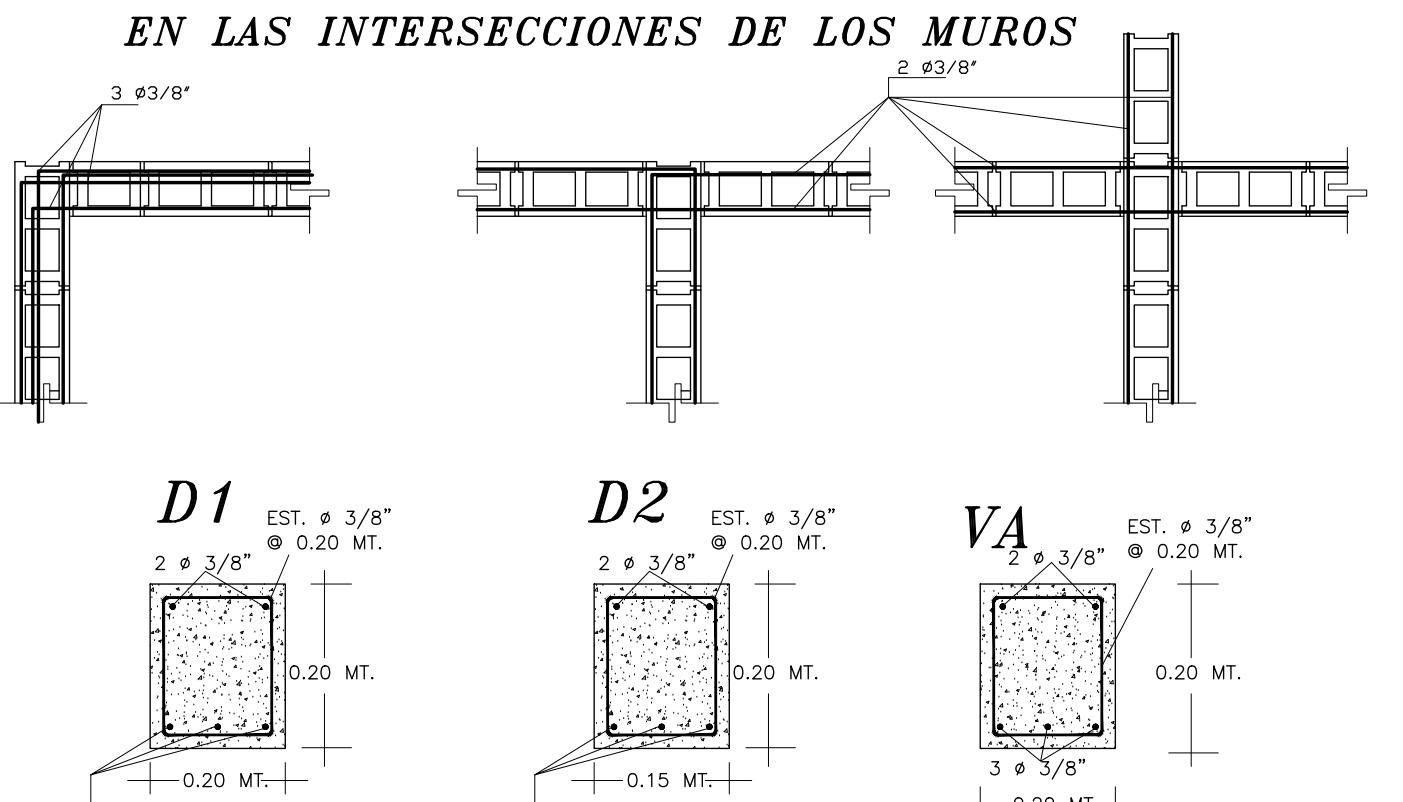

DINTEL D1

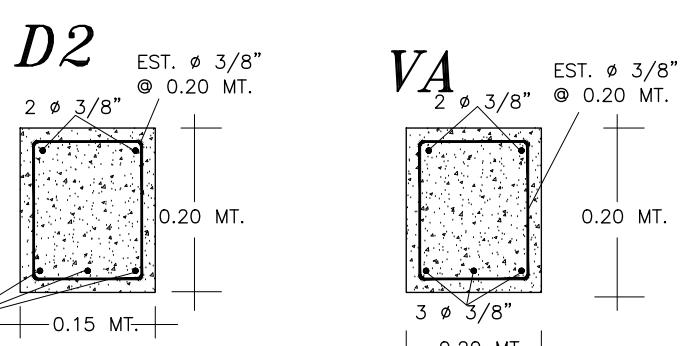


DINTEL D2

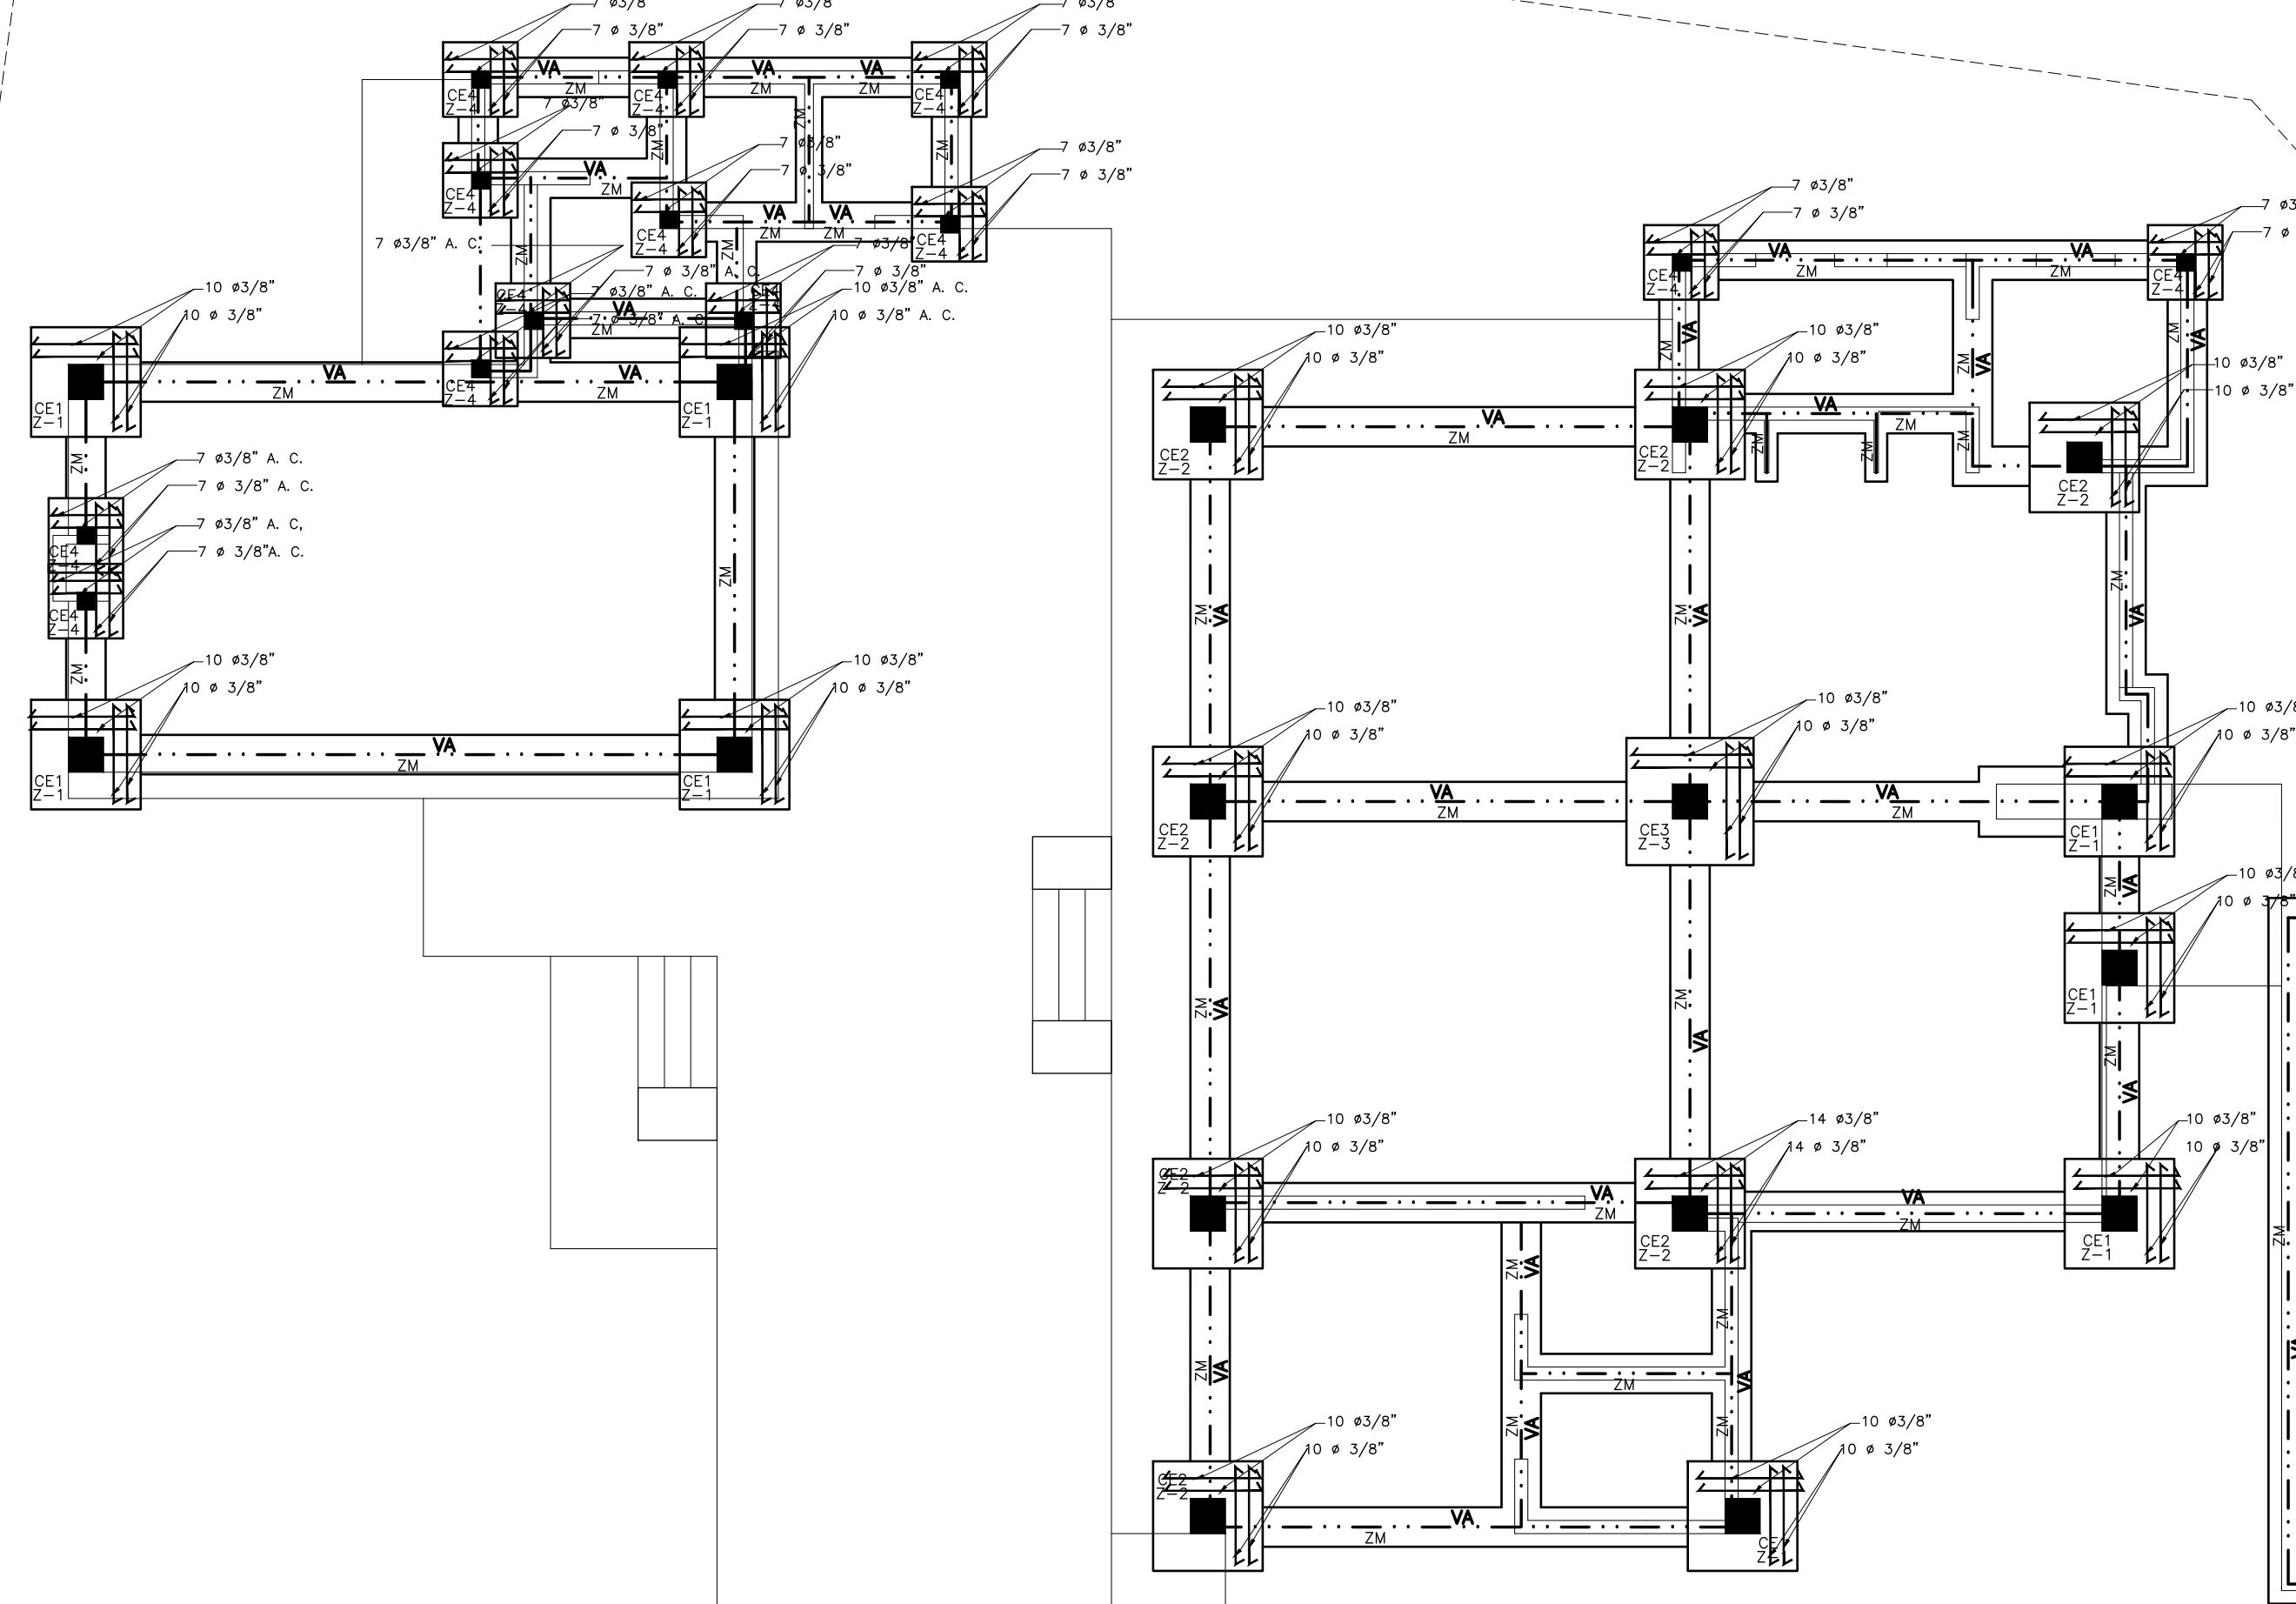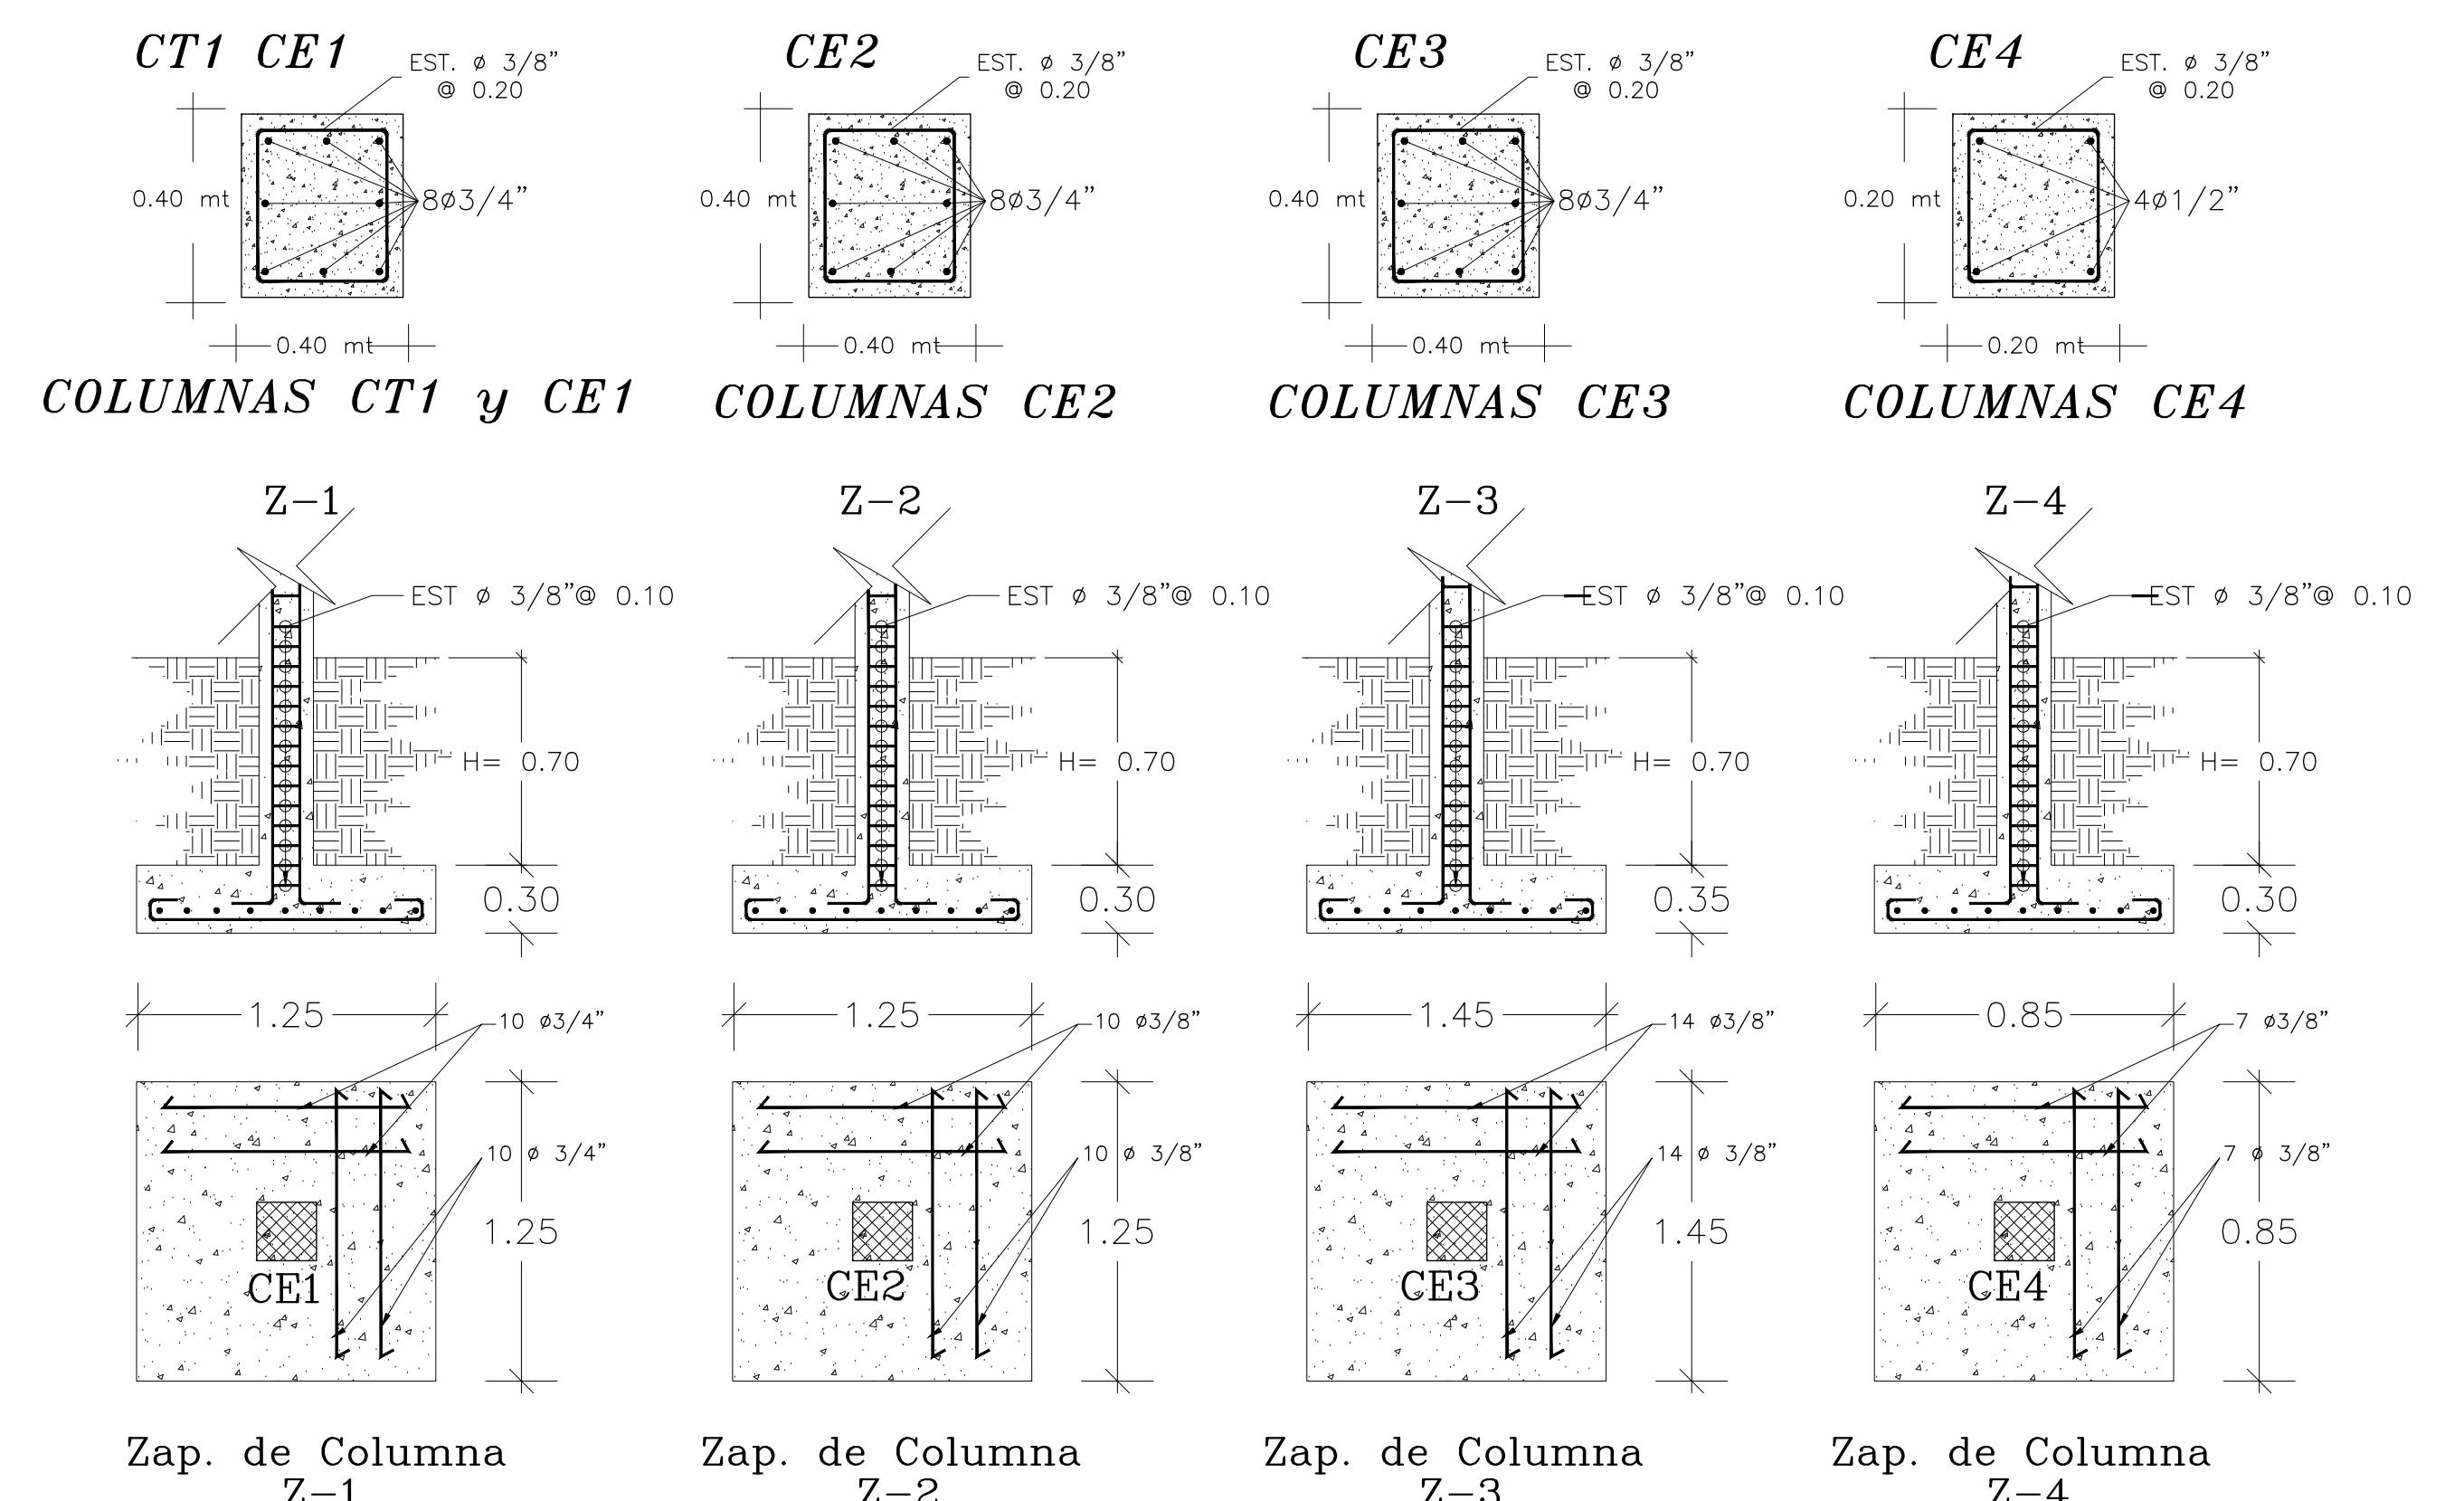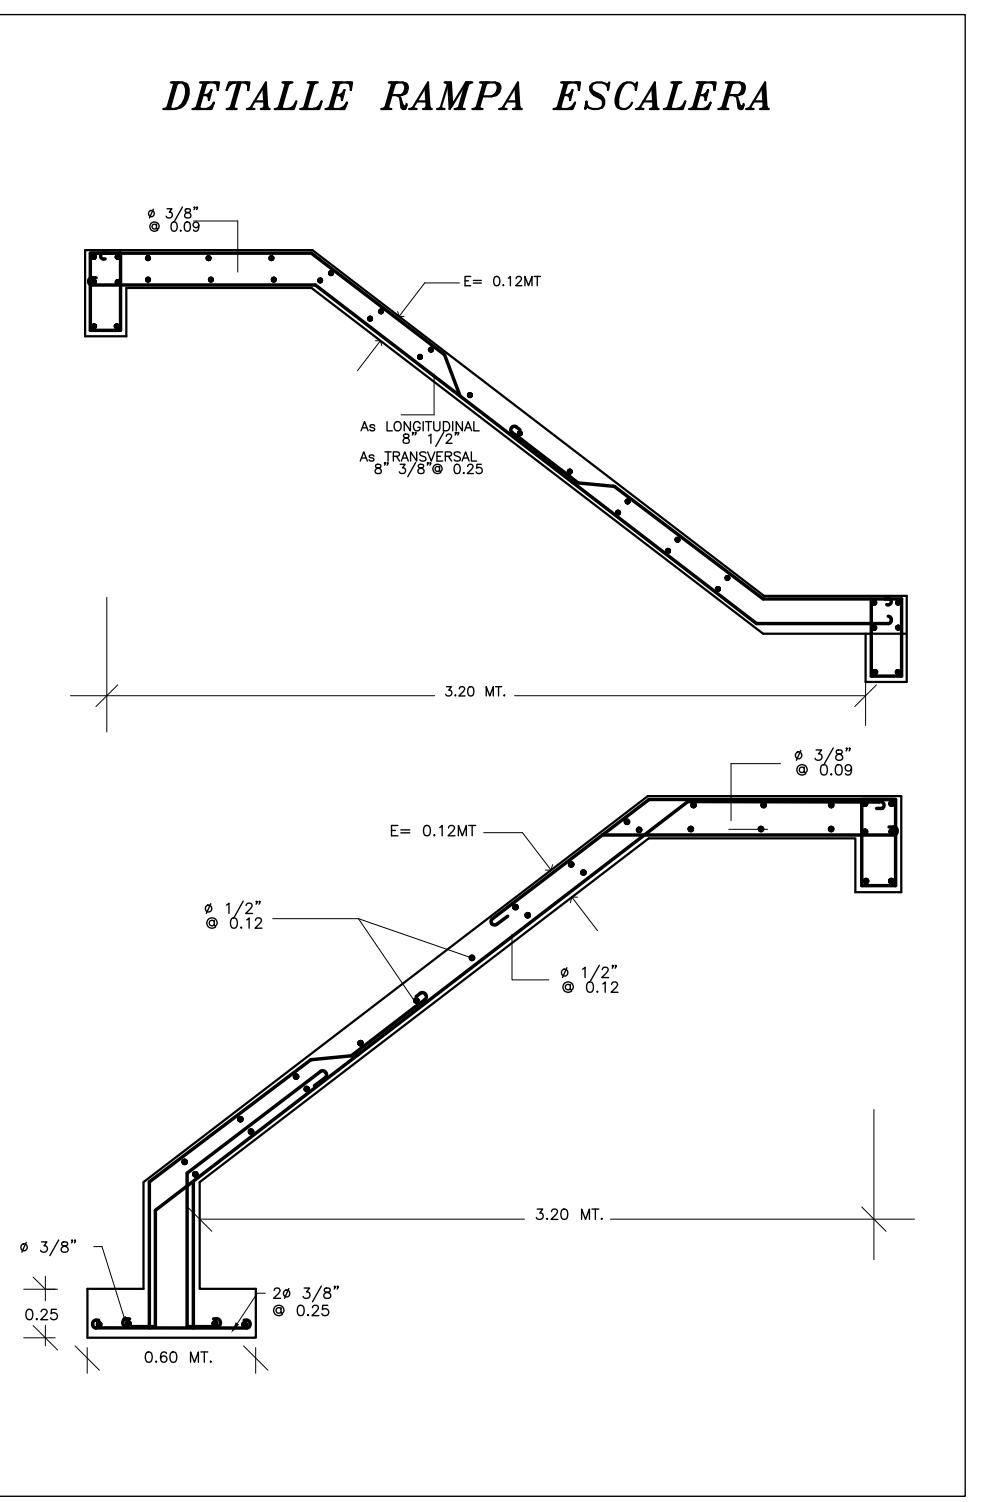

PLANTA CIMENTACION

0.20 1.00M 2.00M ESCALA: 1:75

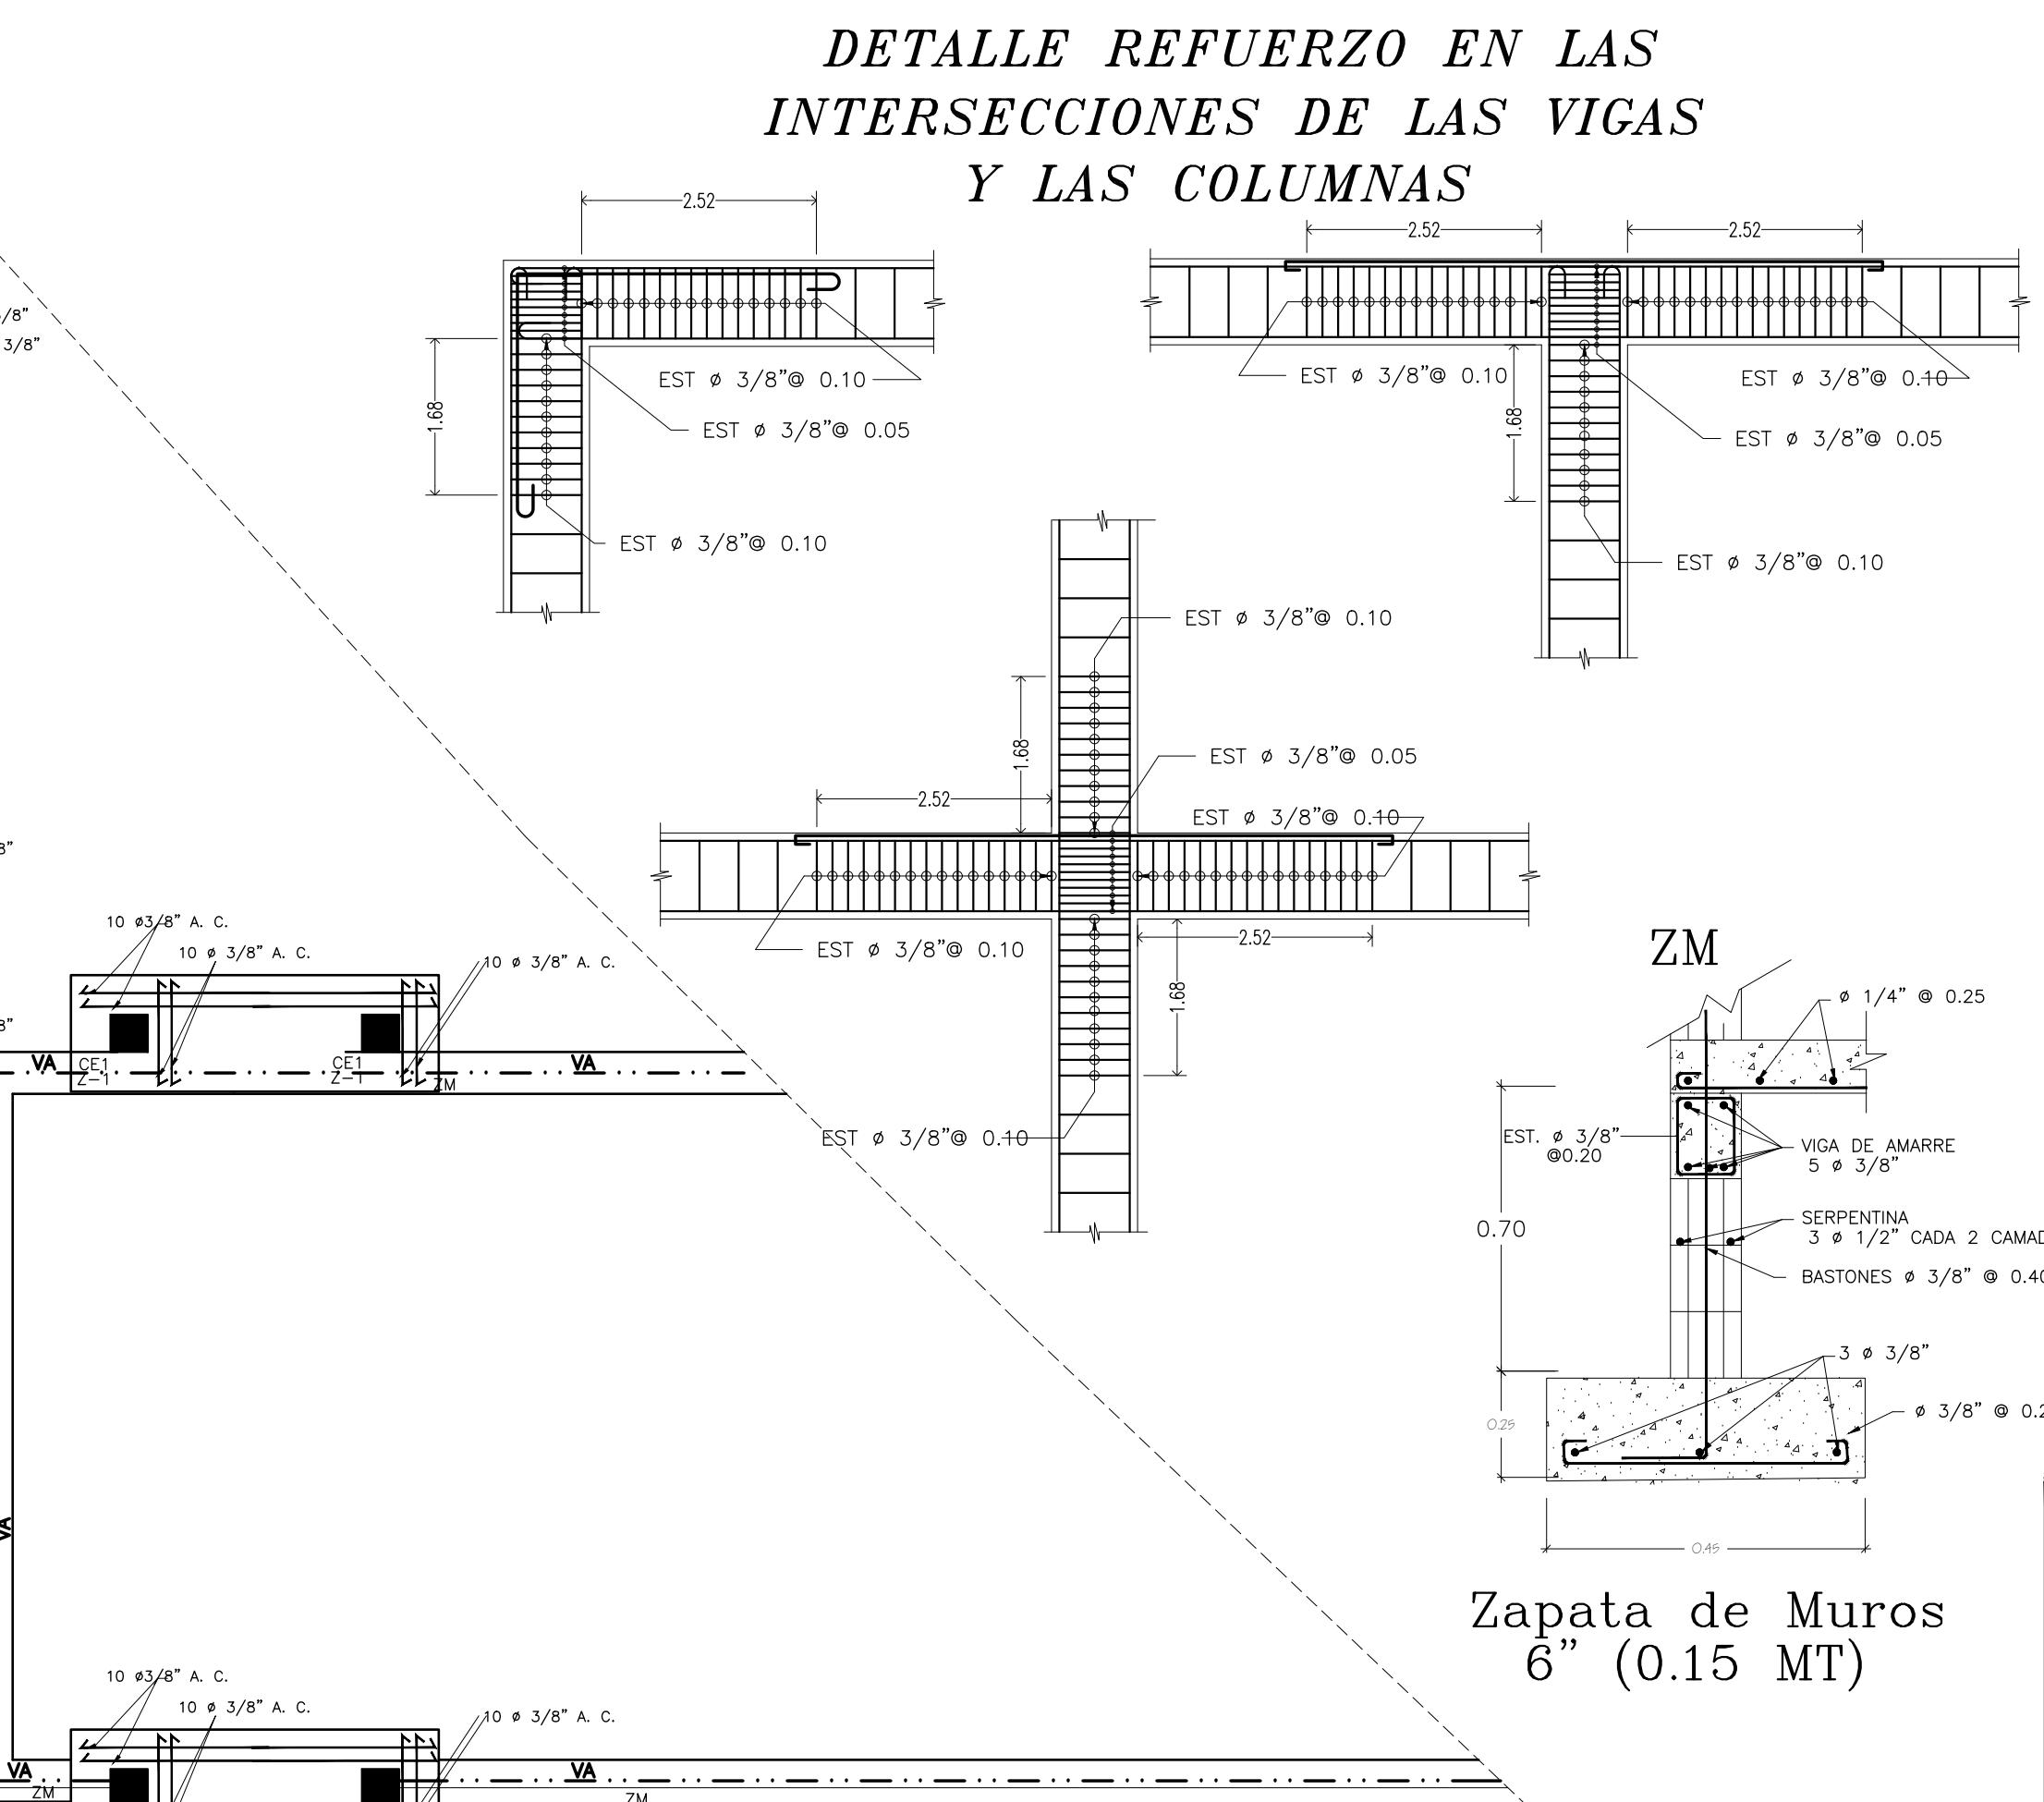

Zapata de Muros 6" (0.15 MT)

Villa Beato Reyes
LOCALIZACION: GUAIGUI, LA VEGA
PROPIETARIOS:
JOSE LUIS BEATO PEÑA CED. 402-2763926-3
JOSELYN ANTONELIA REYES A. CED. 402-2737538-9
DISEÑO ARQUITECTONICO: SHERYL LOPEZ R. CODA: 46298
ARQ. EDDY LOPEZ C. 809-399 8344
DISEÑO SANITARIO: INC. FRANK FELIZ LOPEZ CODA: 19796
DISEÑO ESTRUCT: HIPOLITO MORONTA LLONG CODA: 4166
DISEÑO ELECTRICO: HIPOLITO MORONTA LLONG CODA: 4166
DIBUJO : D 1 B U J O EL ARQUITECTURA AVENIDA INBERT #4 LA VEGA 809.573-7056 809.399-8344 CODA: 13,638
ESCALA : 1:75
HOJA # 17/23
INDICADA

DETALLE VIGAS ENTREPISO

